

Stuart
Osman

Designed by us, inspired by you.

PROPOSED RENOVATION

PROJECT CLIENT

SEEKA CONSTRUCTIONS


LOT 90 No. 356

RUFFLES RD, WILLOWVALE

JOB NUMBER

10588

STUARTOSMAN.COM.AU  

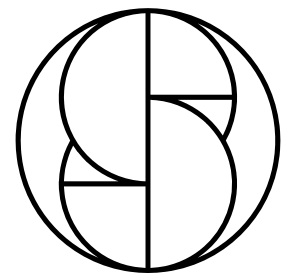

Stuart Osman



PROPOSED RENOVATION

PROJECT CLIENT

SEEKA CONSTRUCTIONS

LOT 90 No. 356

RUFFLES RD, WILLOWVALE

JOB NUMBER

10588

IMAGES ARE DIAGRAMMATIC ONLY - REFER TO ELEVATIONS FOR DETAILS

JOB NUMBER **10588**

[illegible]

STAIR REQUIREMENTS : MIN. TREAD 240mm, MIN. RISER 115mm, MAX. RISER 190mm, SPACE BETWEEN OPEN TREADS MAX. 125mm. TREADS TO BE NON SLIP SURFACE.
BALUSTRADES : MIN. 1000mm ABOVE LANDINGS WITH MAX. OPENING OF 125mm AND IN ACCORDANCE WITH N.C.C 11.3

NCC	NATIONAL CONSTRUCTION CODE	PC ALUM.	POWDERCOATED ALUMINIUM
	SERIES OF AUSTRALIA	CP	COVERPLATE
AS	AUSTRALIAN STANDARDS	PS	PLUMBING STACK / DUCT
AHD	AUSTRALIAN HEIGHT DATUM	CJ	CONSTRUCTION JOINT
RL	RELATIVE LEVEL	LB	LOAD BEARING
FL	FLOOR LEVEL	OHC	OVER HEAD CUPBOARD
FFL	FINISHED FLOOR LEVEL	GAS F.S	GAS FREE STANDING OVEN
AFFL	ABOVE FINISHED FLOOR LEVEL	UBO	UNDER BENCH OVEN
NGL	NATURAL GROUND LINE	WO	WALL OVEN
FSR	FLOOR SPACE RATIO	REF	REFRIGERATOR
T.B.C	TO BE CONFIRMED	DW	DISHWASHER
DP	DOWNPIPE	MW	MICROWAVE
FP	FIRE PLACE	APPL	APPLIANCE
FW	FLOOR WASTE	WM	WASHING MACHINE
HWS	HOT WATER SYSTEM	WIR	WALK-IN-ROBE
AC	AIR CONDITIONING	CSD	CAVITY SLIDING DOOR
SP	STEEL POST	FSD	FACE SLIDING DOOR

JOB NUMBER: 10588

© Copyright reserved in part or whole.
THIS DESIGN IS THE EXCLUSIVE PROPERTY
OF STUART OSMAN
N.B. ALL WRITTEN DIMENSIONS TAKE
PRECEDENCE OVER SCALED SIZES
Contractor to verify dimensions. Notify
designers of discrepancies. Failure to do so
shall void the designers responsibilities.
ALL dimensions to structure only - finishes
excluded. BE WARNED: SUBSTITUTION OF
ANY STRUCTURAL MEMBERS, AND OR ANY
VARIATION TO ANY PART OF THE DESIGN
WILL VOID ANY RESPONSIBILITIES OF STUART
OSMAN FOR THE STRUCTURAL INTEGRITY
AND PERFORMANCE OF THE BUILDING.

PRELIMINARY PLANS ONLY NOT FOR CONSTRUCTION



SITE PLAN - EXISTING SURVEY
SCALE 1:200 SHEET 4 OF 24 JOB NUMBER - 10588


NORTH POINT WARNING
The north point shown refers to the subject survey plan. The user should ensure this is suitable for their purposes.



- SERVICES ALERT**
Boyd & Moore take no responsibility for the location of non-visible services.
- SEWERAGE, WATER & STORMWATER**
Sewerage, water and Stormwater information has been sourced from Local Authority Infrastructure Asset Mapping and located by field survey where possible.
- IDENTIFICATION SURVEY ALERT**
The detail survey does not guarantee the location of boundary pegs or fences. Please contact this office for further advice.
- FLOOD SEARCH ALERT**
Boyd & Moore has not obtained a flood search on this property. Check Council for any flood information.
- GROUND LEVEL**
The levels shown were observed on the surveyed date and may not represent the Local Authority's definition of Ground Level. Please contact this office for further advice.
- TITLE SEARCH ALERT**
Boyd & Moore have not carried out a title search for this survey. Check DNR&M for easements and encumbrances.

SERVICES		BOYD & MOORE PTY LTD		DETAIL SURVEY		F.BOOK	L.BOOK
Electricity	Overhead	ACN 109 294 260		PART LOT 90 ON SP206282		F.WORK	SG
Water	Yes	SURVEYORS		No. 356 RUFFLES ROAD		DATE	7-04-2026
Sewer	Septic	PO BOX 3060		WILLOW VALE		JOB No.	5959
Telecom	Yes	NERANG QLD 4211		LOCAL GOVT : GOLD COAST CITY		SCALE 1 : 250 @ A1	
Stormwater	to Road	Office - 24 GALAPAGOS WAY,		LEVEL DATUM : AHD DERIVED FROM		DRAWING NUMBER	
Gas	-	PACIFIC PINES QLD 4211		PM113726 RL 55.942m AHDD		5959-1-A1	
Kerb	-	Ph/Fax: (07) 55804205					
Footpath	-	Email: boydsurv@bigpond.net.au					
Flood Aff	Search Recommended						

NOTES:
*ALL dimensions to structure only - finishes excluded.
*ALL stormwater & drainage to be in compliance with N.C.C parts 3.3.5 & 7.4, as well as ASNZS3500.
*Discharge stormwater to TANK, where possible, ALL other stormwater & overflow to kerb & channel. In accordance with local government requirements & standards.
*2 Downpipes Max. to each 100mm stormwater pipe, subsurface pipes to be 100mm diameter, any underslab piping to have an inspection opening at upper end, then to be 100mm sewer grade piping with no joins under slab.
*Gutters to be 125mm D-section colorbond gutters.
*ALL driveway & VXO grades to local government requirements & standards.
*Provide sediment control to site where required.
*Meter box position T.B.C on site.
ALL retaining walls by owner.

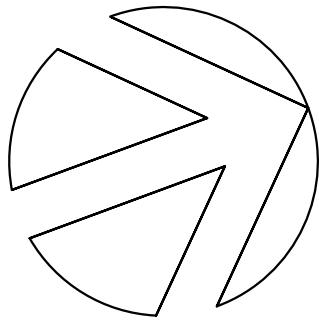

G.L	RL **.
CUT	****mm
FILL	****mm
F.L	RL **.

approx.

PROPOSED DEVELOPMENT DETAILS

SITE AREA - 8657m2
OVERALL BUILDING FOOTPRINT - 587.80m2
SITE COVERAGE - 587.80m2 / 8657 = (6.79%)



P 07 55 203 022
E design@stuartosman.com.au

Studio 2/71 Township Dr,
West Burleigh, QLD 4219

PO BOX 2845
Burleigh Heads DC QLD 4220

ABN 73 097 995 616
QBCC License No: 1129687



PROPOSED RENOVATION

BUILDER:SEEKA CONSTRUCTIONS

CLIENT: SEEKA CONSTRUCTIONS

PROJECT: LOT 90 No. 356
RUFFLES RD
WILLOWVALE

DRAWN BY: EP/RS

CHECKED BY: SO

DESIGN: CUSTOM

DATE: A01/05/2026


SCALES: 1:500 @ A3

AMENDMENTS:
B250526, C020726,

SHEET NUMBER: 5 of 24

JOB NUMBER: 10588

© Copyright reserved in part or whole.
THIS DESIGN IS THE EXCLUSIVE PROPERTY
OF STUART OSMAN
N.B ALL WRITTEN DIMENSIONS TAKE
PRECEDENCE OVER SCALED SIZES
Contractor to verify dimensions. Notify
designers of discrepancies. Failure to do so
shall void the designers responsibilities.
ALL dimensions to structure only - finishes
excluded. BE WARNED: SUBSTITUTION OF
ANY STRUCTURAL MEMBERS, AND OR ANY
VARIATION TO ANY PART OF THE DESIGN
WILL VOID ANY RESPONSIBILITIES OF STUART
OSMAN FOR THE STRUCTURAL INTEGRITY
AND PERFORMANCE OF THE BUILDING.

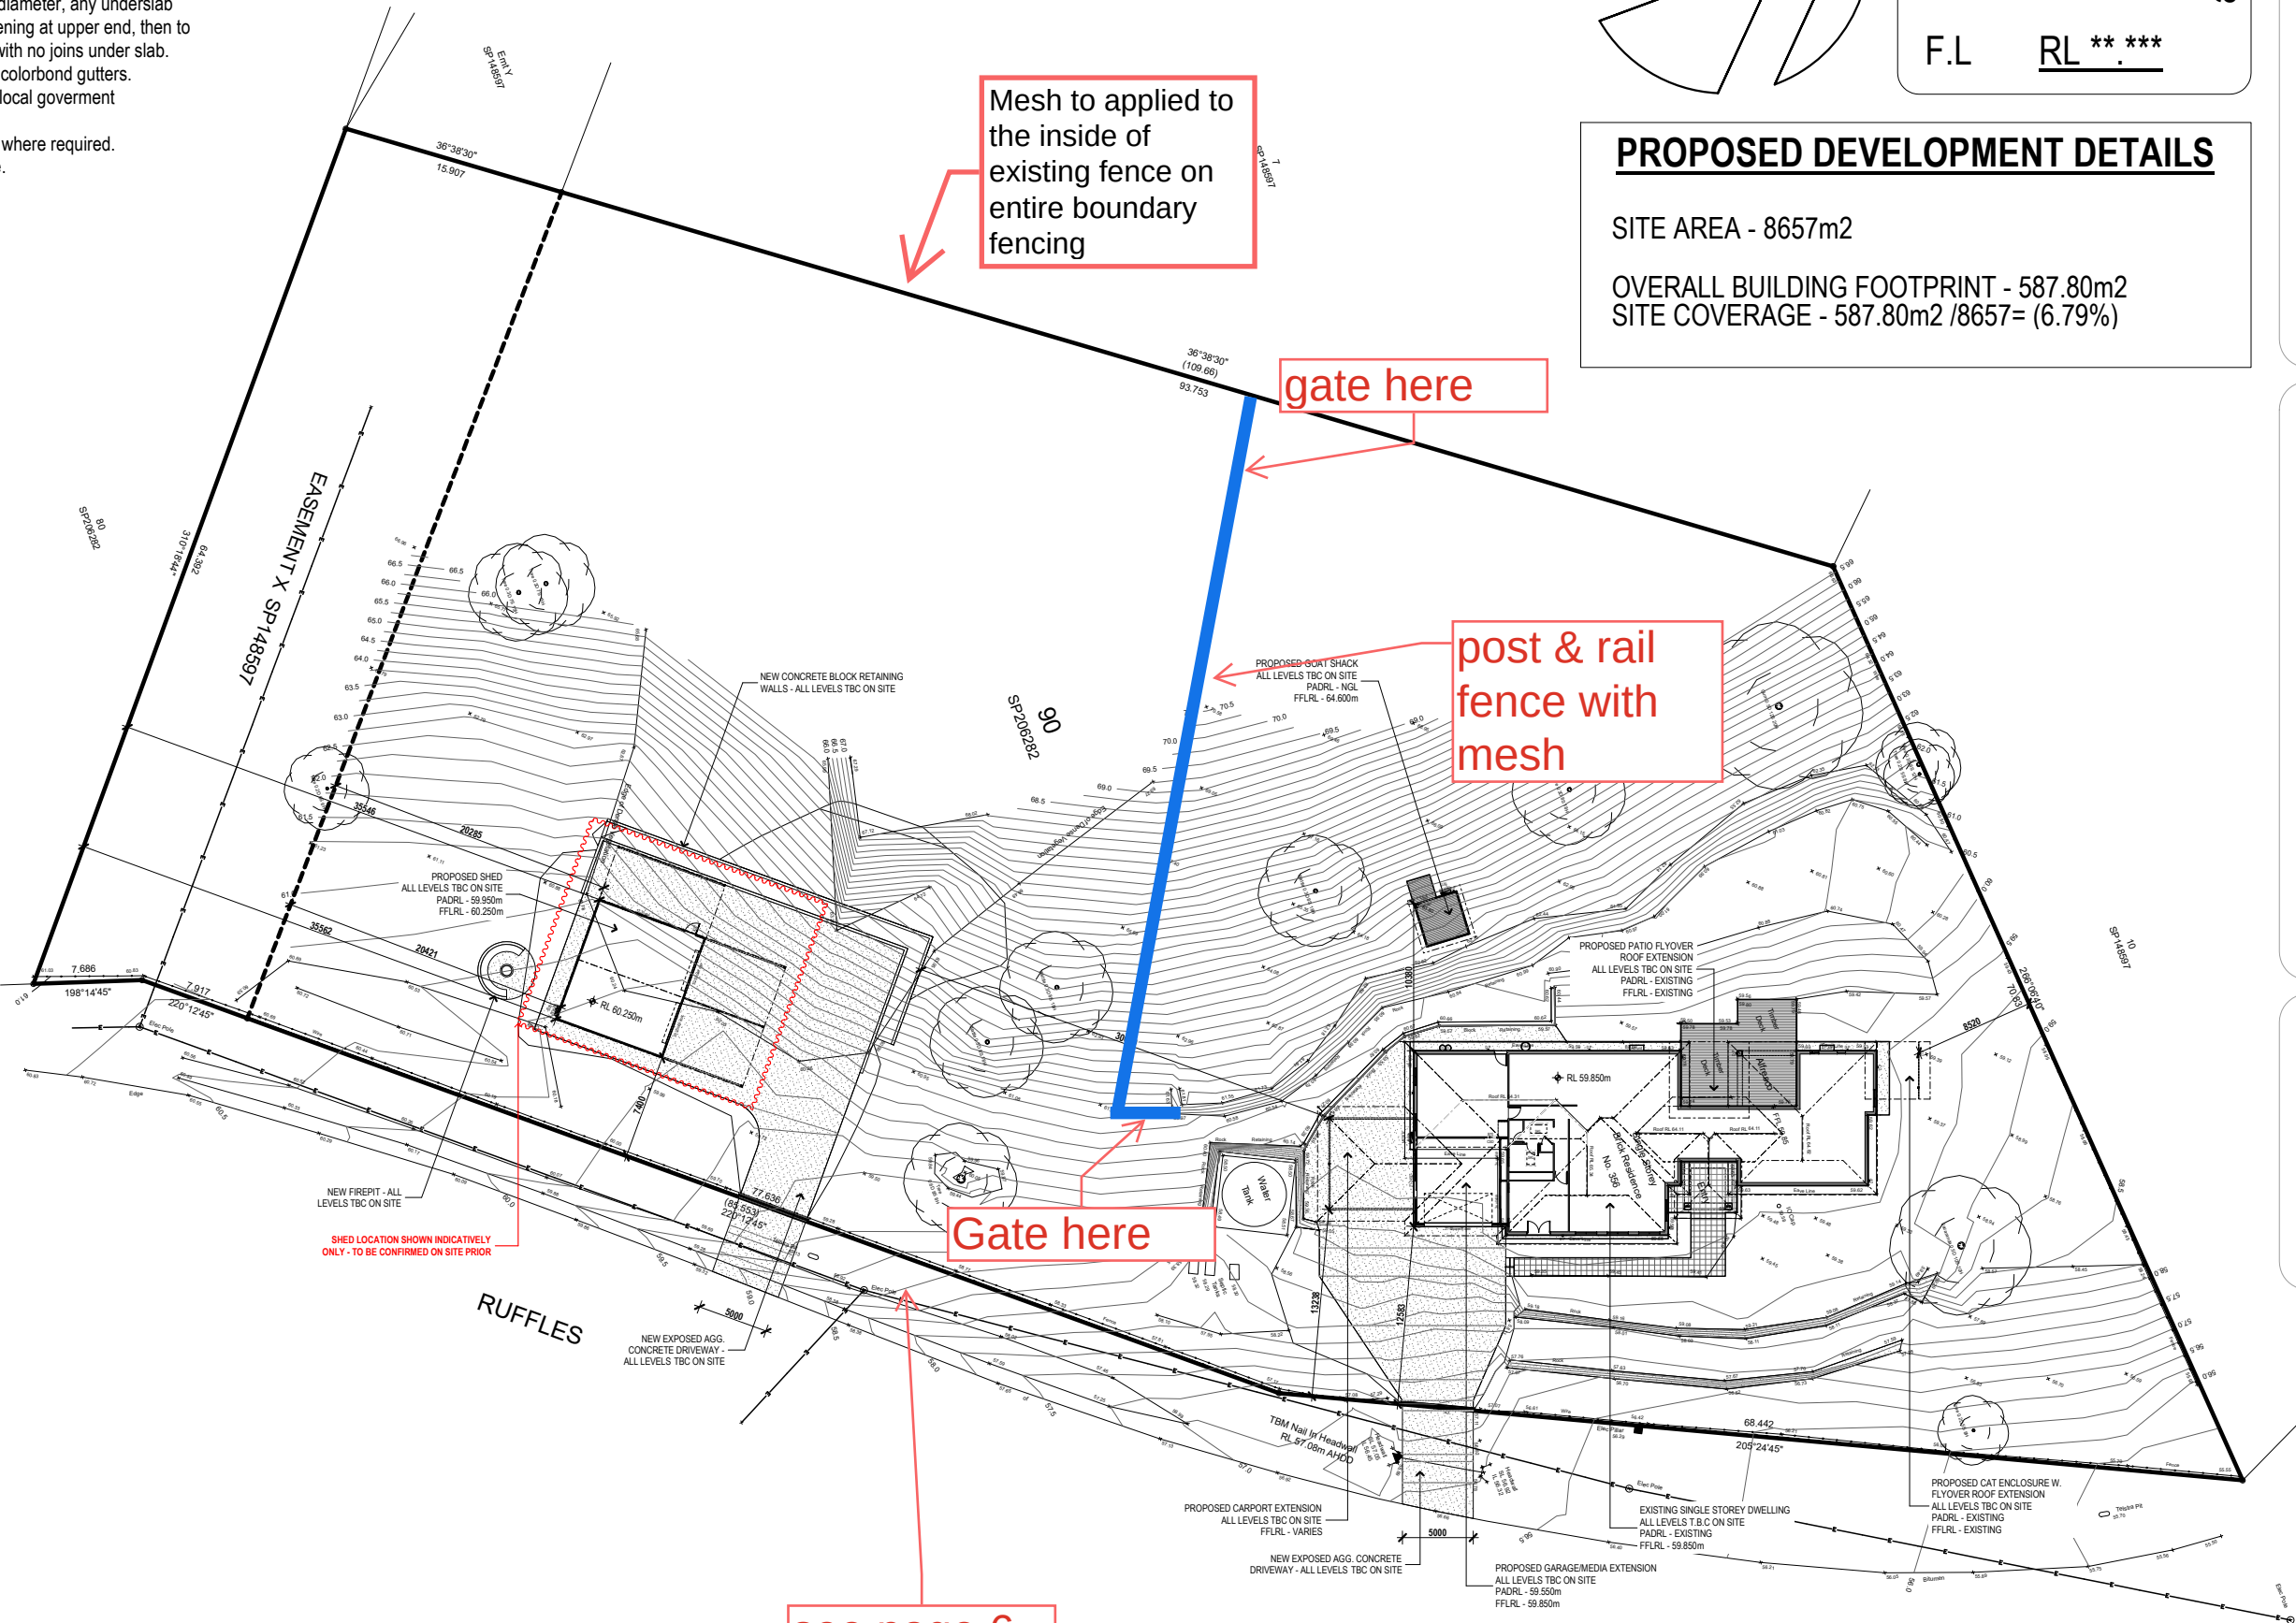

SITE PLAN - GROUND FLOOR OVERALL

SCALE 1:200 SHEET 5 OF 24 JOB NUMBER - 10588

see page 6
for front
boundary
details

PRELIMINARY PLANS ONLY NOT FOR CONSTRUCTION

NOTES:
*ALL dimensions to structure only - finishes excluded.
*ALL stormwater & drainage to be in compliance with N.C.C parts 3.3.5 & 7.4, as well as ASNZS3500.
*Discharge stormwater to TANK, where possible, ALL other stormwater & overflow to kerb & channel. In accordance with local government requirements & standards.
*2 Downpipes Max. to each 100mm stormwater pipe, subsurface pipes to be 100mm diameter, any underslab piping to have an inspection opening at upper end, then to be 100mm sewer grade piping with no joins under slab.
*Gutters to be 125mm D-section colorbond gutters.
*ALL driveway & VXO grades to local government requirements & standards.
*Provide sediment control to site where required.
*Meter box position T.B.C on site.
ALL retaining walls by owner.


PROPOSED DEVELOPMENT DETAILS

SITE AREA - 8657m2

OVERALL BUILDING FOOTPRINT - 587.80m2
SITE COVERAGE - 587.80m2 /8657= (6.79%)

PROPOSED PATIO FLYOVER
ROOF EXTENSION
ALL LEVELS TBC ON SITE
PADRL - EXISTING
FFLRL - EXISTING

G.L	RL ** ***	approx.
CUT	****mm	
FILL	****mm	
F.L	RL ** ***	

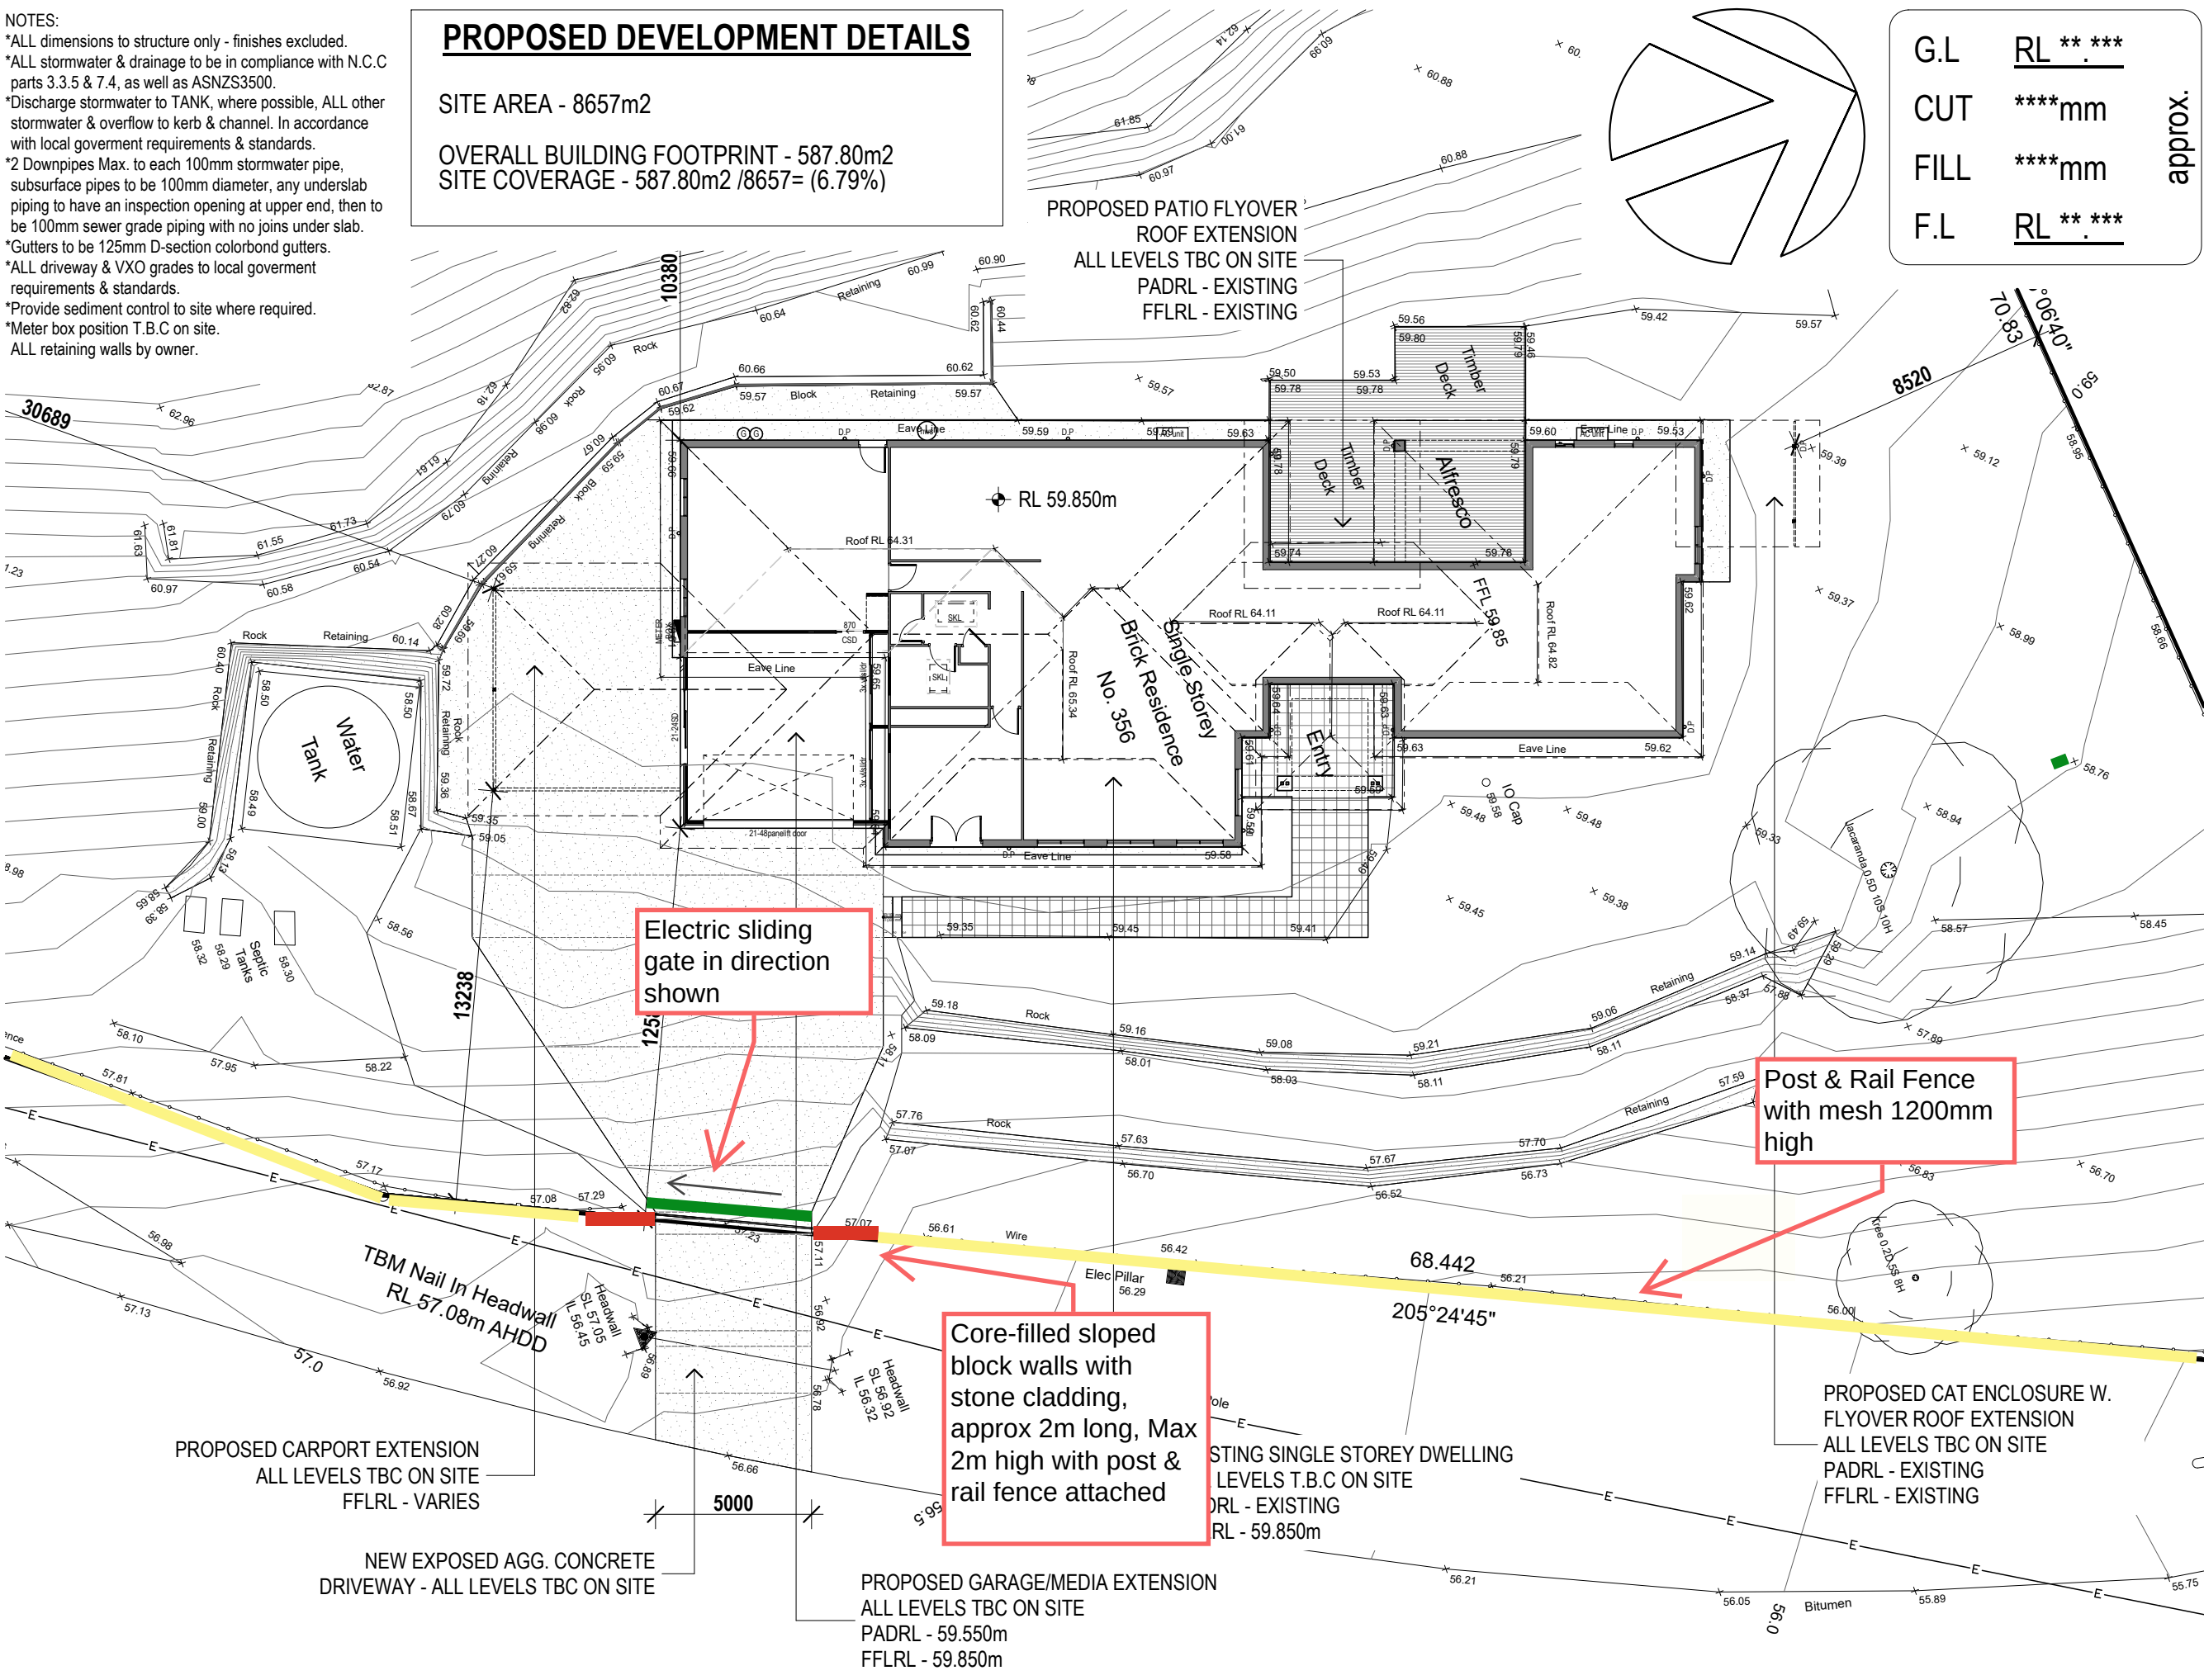

P 07 55 203 022
E design@stuartosman.com.au

Studio 2/71 Township Dr,
West Burleigh, QLD 4219

PO BOX 2845
Burleigh Heads DC QLD 4220

ABN 73 097 995 616
QBCC License No: 1129687



PROPOSED RENOVATION

BUILDER:SEEKA CONSTRUCTIONS

CLIENT: SEEKA CONSTRUCTIONS

PROJECT: LOT 90 No. 356
RUFFLES RD
WILLOWVALE

DRAWN BY: EP/RS

CHECKED BY: SO

DESIGN: CUSTOM

DATE: A01/05/2026

SCALES: 1:200 @ A3

AMENDMENTS:
B250526, C020726,

SHEET NUMBER: 6 of 24

JOB NUMBER: 10588

© Copyright reserved in part or whole.
THIS DESIGN IS THE EXCLUSIVE PROPERTY
OF STUART OSMAN
N.B ALL WRITTEN DIMENSIONS TAKE
PRECEDENCE OVER SCALED SIZES
Contractor to verify dimensions. Notify
designers of discrepancies. Failure to do so
shall void the designers responsibilities.
ALL dimensions to structure only - finishes
excluded. BE WARNED: SUBSTITUTION OF
ANY STRUCTURAL MEMBERS, AND OR ANY
VARIATION TO ANY PART OF THE DESIGN
WILL VOID ANY RESPONSIBILITIES OF STUART
OSMAN FOR THE STRUCTURAL INTEGRITY
AND PERFORMANCE OF THE BUILDING.


NOTES:
*ALL dimensions to structure only - finishes excluded.
*ALL stormwater & drainage to be in compliance with N.C.C parts 3.3.5 & 7.4, as well as ASNZS3500.
*Discharge stormwater to TANK, where possible, ALL other stormwater & overflow to kerb & channel. In accordance with local government requirements & standards.
*2 Downpipes Max. to each 100mm stormwater pipe, subsurface pipes to be 100mm diameter, any underslab piping to have an inspection opening at upper end, then to be 100mm sewer grade piping with no joins under slab.
*Gutters to be 125mm D-section colorbond gutters.
*ALL driveway & VXO grades to local government requirements & standards.
*Provide sediment control to site where required.
*Meter box position T.B.C on site.
ALL retaining walls by owner.

PROPOSED DEVELOPMENT DETAILS


SITE AREA - 8657m2

OVERALL BUILDING FOOTPRINT - 587.80m2
SITE COVERAGE - 587.80m2 /8657= (6.79%)

NEW CONCRETE BLOCK RETAINING WALLS - ALL LEVELS TBC ON SITE

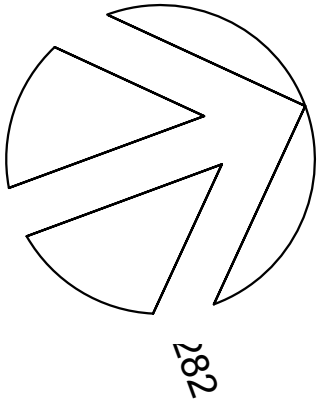


G.L	RL ** ***	approx.
CUT	****mm	
FILL	****mm	
F.L	RL ** ***	

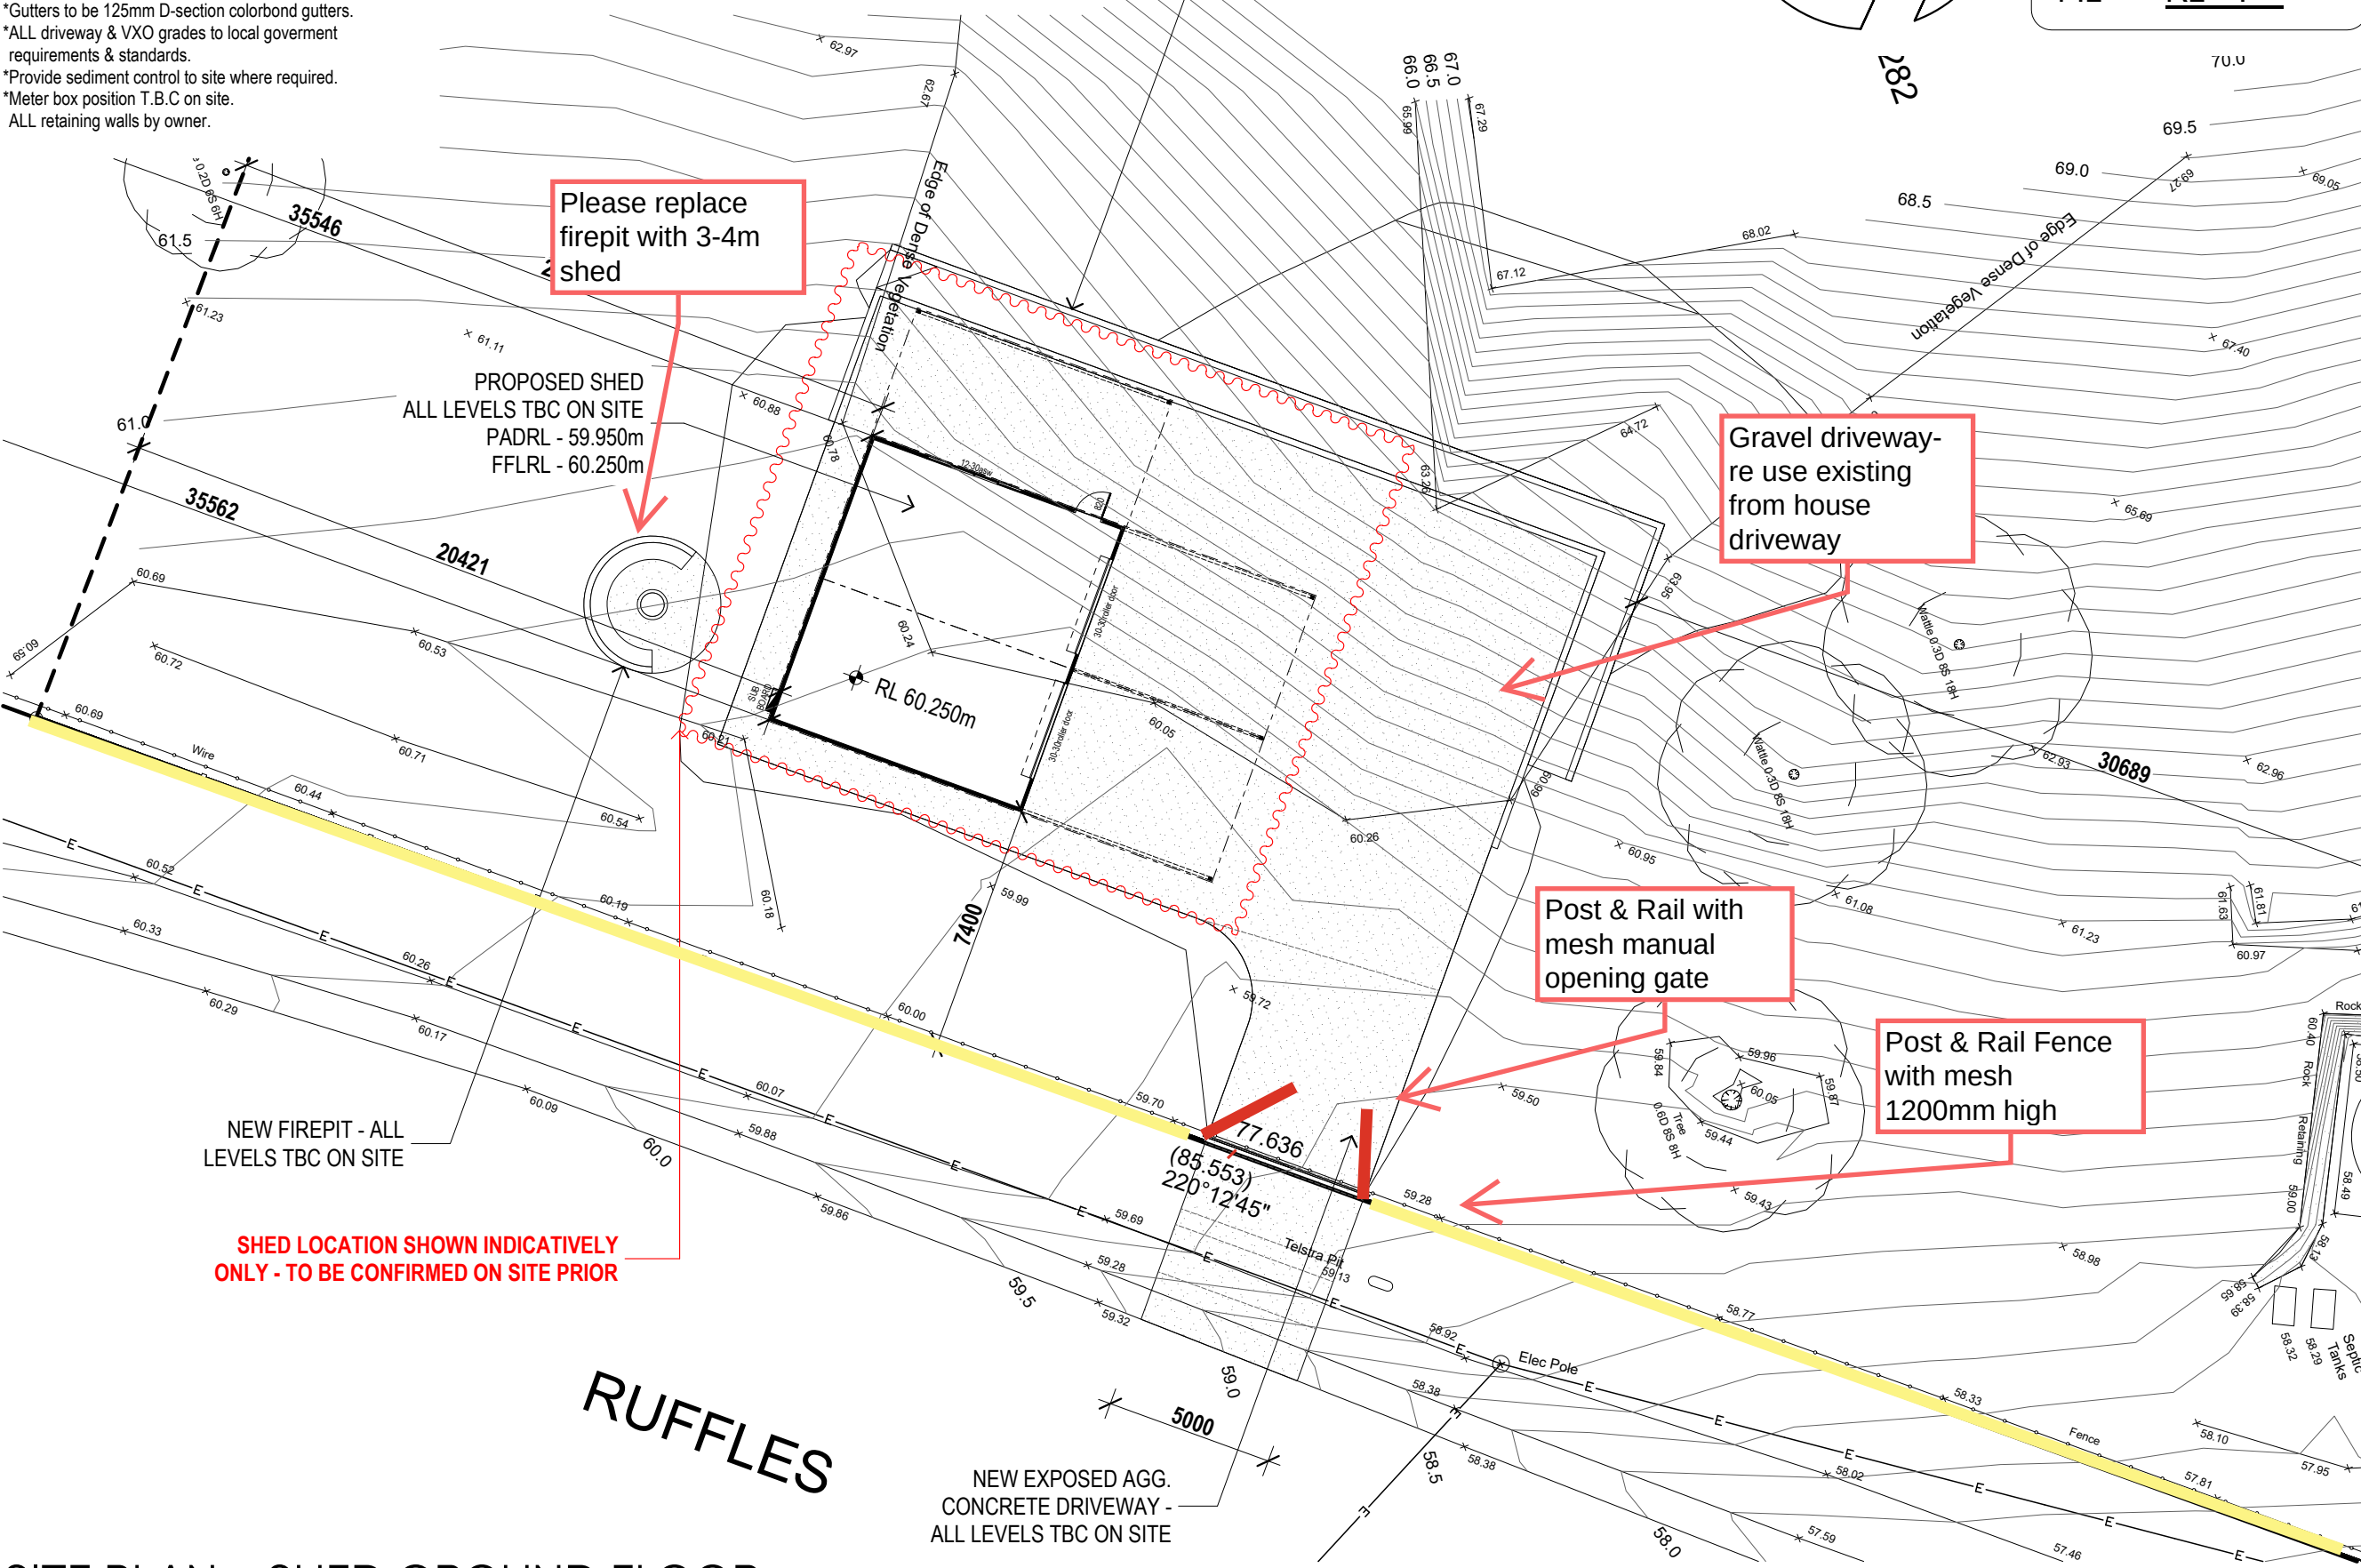

SITE PLAN – SHED GROUND FLOOR
SCALE 1:200 SHEET 7 OF 24 JOB NUMBER – 10588

PRELIMINARY PLANS ONLY NOT FOR CONSTRUCTION

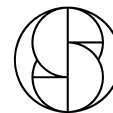

**Stuart
Osman**

P 07 55 203 022
E design@stuartosman.com.au

Studio 2/71 Township Dr,
West Burleigh, QLD 4219

PO BOX 2845
Burleigh Heads DC QLD 4220

ABN 73 097 995 616
QBCC License No: 1129687



BD Building Design
Queensland



**MASTER
BUILDERS**
QUEENSLAND

PROPOSED RENOVATION	
BUILDER:SEEKA CONSTRUCTIONS	
CLIENT: SEEKA CONSTRUCTIONS	
PROJECT:	LOT 90 No. 356 RUFFLES RD WILLOWVALE
DRAWN BY:	EP/RS
CHECKED BY:	SO
DESIGN:	CUSTOM
DATE:	A01/05/2026
SCALES:	1:200 @ A3
AMENDMENTS:	B250526, C020726,
SHEET NUMBER:	7 of 24
JOB NUMBER:	10588

© Copyright reserved in part or whole.
THIS DESIGN IS THE EXCLUSIVE PROPERTY
OF STUART OSMAN
N.B ALL WRITTEN DIMENSIONS TAKE
PRECEDENCE OVER SCALED SIZES
Contractor to verify dimensions. Notify
designers of discrepancies. Failure to do so
shall void the designers responsibilities.
ALL dimensions to structure only - finishes
excluded. BE WARNED: SUBSTITUTION OF
ANY STRUCTURAL MEMBERS, AND OR ANY
VARIATION TO ANY PART OF THE DESIGN
WILL VOID ANY RESPONSIBILITIES OF STUART
OSMAN FOR THE STRUCTURAL INTEGRITY
AND PERFORMANCE OF THE BUILDING.

NOTES:
*ALL dimensions to structure only - finishes excluded.
*ALL stormwater & drainage to be in compliance with N.C.C parts 3.3.5 & 7.4, as well as ASNZS3500.
*Discharge stormwater to TANK, where possible, ALL other stormwater & overflow to kerb & channel. In accordance with local government requirements & standards.
*2 Downpipes Max. to each 100mm stormwater pipe, subsurface pipes to be 100mm diameter, any underslab piping to have an inspection opening at upper end, then to be 100mm sewer grade piping with no joins under slab.
*Gutters to be 125mm D-section colorbond gutters.
*ALL driveway & VXO grades to local government requirements & standards.
*Provide sediment control to site where required.
*Meter box position T.B.C on site.
ALL retaining walls by owner.



PROPOSED DEVELOPMENT DETAILS

SITE AREA - 8657m2

OVERALL BUILDING FOOTPRINT - 587.80m2
SITE COVERAGE - 587.80m2 /8657= (6.79%)

PROPOSED GOAT SHACK
ALL LEVELS TBC ON SITE
PADRL - NGL
FFLRL - 64.600m

PROPOSED PATIO FLYOVER
ROOF EXTENSION
ALL LEVELS TBC ON SITE
PADRL - EXISTING
FFLRL - EXISTING

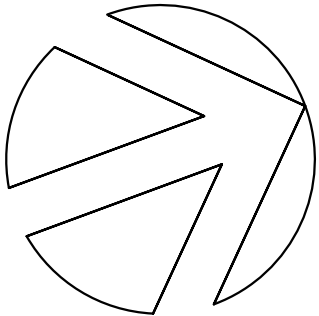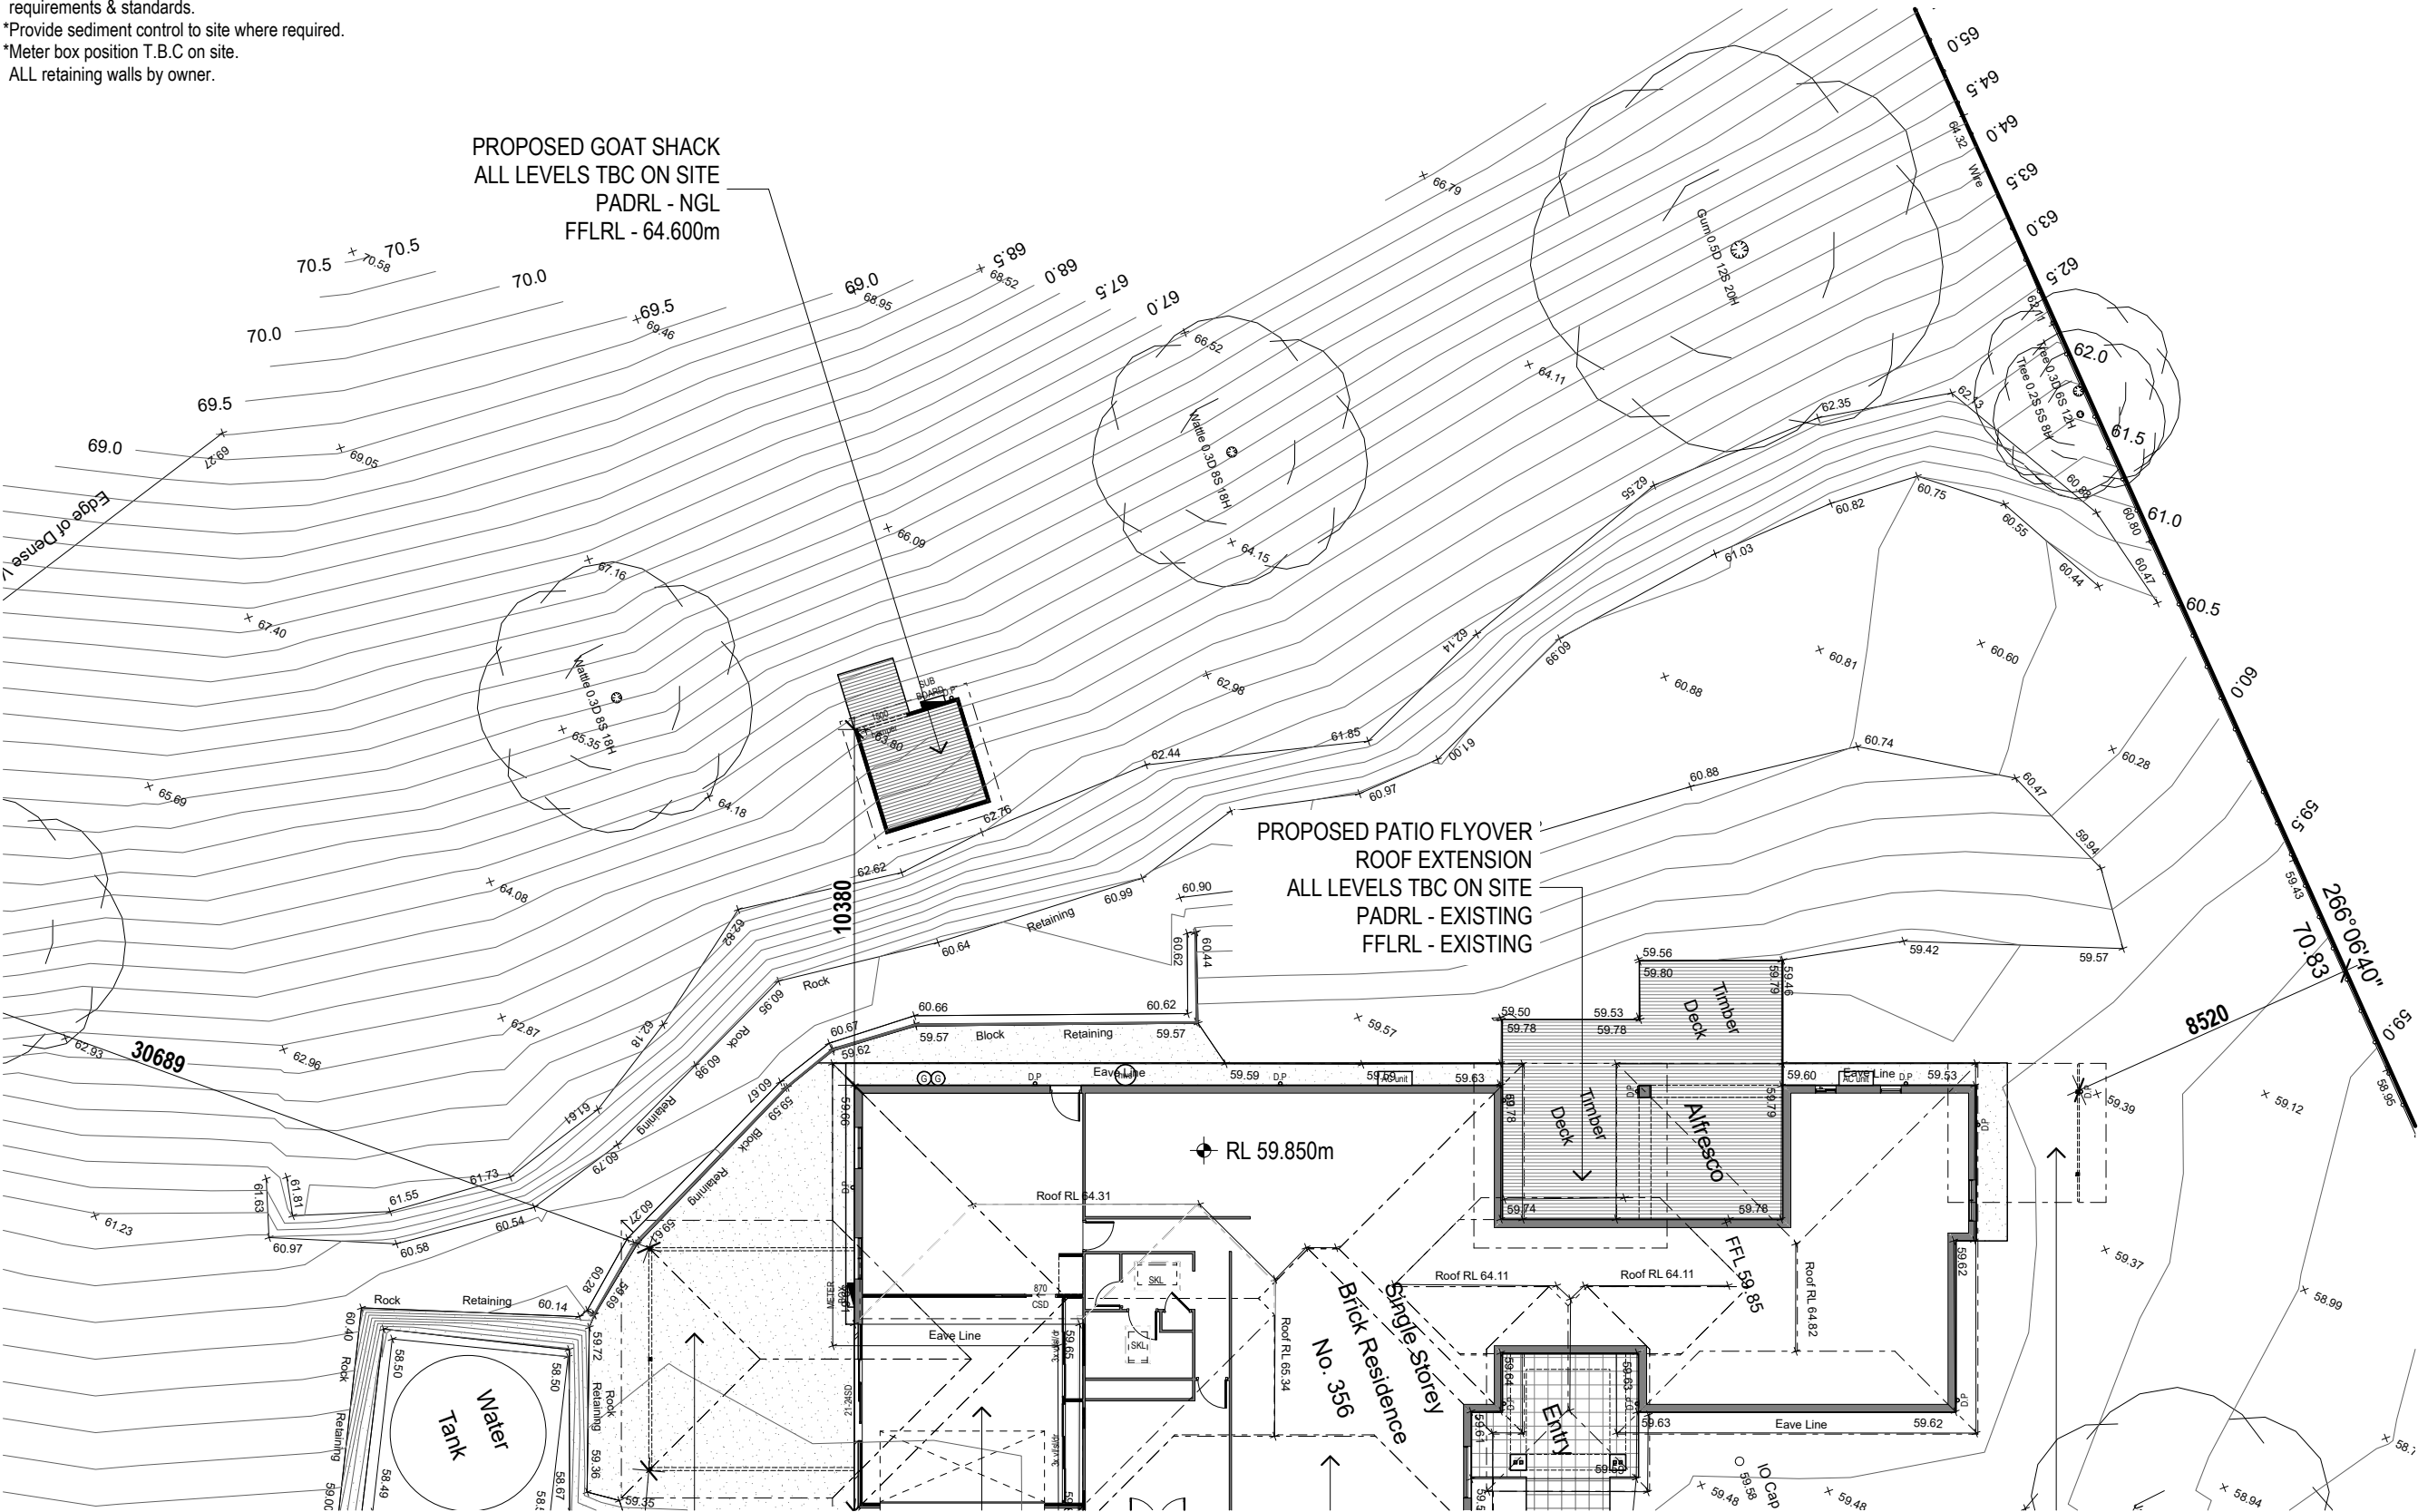

G.L	RL ** ***	approx.
CUT	****mm	
FILL	****mm	
F.L	RL ** ***	



P 07 55 203 022
E design@stuartosman.com.au

Studio 2/71 Township Dr,
West Burleigh, QLD 4219

PO BOX 2845
Burleigh Heads DC QLD 4220

ABN 73 097 995 616
QBCC License No: 1129687



PROPOSED RENOVATION

BUILDER:SEEKA CONSTRUCTIONS

CLIENT: SEEKA CONSTRUCTIONS

PROJECT: LOT 90 No. 356
RUFFLES RD
WILLOWVALE

DRAWN BY: EP/RS
CHECKED BY: SO
DESIGN: CUSTOM
DATE: A01/05/2026
SCALES: 1:200 @ A3
AMENDMENTS:
B250526, C020726,

SHEET NUMBER: 8 of 24
JOB NUMBER: 10588

© Copyright reserved in part or whole.
THIS DESIGN IS THE EXCLUSIVE PROPERTY
OF STUART OSMAN
N.B ALL WRITTEN DIMENSIONS TAKE
PRECEDENCE OVER SCALED SIZES
Contractor to verify dimensions. Notify
designers of discrepancies. Failure to do so
shall void the designers responsibilities.
ALL dimensions to structure only - finishes
excluded. BE WARNED: SUBSTITUTION OF
ANY STRUCTURAL MEMBERS, AND OR ANY
VARIATION TO ANY PART OF THE DESIGN
WILL VOID ANY RESPONSIBILITIES OF STUART
OSMAN FOR THE STRUCTURAL INTEGRITY
AND PERFORMANCE OF THE BUILDING.

SITE PLAN - GOAT SHACK


SCALE 1:200 SHEET 8 OF 24 JOB NUMBER - 10588

PRELIMINARY PLANS ONLY NOT FOR CONSTRUCTION

ALL ELEMENTS MARKED IN RED TO BE DEMOLISHED.


EXISTING FLOOR AREA

	Area (m2)
GROUND FLOOR LIVING	247.55
GARAGE	46.49
PATIO	16.46
PORCH	11.42
TOTAL	321.92 m²

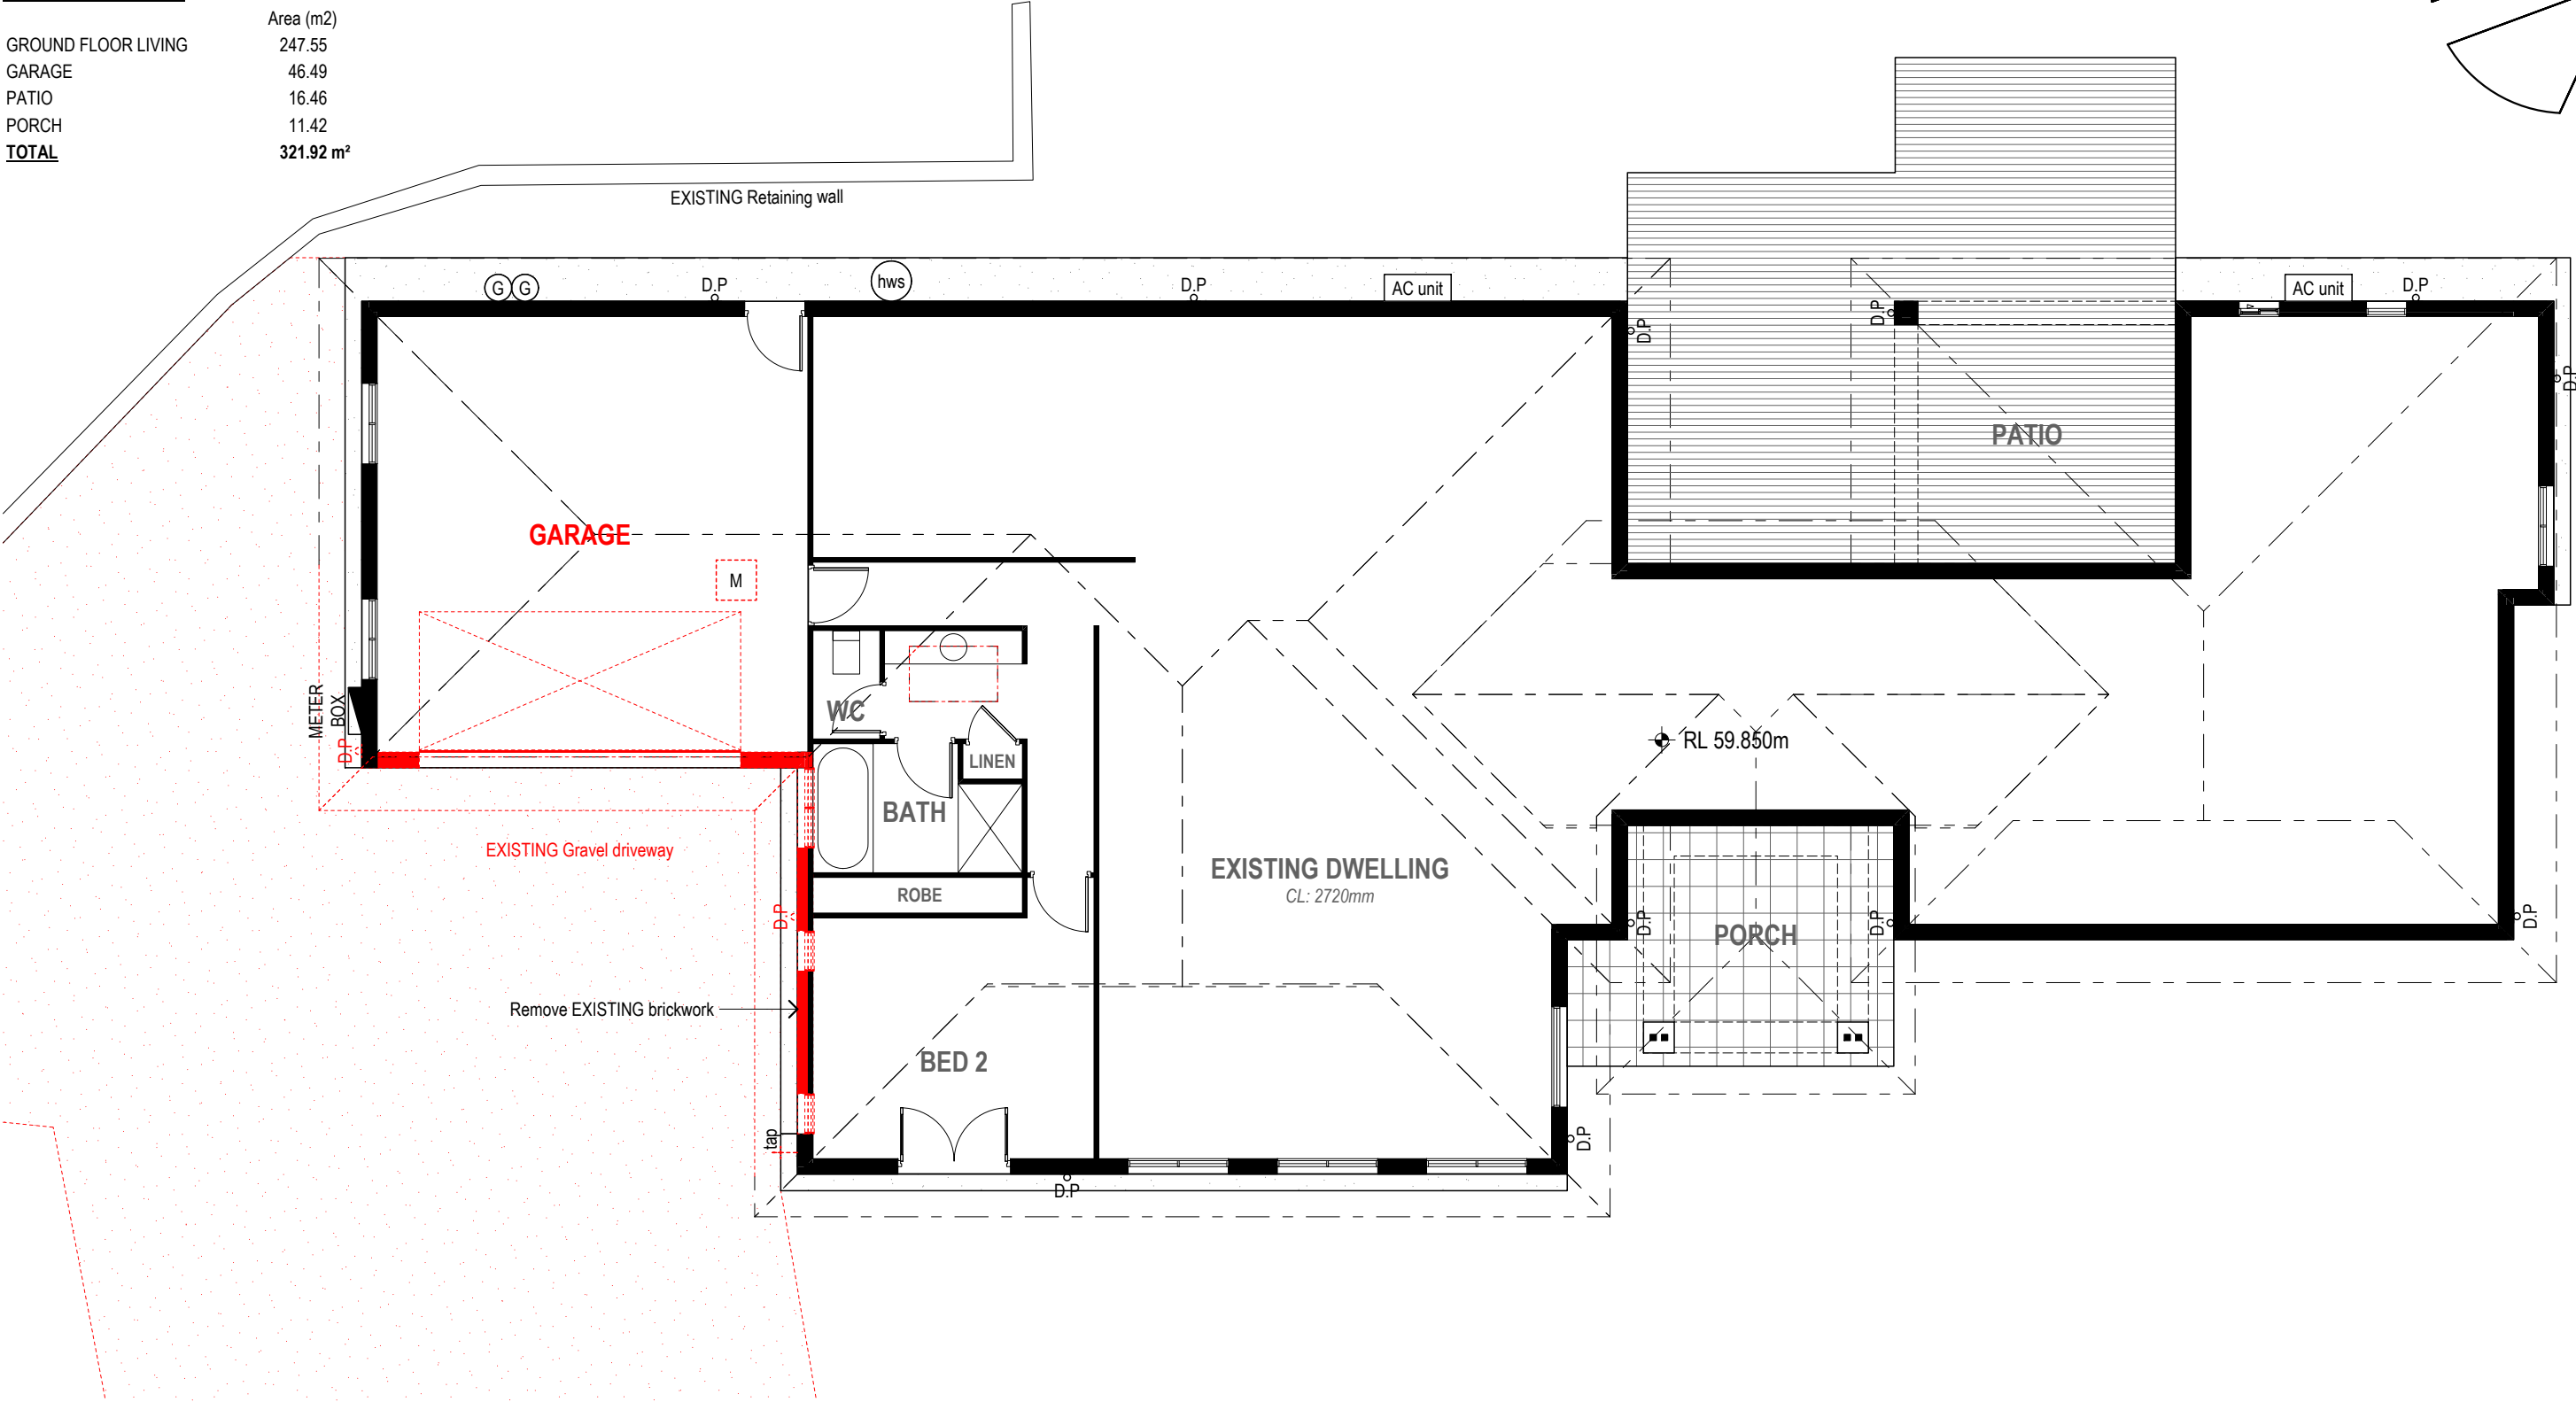

PRELIMINARY PLANS ONLY NOT FOR CONSTRUCTION

DEMOLITION GROUND FLOOR PLAN
SCALE 1:100

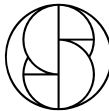

Stuart
Osman

P 07 55 203 022
E design@stuartosman.com.au
Studio 2/71 Township Dr,
West Burleigh, QLD 4219
PO BOX 2845
Burleigh Heads DC QLD 4220

BD Building Design
Queensland

MASTER
BUILDERS
QUEENSLAND

bdqa
BUILDING DESIGNERS
ASSOCIATION OF AUSTRALIA

ABN 73 097 995 616
QBCC License No: 1129687


PROPOSED RENOVATION

BUILDER: SEEKA
CONSTRUCTIONS
CLIENT: SEEKA
CONSTRUCTIONS
PROJECT: LOT 90 No. 356
RUFFLES RD
WILLOWVALE

DESIGN: CUSTOM
DATE: A01/05/2026
SCALES: 1:100 @ A3
AMENDMENTS:
B250526, C020726,
DRAWN BY: EP/RS
CHECKED BY: SO
SHEET NUMBER: 9 of 24
JOB NUMBER: 10588

© Copyright reserved in part or whole.
THIS DESIGN IS THE EXCLUSIVE PROPERTY
OF STUART OSMAN
N.B ALL WRITTEN DIMENSIONS TAKE
PRECEDENCE OVER SCALED SIZES
Contractor to verify dimensions. Notify
designers of discrepancies. Failure to do so
shall void the designers responsibilities.
ALL dimensions to structure only - finishes
excluded. BE WARNED: SUBSTITUTION OF
ANY STRUCTURAL MEMBERS, AND OR ANY
VARIATION TO ANY PART OF THE DESIGN
WILL VOID ANY RESPONSIBILITIES OF
STUART OSMAN FOR THE STRUCTURAL
INTEGRITY AND PERFORMANCE OF THE
BUILDING.

ALL ELEMENTS MARKED IN RED TO BE DEMOLISHED.

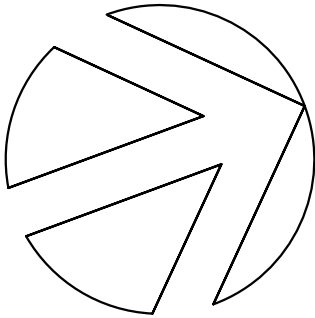

**Stuart
Osman**

P 07 55 203 022
E design@stuartosman.com.au

Studio 2/71 Township Dr,
West Burleigh, QLD 4219

PO BOX 2845
Burleigh Heads DC QLD 4220

ABN 73 097 995 616
QBCC License No: 1129687



PROPOSED RENOVATION

BUILDER:SEEKA CONSTRUCTIONS

CLIENT: SEEKA CONSTRUCTIONS

PROJECT: LOT 90 No. 356
RUFFLES RD
WILLOWVALE

DRAWN BY: EP/RS

CHECKED BY: SO

DESIGN: CUSTOM

DATE: A01/05/2026


SCALES: 1:100 @ A3

AMENDMENTS:
B250526, C020726,

SHEET NUMBER: 10 of 24

JOB NUMBER: **10588**


© Copyright reserved in part or whole.
THIS DESIGN IS THE EXCLUSIVE PROPERTY
OF STUART OSMAN
N.B ALL WRITTEN DIMENSIONS TAKE
PRECEDENCE OVER SCALED SIZES
Contractor to verify dimensions. Notify
designers of discrepancies. Failure to do so
shall void the designers responsibilities.
ALL dimensions to structure only - finishes
excluded. BE WARNED: SUBSTITUTION OF
ANY STRUCTURAL MEMBERS, AND OR ANY
VARIATION TO ANY PART OF THE DESIGN
WILL VOID ANY RESPONSIBILITIES OF STUART
OSMAN FOR THE STRUCTURAL INTEGRITY
AND PERFORMANCE OF THE BUILDING.

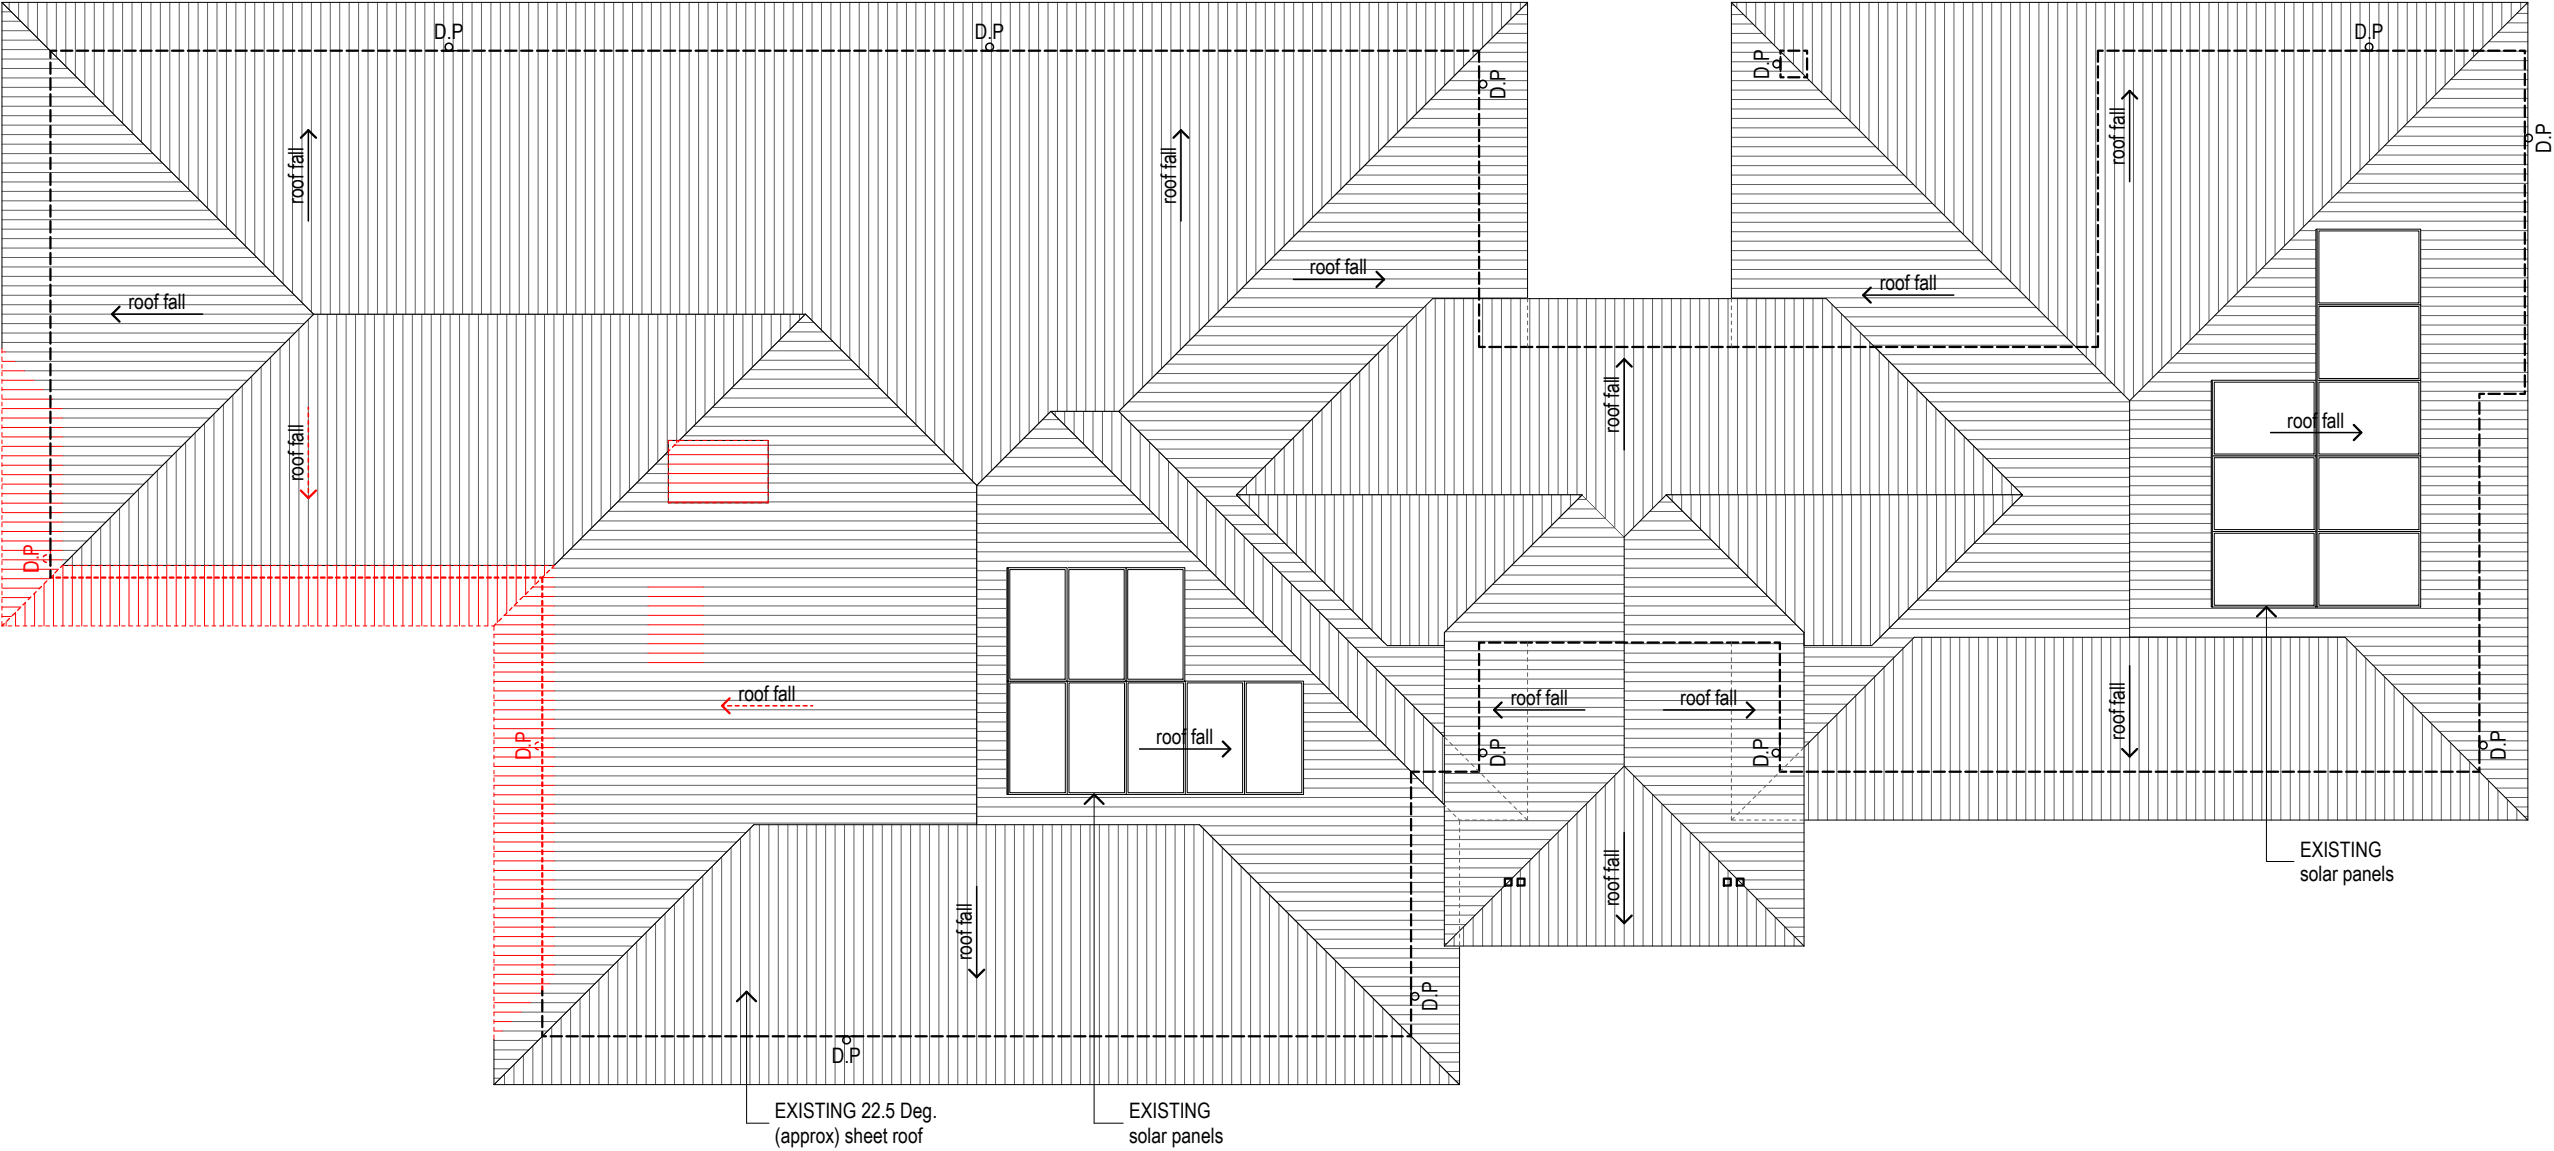

DEMOLITION ROOF PLAN
SCALE 1:100

PRELIMINARY PLANS ONLY NOT FOR CONSTRUCTION

ALL DIMENSIONS ARE APPROX T.B.C BY BUILDER ONSITE

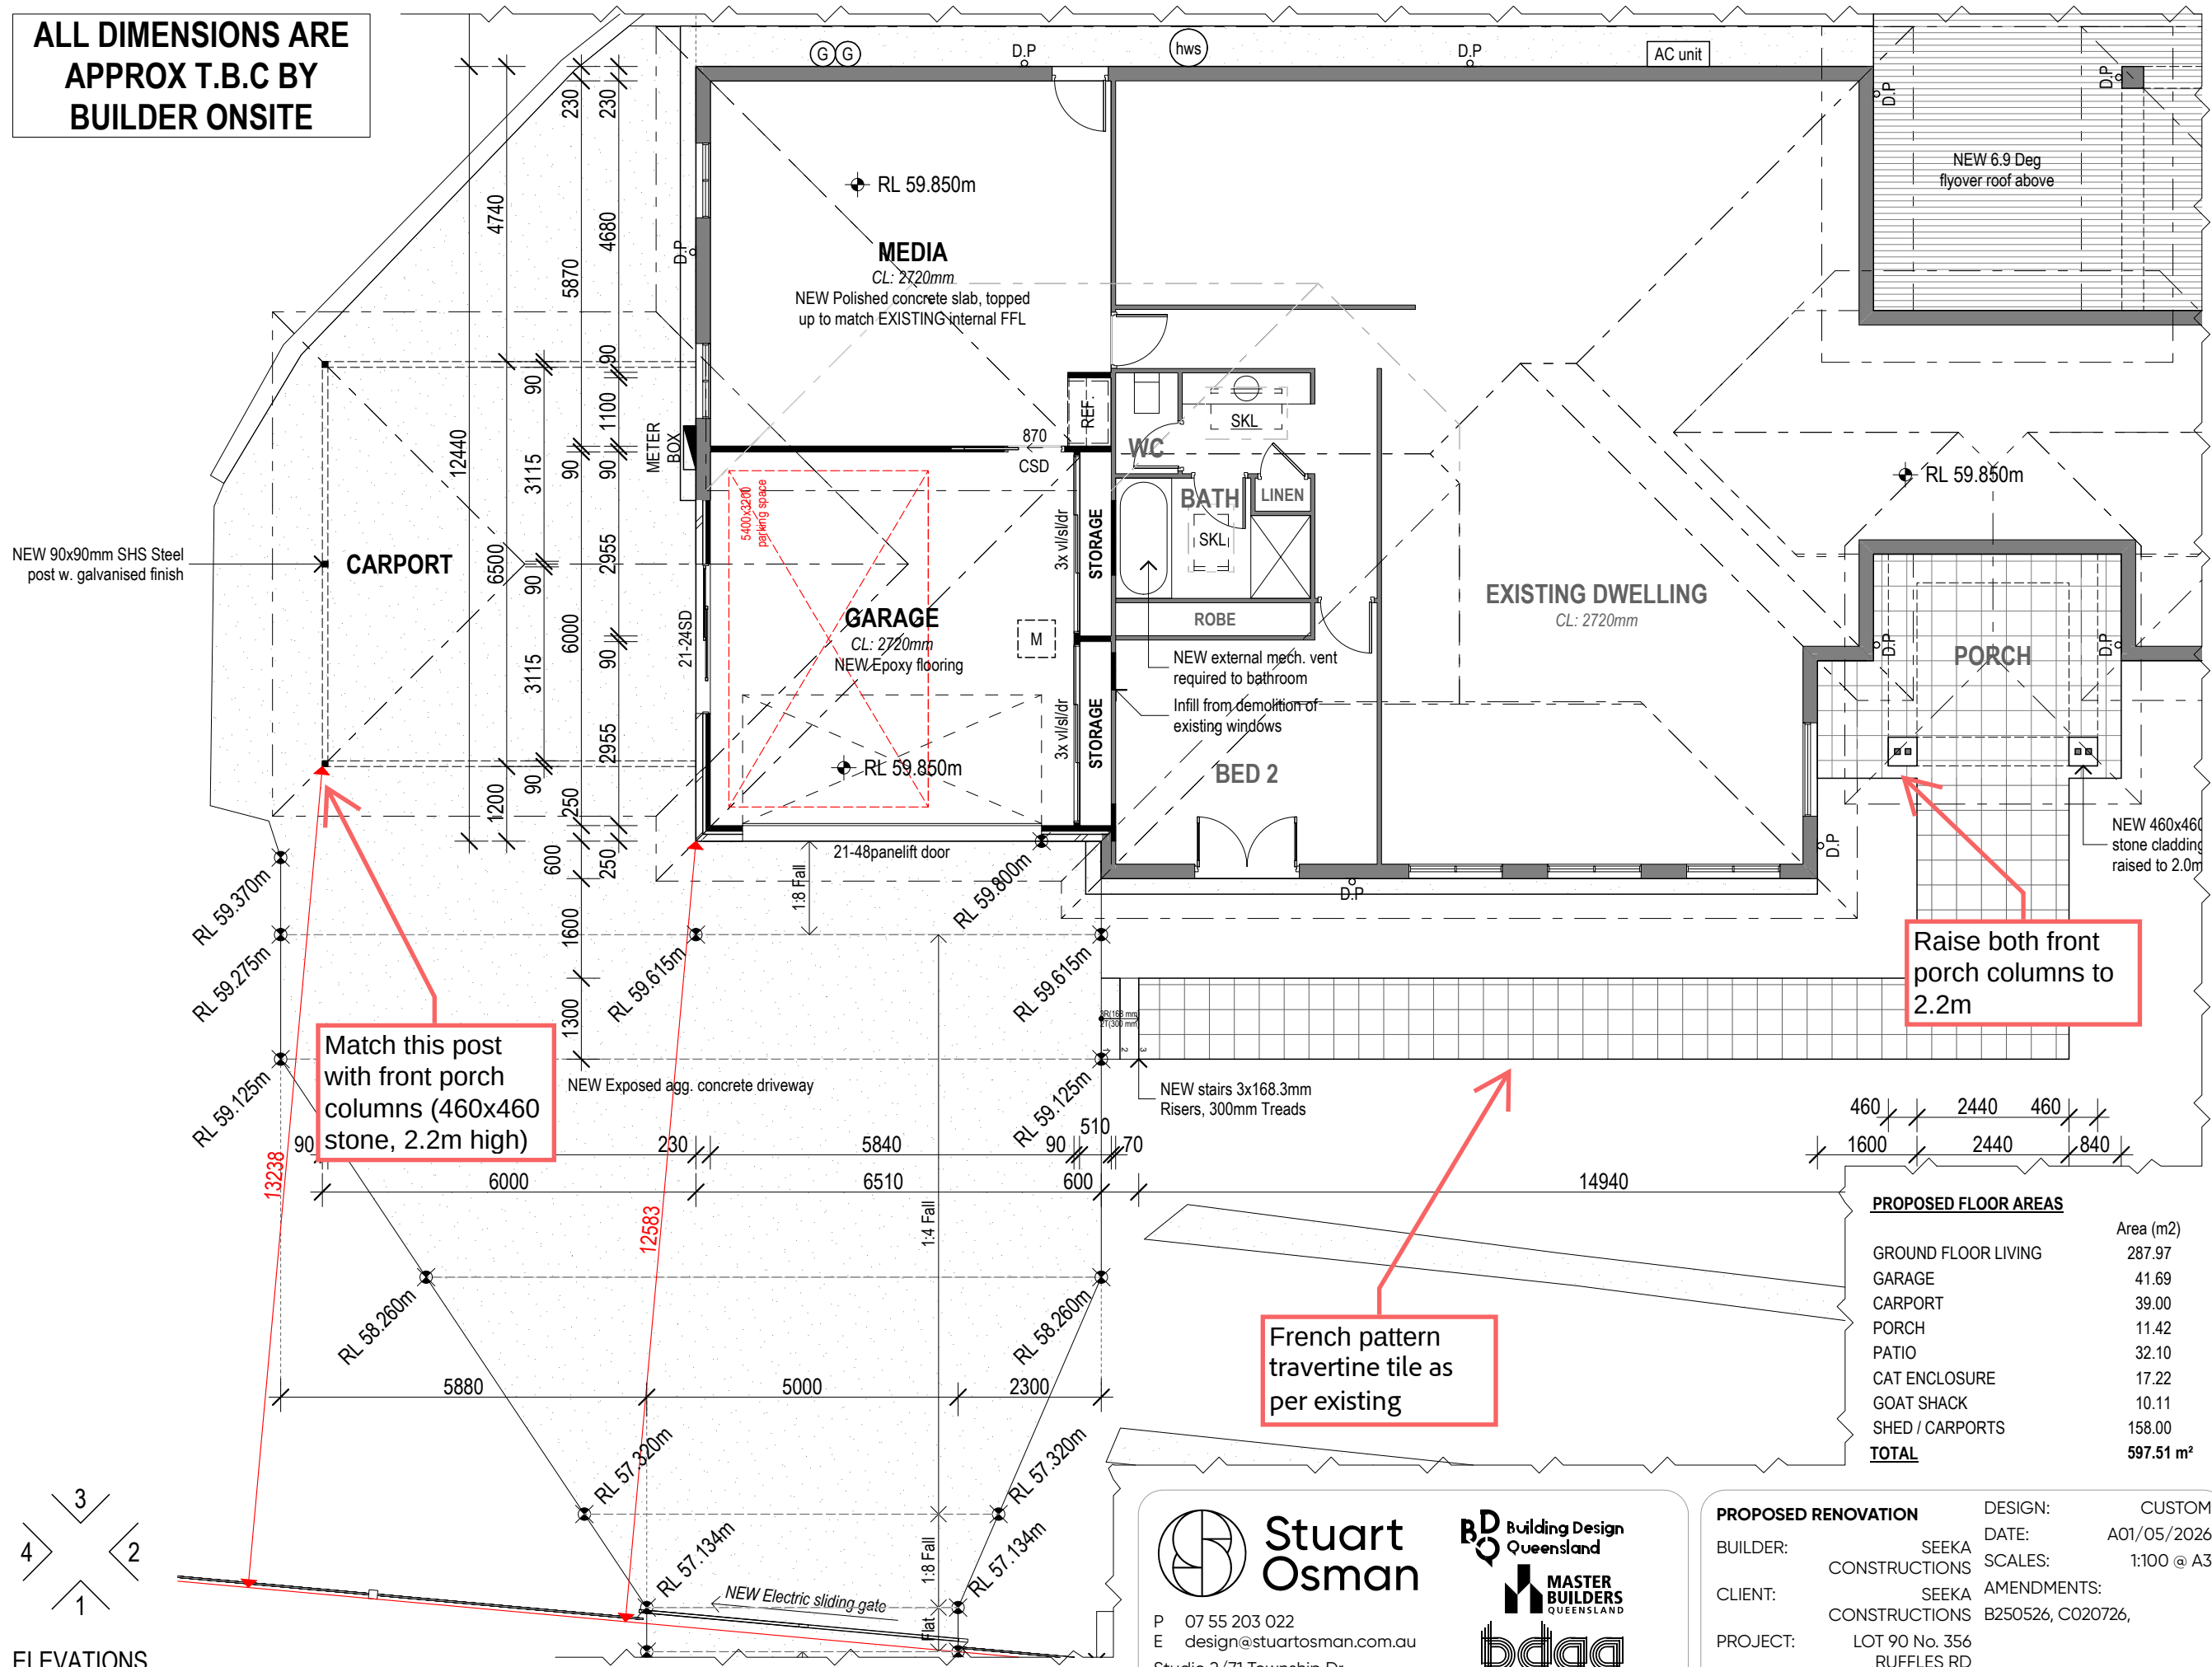

ELEVATIONS
PROPOSED GROUND FLOOR PLAN
SCALE 1:100

Stuart Osman
P 07 55 203 022
E design@stuartosman.com.au
Studio 2/71 Township Dr,
West Burleigh, QLD 4219
PO BOX 2845
Burleigh Heads DC QLD 4220

Building Design Queensland
MASTER BUILDERS QUEENSLAND
bdqa
BUILDING DESIGNERS ASSOCIATION OF AUSTRALIA
ABN 73 097 995 616
QBCC License No: 1129687

PROPOSED RENOVATION

BUILDER: SEEKA CONSTRUCTIONS
CLIENT: SEEKA CONSTRUCTIONS
PROJECT: LOT 90 No. 356 RUFFLES RD WILLOWVALE


DRAWN BY: EP/RS
CHECKED BY: SO

DESIGN: CUSTOM
DATE: A01/05/2026
SCALES: 1:100 @ A3
AMENDMENTS: B250526, C020726,


SHEET NUMBER: 11 of 24
JOB NUMBER: 10588

PROPOSED FLOOR AREAS	
	Area (m2)
GROUND FLOOR LIVING	287.97
GARAGE	41.69
CARPORT	39.00
PORCH	11.42
PATIO	32.10
CAT ENCLOSURE	17.22
GOAT SHACK	10.11
SHED / CARPORTS	158.00
TOTAL	597.51 m²


- NOTES:
- *All dimensions to structure only - finishes excluded.
 - *Lift off hinges to WC door, as per N.C.C 10.4.2.
 - *Provide GPO & cold water provisions to DW space.
 - *ALL external & internal doors & windows to be measured onsite & confirmed by builder.
 - *Sarking to external walls.
 - *Insulation Req. as per Energy Efficiency Report.
 - *Mechanically vent rooms without natural ventilation.
 - *Maximum water supply pressure not to exceed 500kpa at any outlet.
 - *All shower roses to be AAA rated.
 - *Hot water system shall be heat pump, solar, or gas.
 - *Water supply outlets to have WELs rating.
 - *Toilet cisterns to have dual flush, 6/3 Litre.
 - *ALL handrails to be 1000mm above finished floor level.
 - *Bedroom windows w. 2m fall height from FL to ground below must comply with N.C.C 11.3.7. To be fitted with non-removable screens or restricted to 125mm opening.
 - *If more than one smoke alarm is required they must be interconnected as per N.C.C 9.5.1, & comply with AS 3786.

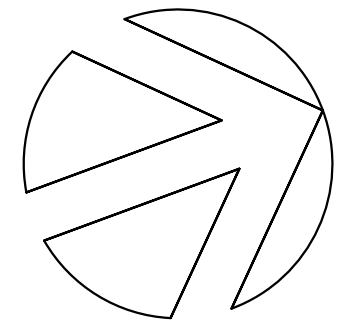

PRELIMINARY PLANS ONLY NOT FOR CONSTRUCTION

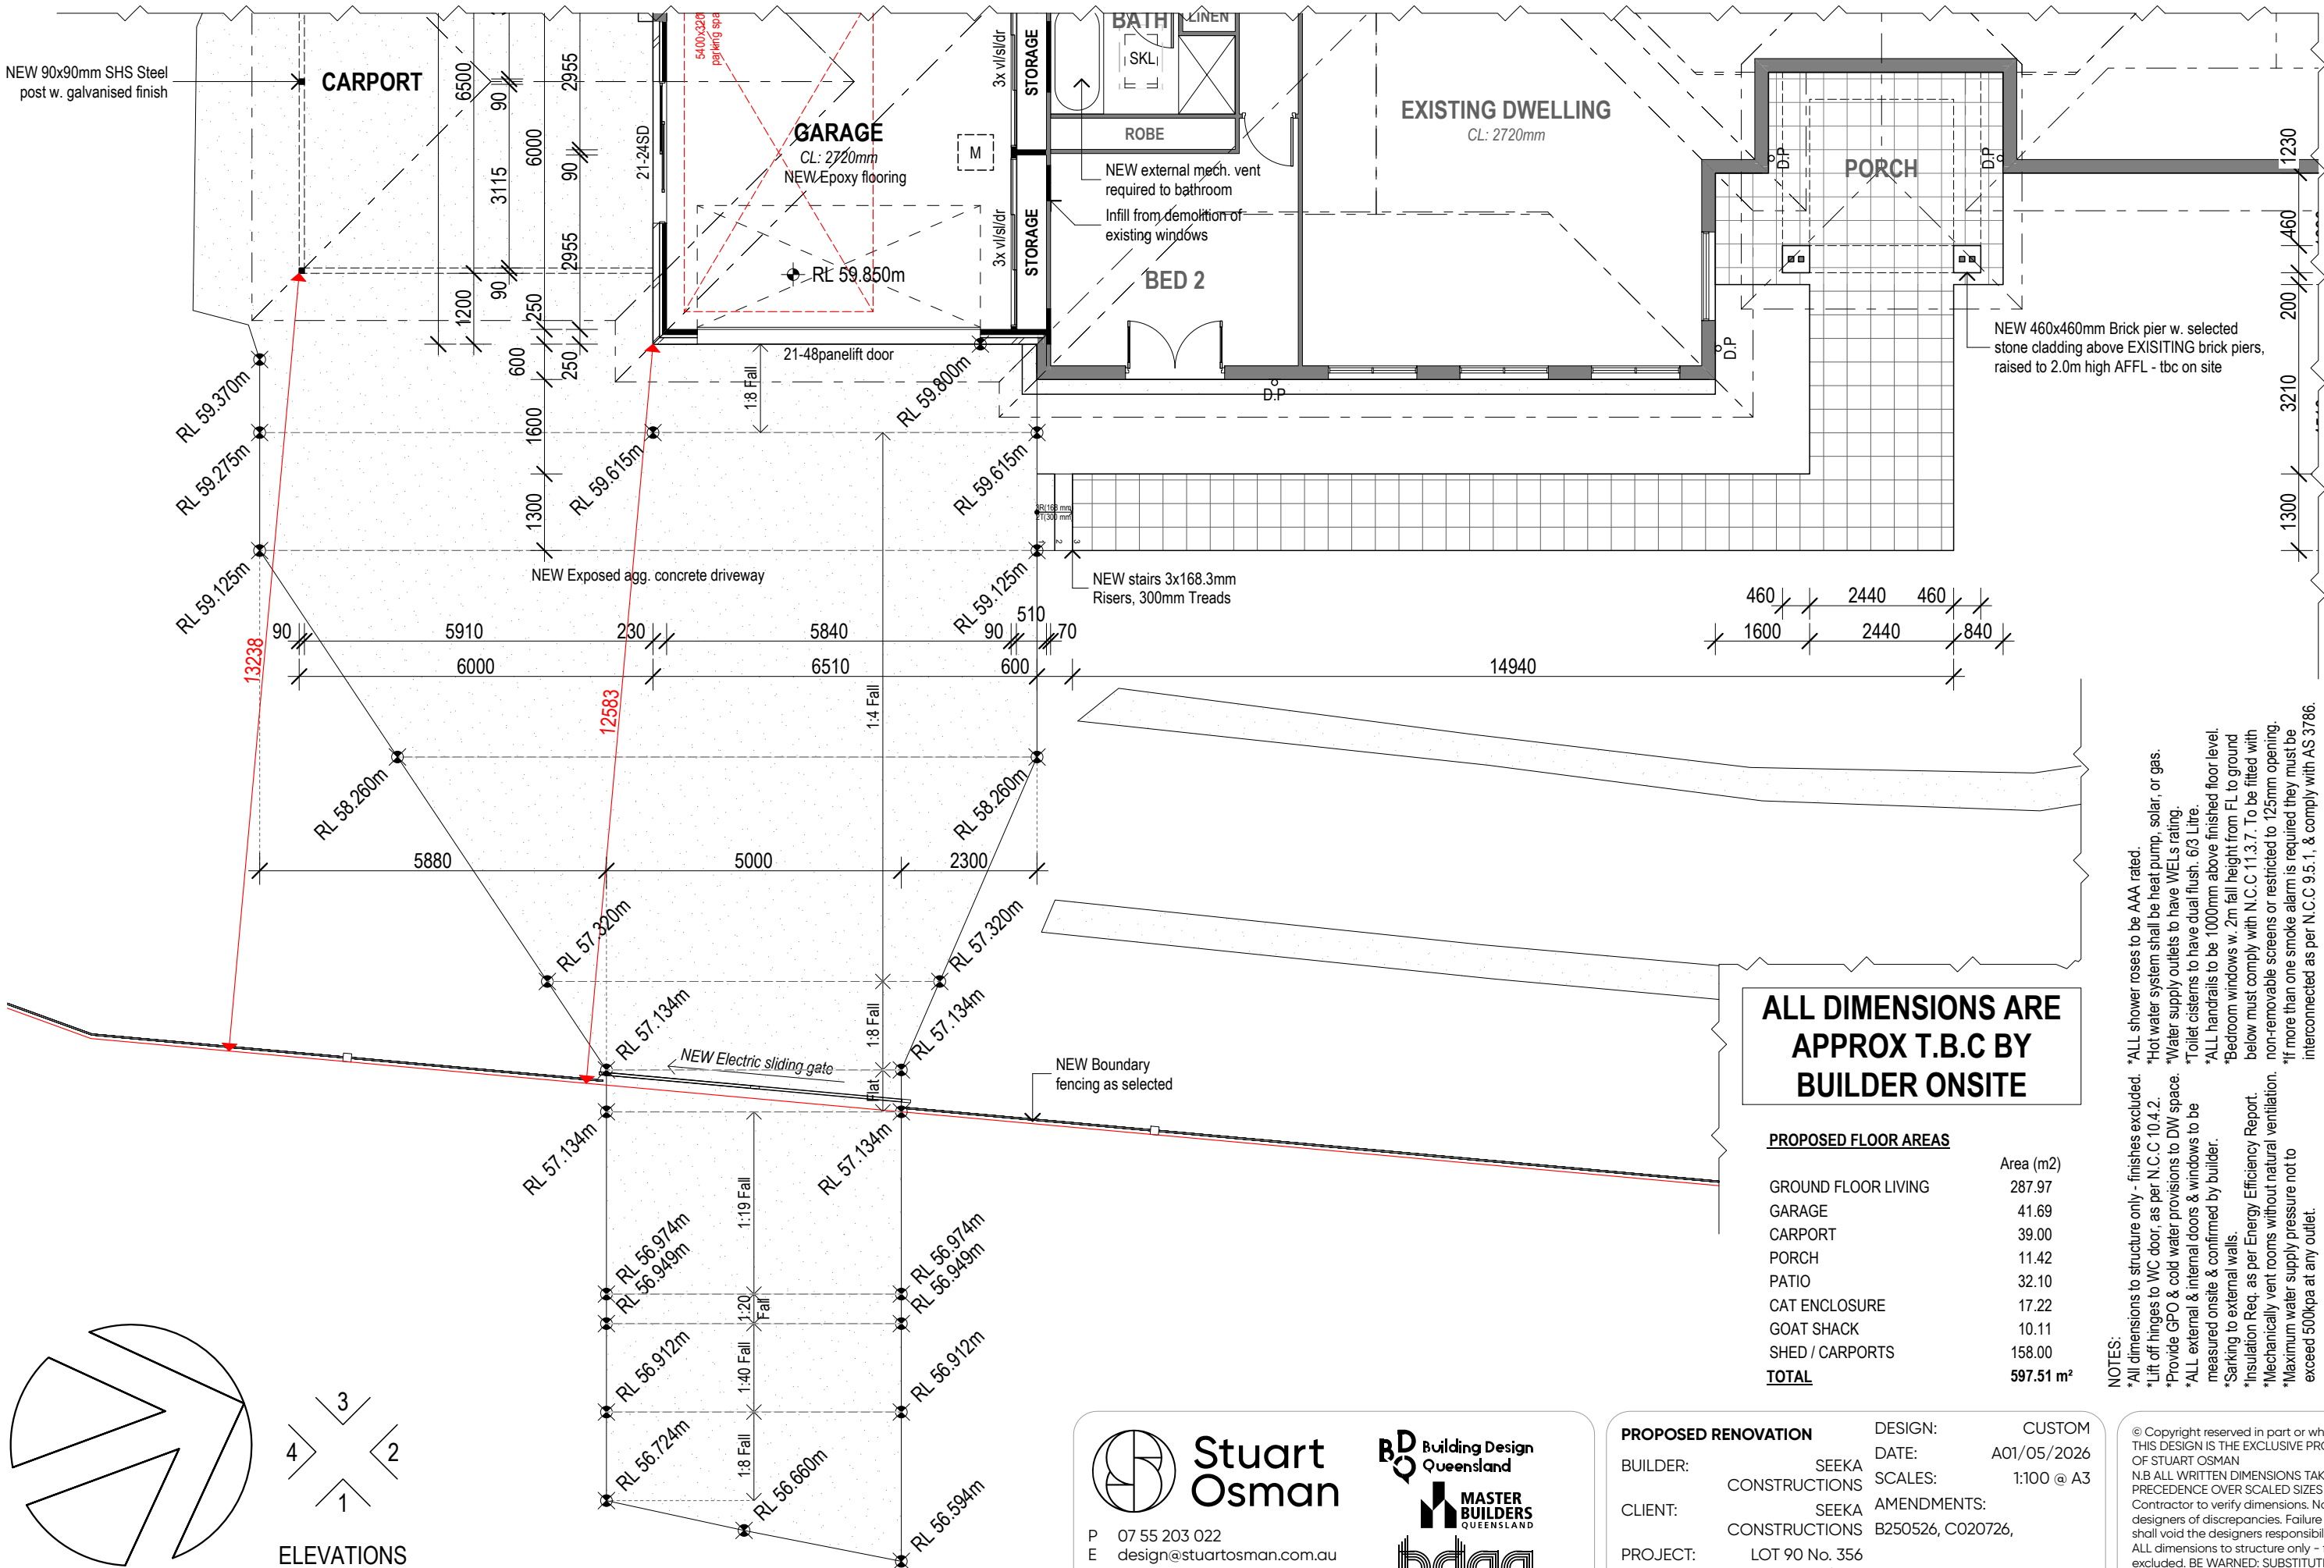

PRELIMINARY PLANS ONLY NOT FOR CONSTRUCTION

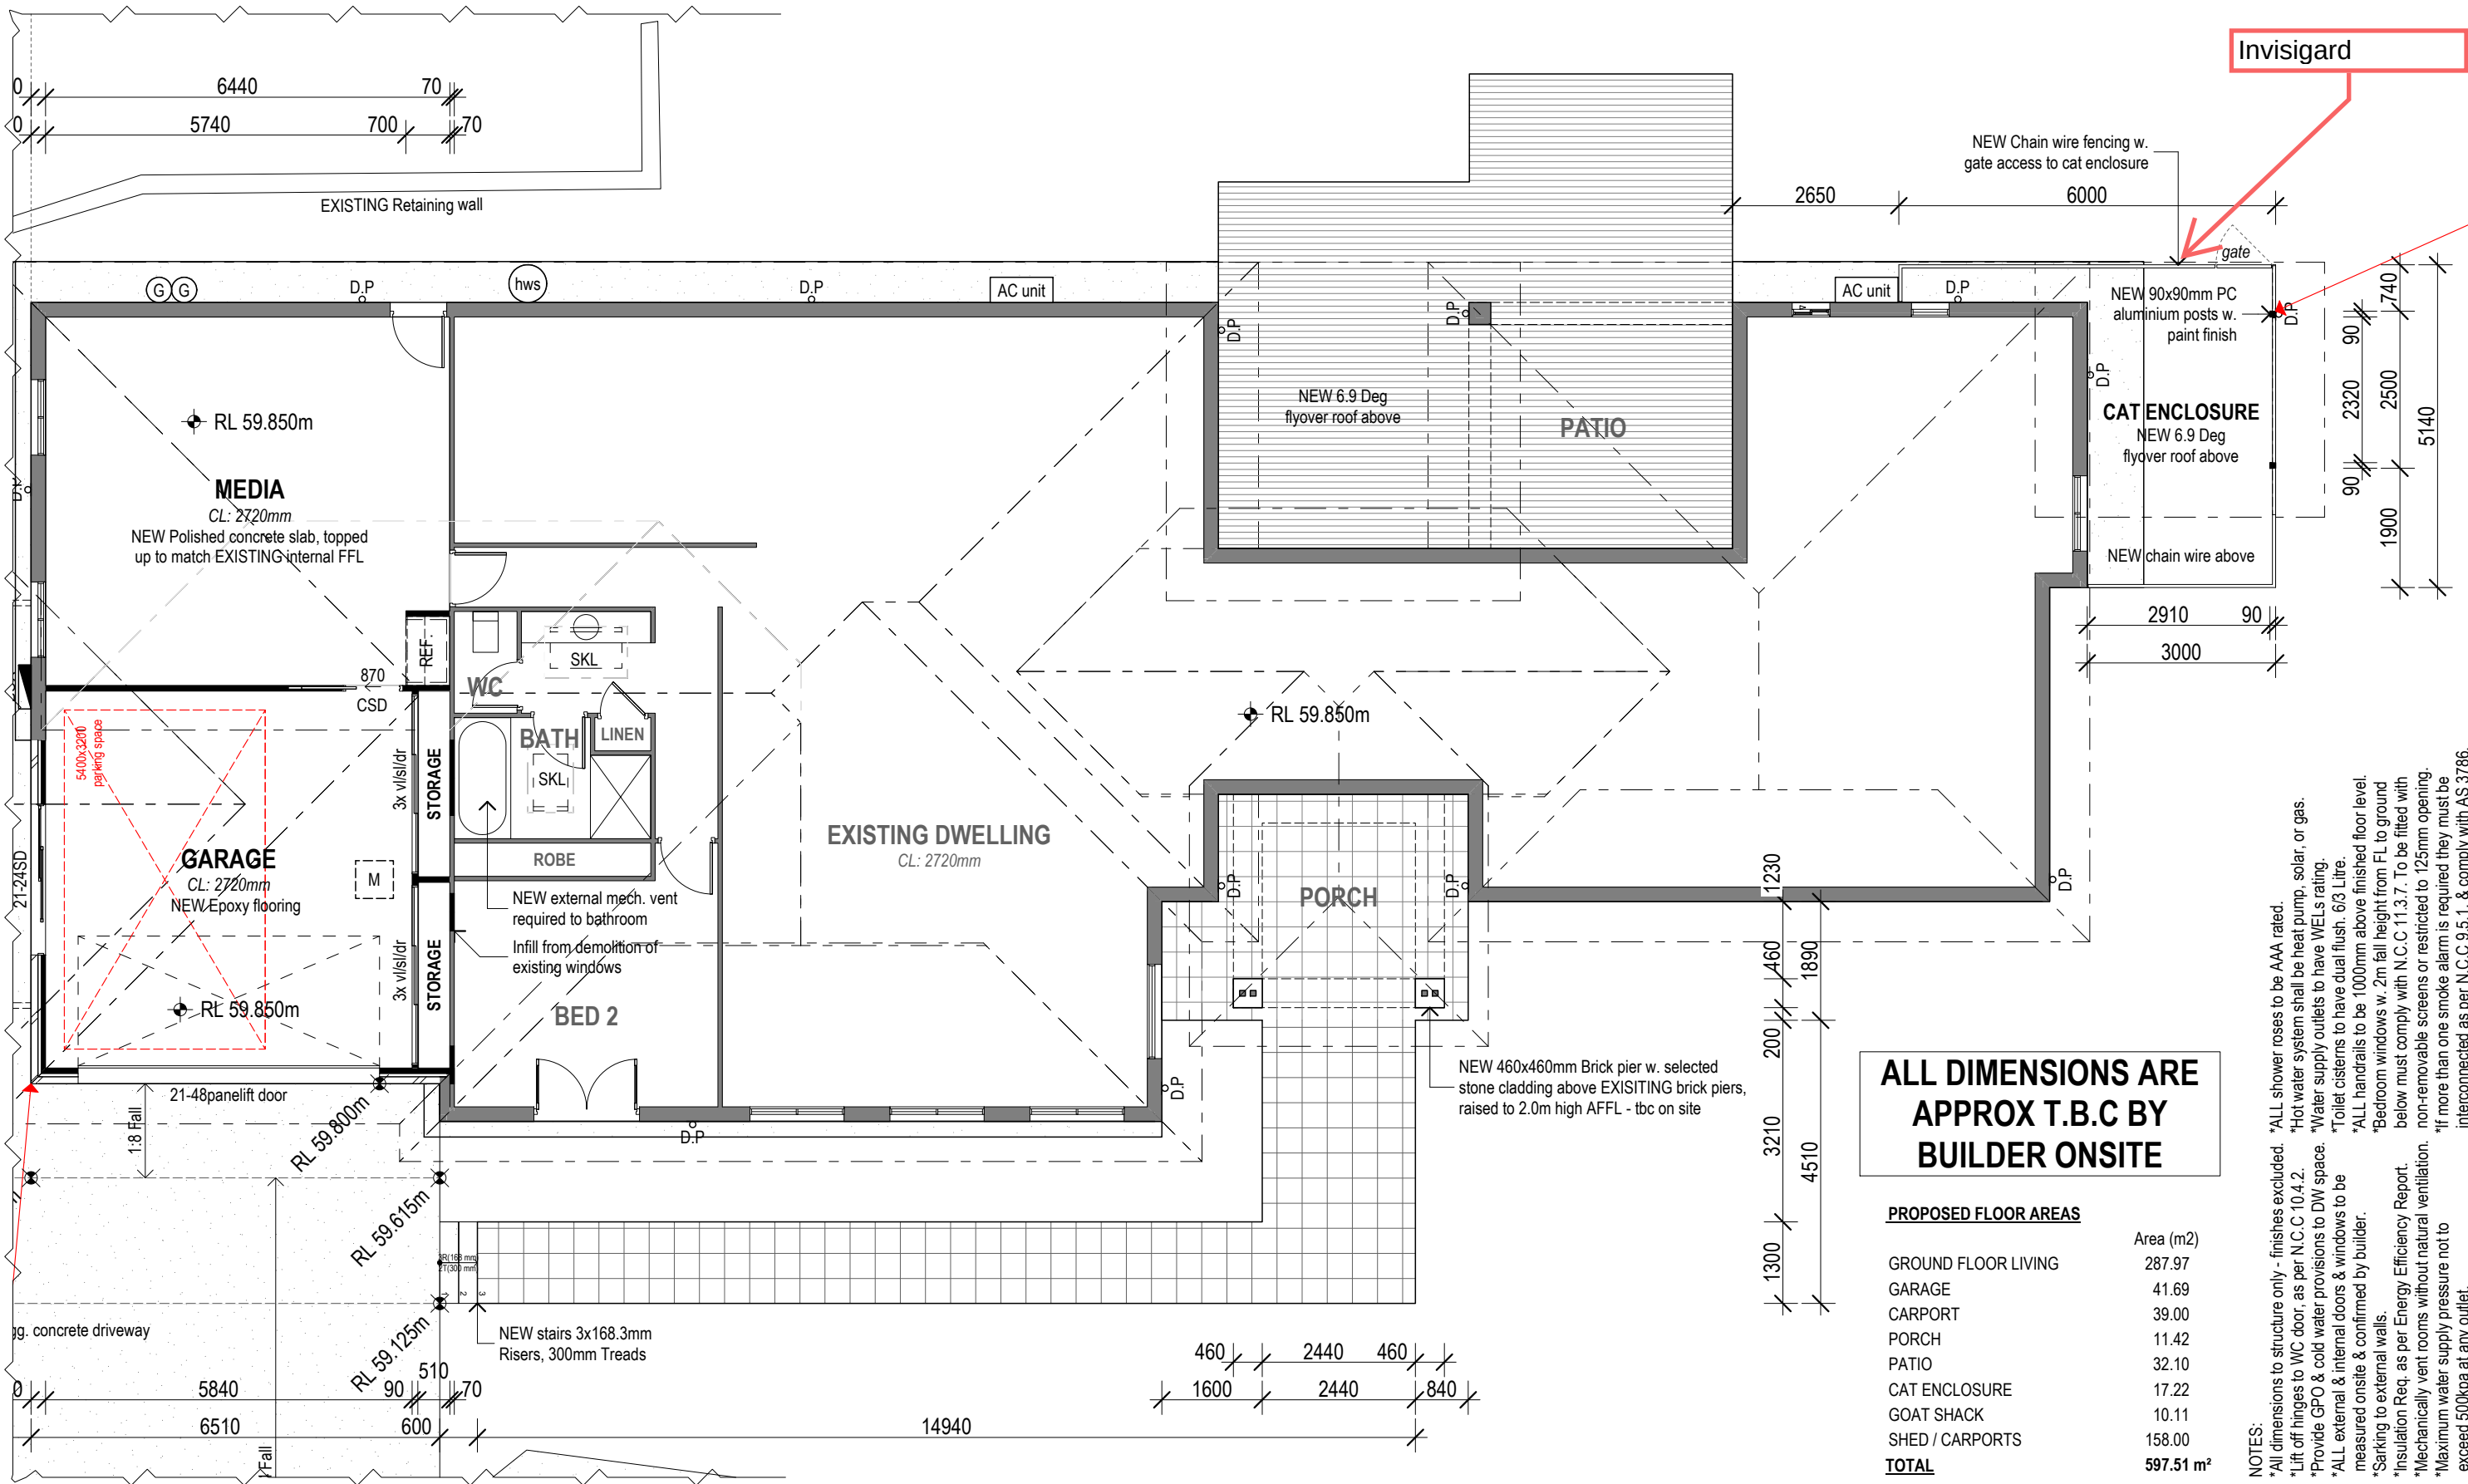


ALL DIMENSIONS ARE APPROX T.B.C BY BUILDER ONSITE

PROPOSED FLOOR AREAS	
	Area (m2)
GROUND FLOOR LIVING	287.97
GARAGE	41.69
CARPORT	39.00
PORCH	11.42
PATIO	32.10
CAT ENCLOSURE	17.22
GOAT SHACK	10.11
SHED / CARPORTS	158.00
TOTAL	597.51 m ²

- NOTES:
- *All dimensions to structure only - finishes excluded.
 - *Lift off hinges to WC door, as per N.C.C 10.4.2.
 - *Provide GPO & cold water provisions to DW space.
 - *ALL external & internal doors & windows to be measured onsite & confirmed by builder.
 - *Sarking to external walls.
 - *Insulation Req. as per Energy Efficiency Report.
 - *Mechanically vent rooms without natural ventilation.
 - *Maximum water supply pressure not to exceed 500kpa at any outlet.
 - *All shower roses to be AAA rated.
 - *Hot water system shall be heat pump, solar, or gas.
 - *Water supply outlets to have WELs rating.
 - *Toilet cisterns to have dual flush, 6/3 Litre.
 - *ALL handrails to be 1000mm above finished floor level.
 - *Bedroom windows w. 2m fall height from FL to ground below must comply with N.C.C 11.3.7. To be fitted with non-removable screens or restricted to 125mm opening.
 - *If more than one smoke alarm is required they must be interconnected as per N.C.C 9.5.1, & comply with AS 3786.

ELEVATIONS
PROPOSED GROUND FLOOR PLAN
SCALE 1:100

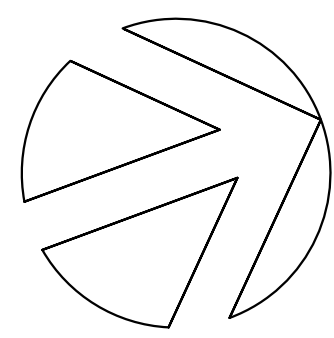

Stuart Osman
P 07 55 203 022
E design@stuartosman.com.au
Studio 2/71 Township Dr,
West Burleigh, QLD 4219
PO BOX 2845
Burleigh Heads DC QLD 4220



Building Design Queensland
MASTER BUILDERS QUEENSLAND
bdqa
BUILDING DESIGNERS ASSOCIATION OF AUSTRALIA
ABN 73 097 995 616
QBCC License No: 1129687

PROPOSED RENOVATION		DESIGN:	CUSTOM
BUILDER:	SEEKA CONSTRUCTIONS	DATE:	A01/05/2026
CLIENT:	SEEKA CONSTRUCTIONS	SCALES:	1:100 @ A3
PROJECT:	LOT 90 No. 356 RUFFLES RD WILLOWVALE	AMENDMENTS:	B250526, C020726,
DRAWN BY:	EP/RS	SHEET NUMBER:	13 of 24
CHECKED BY:	SO	JOB NUMBER:	10588


© Copyright reserved in part or whole. THIS DESIGN IS THE EXCLUSIVE PROPERTY OF STUART OSMAN
N.B ALL WRITTEN DIMENSIONS TAKE PRECEDENCE OVER SCALED SIZES
Contractor to verify dimensions. Notify designers of discrepancies. Failure to do so shall void the designers responsibilities.
ALL dimensions to structure only - finishes excluded. BE WARNED: SUBSTITUTION OF ANY STRUCTURAL MEMBERS, AND OR ANY VARIATION TO ANY PART OF THE DESIGN WILL VOID ANY RESPONSIBILITIES OF STUART OSMAN FOR THE STRUCTURAL INTEGRITY AND PERFORMANCE OF THE BUILDING.

PRELIMINARY PLANS ONLY NOT FOR CONSTRUCTION

ALL DIMENSIONS ARE
APPROX T.B.C BY
BUILDER ONSITE

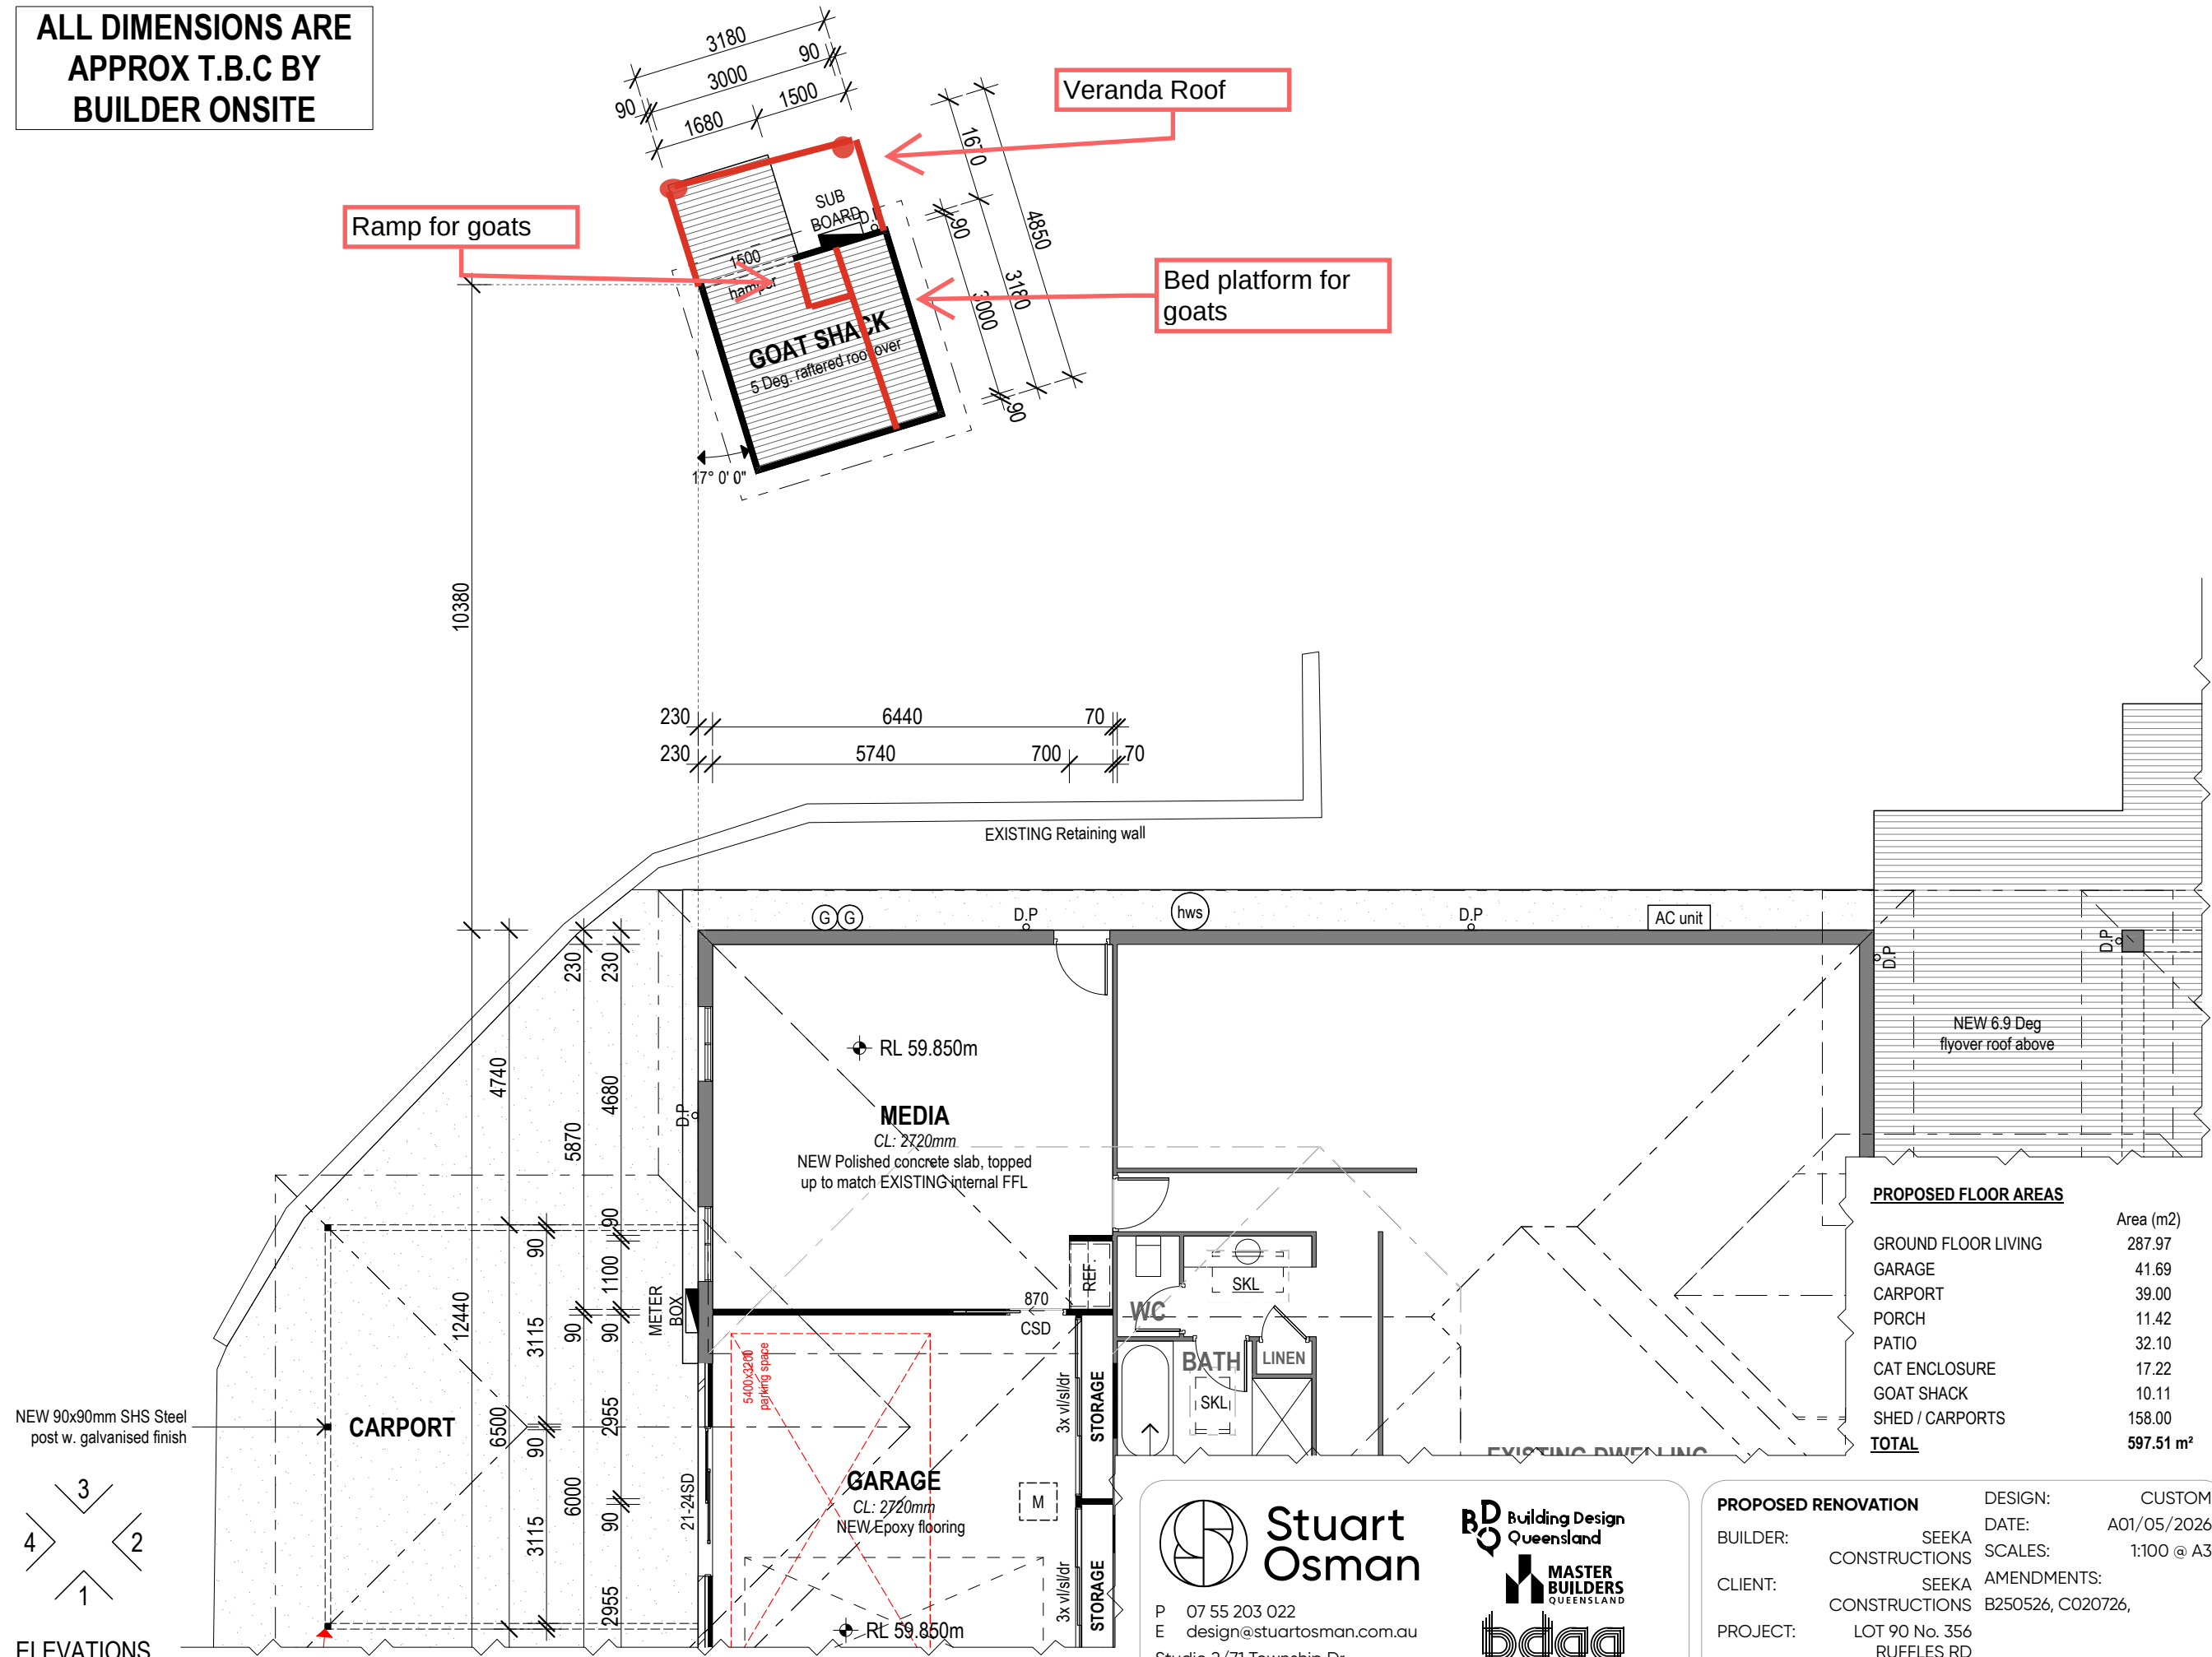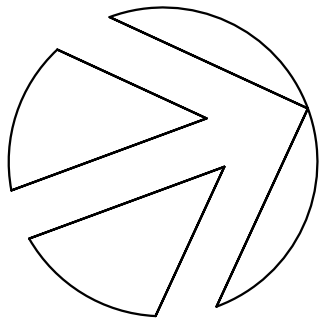


NEW 90x90mm SHS Steel
post w. galvanised finish

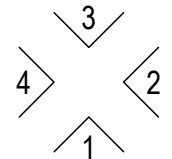

ELEVATIONS
PROPOSED GROUND FLOOR PLAN
SCALE 1:100

PROPOSED FLOOR AREAS	
	Area (m2)
GROUND FLOOR LIVING	287.97
GARAGE	41.69
CARPORT	39.00
PORCH	11.42
PATIO	32.10
CAT ENCLOSURE	17.22
GOAT SHACK	10.11
SHED / CARPORTS	158.00
TOTAL	597.51 m²

- NOTES:
- *All dimensions to structure only - finishes excluded.
 - *All shower roses to be AAA rated.
 - *Lift off hinges to WC door, as per N.C.C 10.4.2.
 - *Hot water system shall be heat pump, solar, or gas.
 - *Provide GPO & cold water provisions to DW space.
 - *Water supply outlets to have WELs rating.
 - *ALL external & internal doors & windows to be measured onsite & confirmed by builder.
 - *Toilet cisterns to have dual flush, 6/3 Litre.
 - *Sarking to external walls.
 - *ALL handrails to be 1000mm above finished floor level.
 - *Bedroom windows w. 2m fall height from FL to ground below must comply with N.C.C 11.3.7. To be fitted with non-removable screens or restricted to 125mm opening.
 - *Insulation Req. as per Energy Efficiency Report.
 - *If more than one smoke alarm is required they must be interconnected as per N.C.C 9.5.1, & comply with AS 3786.
 - *Maximum water supply pressure not to exceed 500kpa at any outlet.

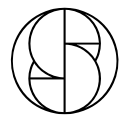

**Stuart
Osman**

P 07 55 203 022
E design@stuartosman.com.au

Studio 2/71 Township Dr,
West Burleigh, QLD 4219
PO BOX 2845
Burleigh Heads DC QLD 4220



**Building Design
Queensland**



**MASTER
BUILDERS
QUEENSLAND**





**BUILDING DESIGNERS
ASSOCIATION OF AUSTRALIA**

ABN 73 097 995 616
QBCC License No: 1129687


PROPOSED RENOVATION	DESIGN: CUSTOM
BUILDER: SEEKA CONSTRUCTIONS	DATE: A01/05/2026
CLIENT: SEEKA CONSTRUCTIONS	SCALES: 1:100 @ A3
PROJECT: LOT 90 No. 356 RUFFLES RD WILLOWVALE	AMENDMENTS: B250526, C020726,
DRAWN BY: EP/RS	SHEET NUMBER: 14 of 24
CHECKED BY: SO	JOB NUMBER: 10588

© Copyright reserved in part or whole. THIS DESIGN IS THE EXCLUSIVE PROPERTY OF STUART OSMAN
N.B ALL WRITTEN DIMENSIONS TAKE PRECEDENCE OVER SCALED SIZES
Contractor to verify dimensions. Notify designers of discrepancies. Failure to do so shall void the designers responsibilities.
ALL dimensions to structure only - finishes excluded. BE WARNED: SUBSTITUTION OF ANY STRUCTURAL MEMBERS, AND OR ANY VARIATION TO ANY PART OF THE DESIGN WILL VOID ANY RESPONSIBILITIES OF STUART OSMAN FOR THE STRUCTURAL INTEGRITY AND PERFORMANCE OF THE BUILDING.

PRELIMINARY PLANS ONLY NOT FOR CONSTRUCTION

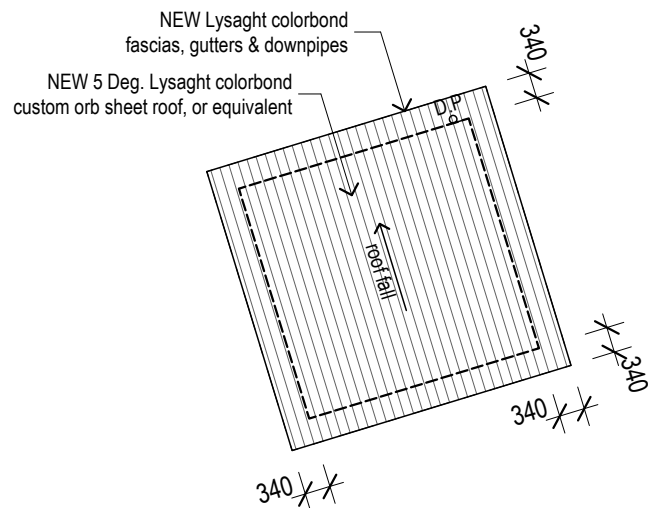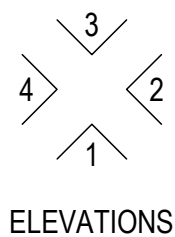

ALL DIMENSIONS ARE APPROX
T.B.C BY BUILDER ONSITE

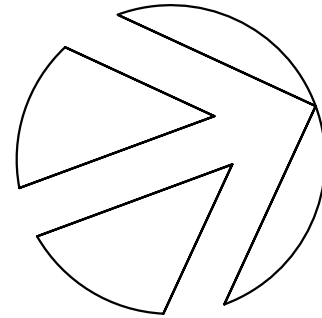

- NOTES:
- *All dimensions to structure only - finishes excluded.
 - *Lift off hinges to WC door, as per N.C.C 10.4.2.
 - *Provide GPO & cold water provisions to DW space.
 - *ALL external & internal doors & windows to be measured onsite & confirmed by builder.
 - *Sarking to external walls.
 - *Insulation Req. as per Energy Efficiency Report.
 - *Mechanically vent rooms without natural ventilation.
 - *ALL shower roses to be AAA rated.
 - *Maximum water supply pressure not to exceed 500kpa at any outlet.
 - *Hot water system shall be heat pump, solar, or gas.
 - *Water supply outlets to have WELs rating.
 - *Toilet cisterns to have dual flush. 6/3 Litre.
 - *ALL handrails to be 1000mm above finished floor level.
 - *Bedroom windows w. 2m fall height from FL to ground below must comply with N.C.C 11.3.7. To be fitted with non-removable screens or restricted to 125mm opening.
 - *If more than one smoke alarm is required they must be interconnected as per N.C.C 9.5.1, & comply with AS 3786.



P 07 55 203 022
E design@stuartosman.com.au

Studio 2/71 Township Dr,
West Burleigh, QLD 4219

PO BOX 2845
Burleigh Heads DC QLD 4220

ABN 73 097 995 616
QBCC License No: 1129687



PROPOSED RENOVATION

BUILDER:SEEKA CONSTRUCTIONS

CLIENT: SEEKA CONSTRUCTIONS

PROJECT: LOT 90 No. 356
RUFFLES RD
WILLOWVALE

DRAWN BY: EP/RS

CHECKED BY: SO

DESIGN: CUSTOM

DATE: A01/05/2026


SCALES: 1:100 @ A3

AMENDMENTS:
B250526, C020726,

SHEET NUMBER: 15 of 24

JOB NUMBER: 10588

© Copyright reserved in part or whole.
THIS DESIGN IS THE EXCLUSIVE PROPERTY
OF STUART OSMAN
N.B ALL WRITTEN DIMENSIONS TAKE
PRECEDENCE OVER SCALED SIZES
Contractor to verify dimensions. Notify
designers of discrepancies. Failure to do so
shall void the designers responsibilities.
ALL dimensions to structure only - finishes
excluded. BE WARNED: SUBSTITUTION OF
ANY STRUCTURAL MEMBERS, AND OR ANY
VARIATION TO ANY PART OF THE DESIGN
WILL VOID ANY RESPONSIBILITIES OF STUART
OSMAN FOR THE STRUCTURAL INTEGRITY
AND PERFORMANCE OF THE BUILDING.

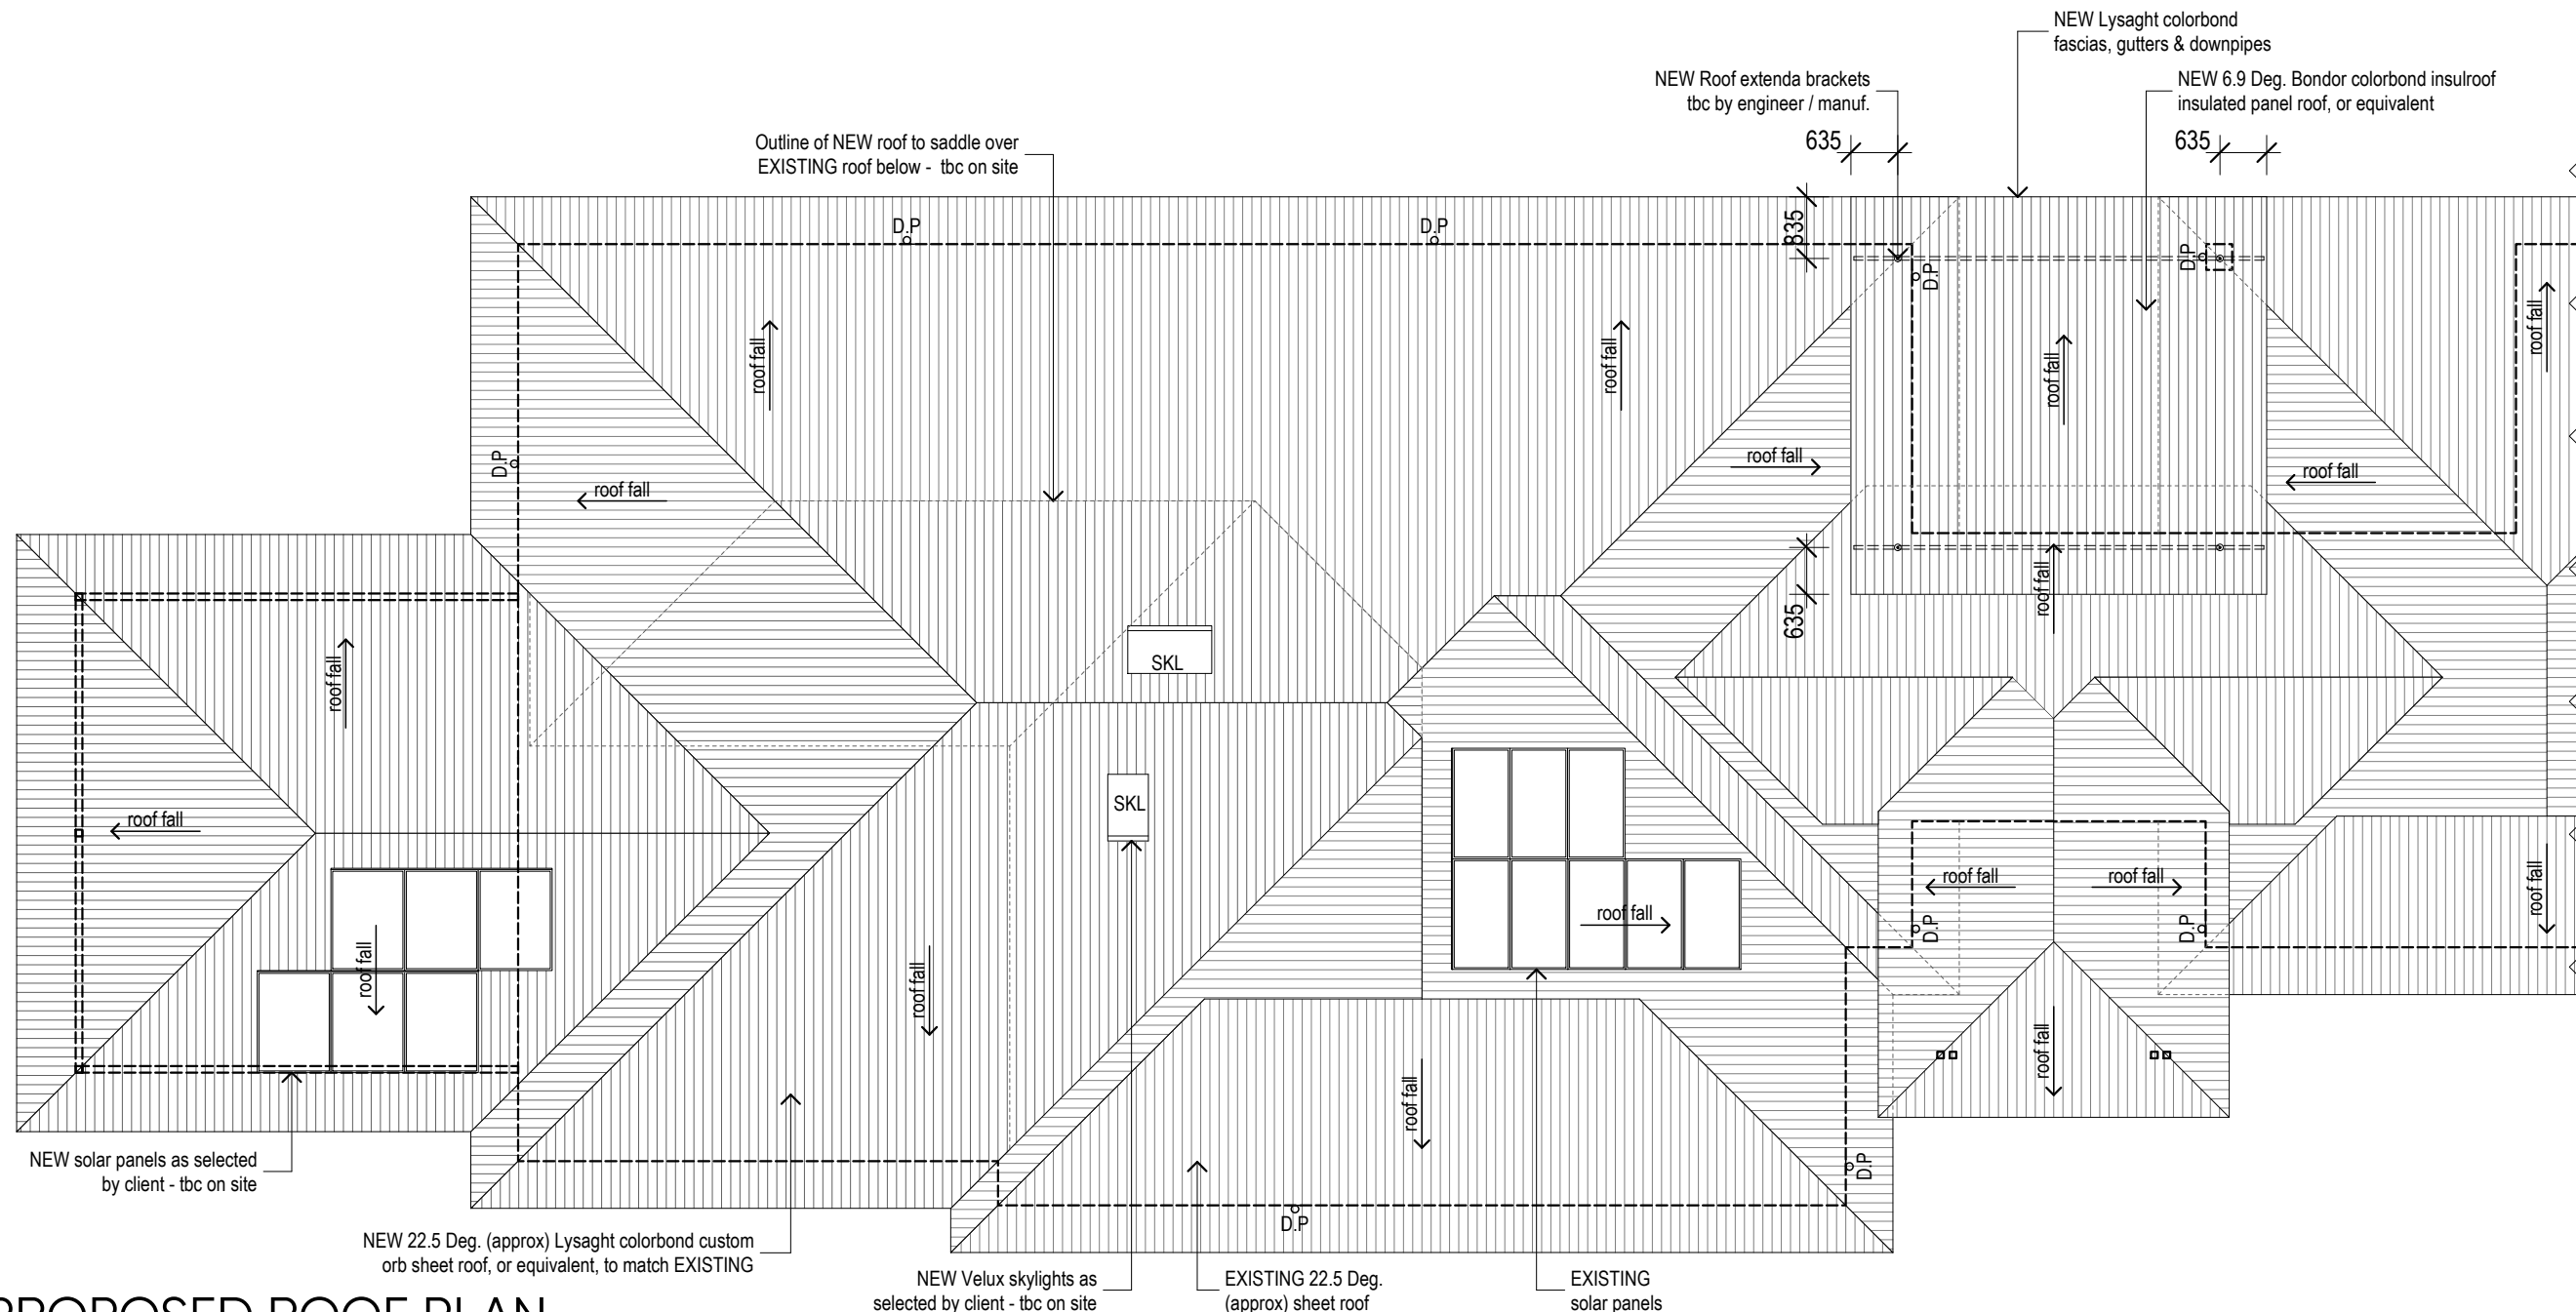

PROPOSED ROOF PLAN

SCALE 1:100


PRELIMINARY PLANS ONLY NOT FOR CONSTRUCTION

- *All dimensions to structure only - finishes excluded.
- *Lift off hinges to WC door, as per N.C.C 10.4.2.
- *Provide GPO & cold water provisions to DW space.
- *ALL external & internal doors & windows to be measured onsite & confirmed by builder.
- *Sarking to external walls.
- *Insulation Req. as per Energy Efficiency Report.
- *Mechanically vent rooms without natural ventilation.
- *ALL shower roses to be AAA rated.
- *Maximum water supply pressure not to exceed 500kpa at any outlet.
- *Hot water system shall be heat pump, solar, or gas.
- *Water supply outlets to have WELs rating.
- *Toilet cisterns to have dual flush. 6/3 Litre.
- *ALL handrails to be 1000mm above finished floor level.
- *Bedroom windows w. 2m fall height from FL to ground below must comply with N.C.C 11.3.7. To be fitted with non-removable screens or restricted to 125mm opening.
- *If more than one smoke alarm is required they must be interconnected as per N.C.C 9.5.1, & comply with AS 3786.





JOB NUMBER: 10588

© Copyright reserved in part or whole.
THIS DESIGN IS THE EXCLUSIVE PROPERTY
OF STUART OSMAN
N.B ALL WRITTEN DIMENSIONS TAKE
PRECEDENCE OVER SCALED SIZES
Contractor to verify dimensions. Notify
designers of discrepancies. Failure to do so
shall void the designers responsibilities.
ALL dimensions to structure only - finishes
excluded. BE WARNED: SUBSTITUTION OF
ANY STRUCTURAL MEMBERS, AND OR ANY
VARIATION TO ANY PART OF THE DESIGN
WILL VOID ANY RESPONSIBILITIES OF STUART
OSMAN FOR THE STRUCTURAL INTEGRITY
AND PERFORMANCE OF THE BUILDING.

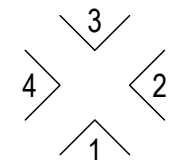


PRELIMINARY PLANS ONLY NOT FOR CONSTRUCTION

NOTES:
*All dimensions to structure only - finishes excluded.
*ALL external & internal doors & windows to be measured onsite & confirmed by builder.
*Sarking to external walls.
*Insulation Req. as per Energy Efficiency Report.
*Hot water system shall be heat pump, solar, or gas.
*Water supply outlets to have WELs rating.
*ALL handrails to be 1000mm above finished floor level.
*Bedroom windows w. 2m fall height from FL to ground below must comply with N.C.C 11.3.7. To be fitted with non-removable screens or restricted to 125mm opening.

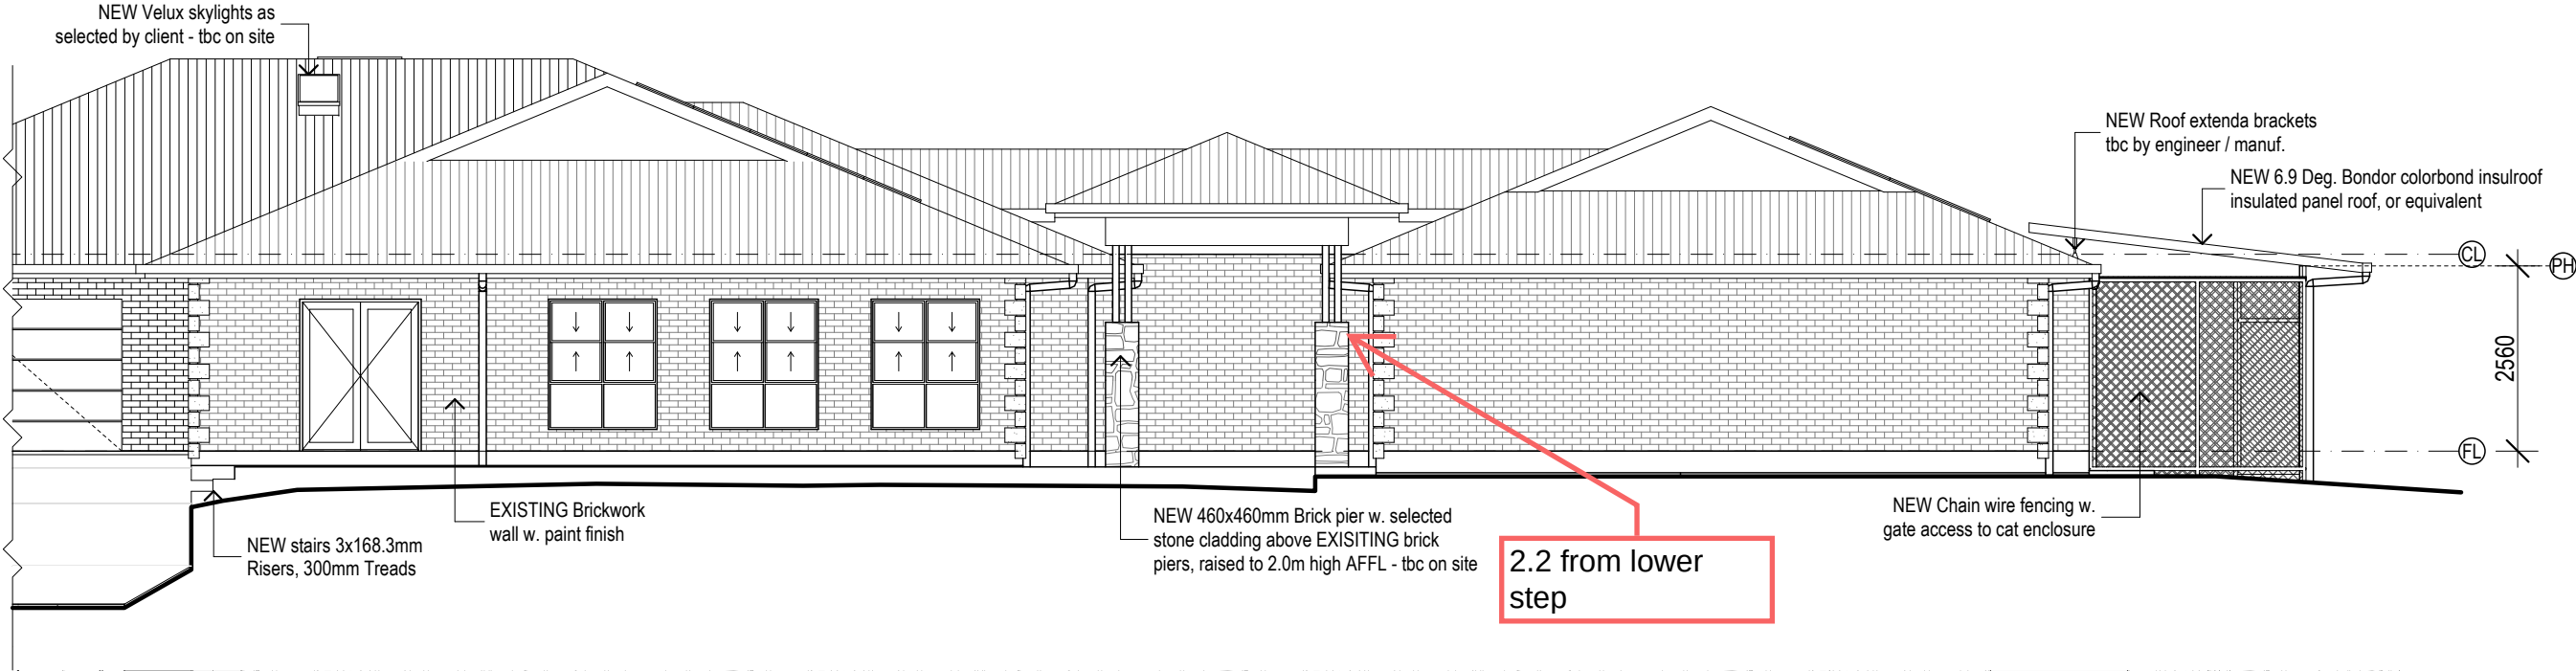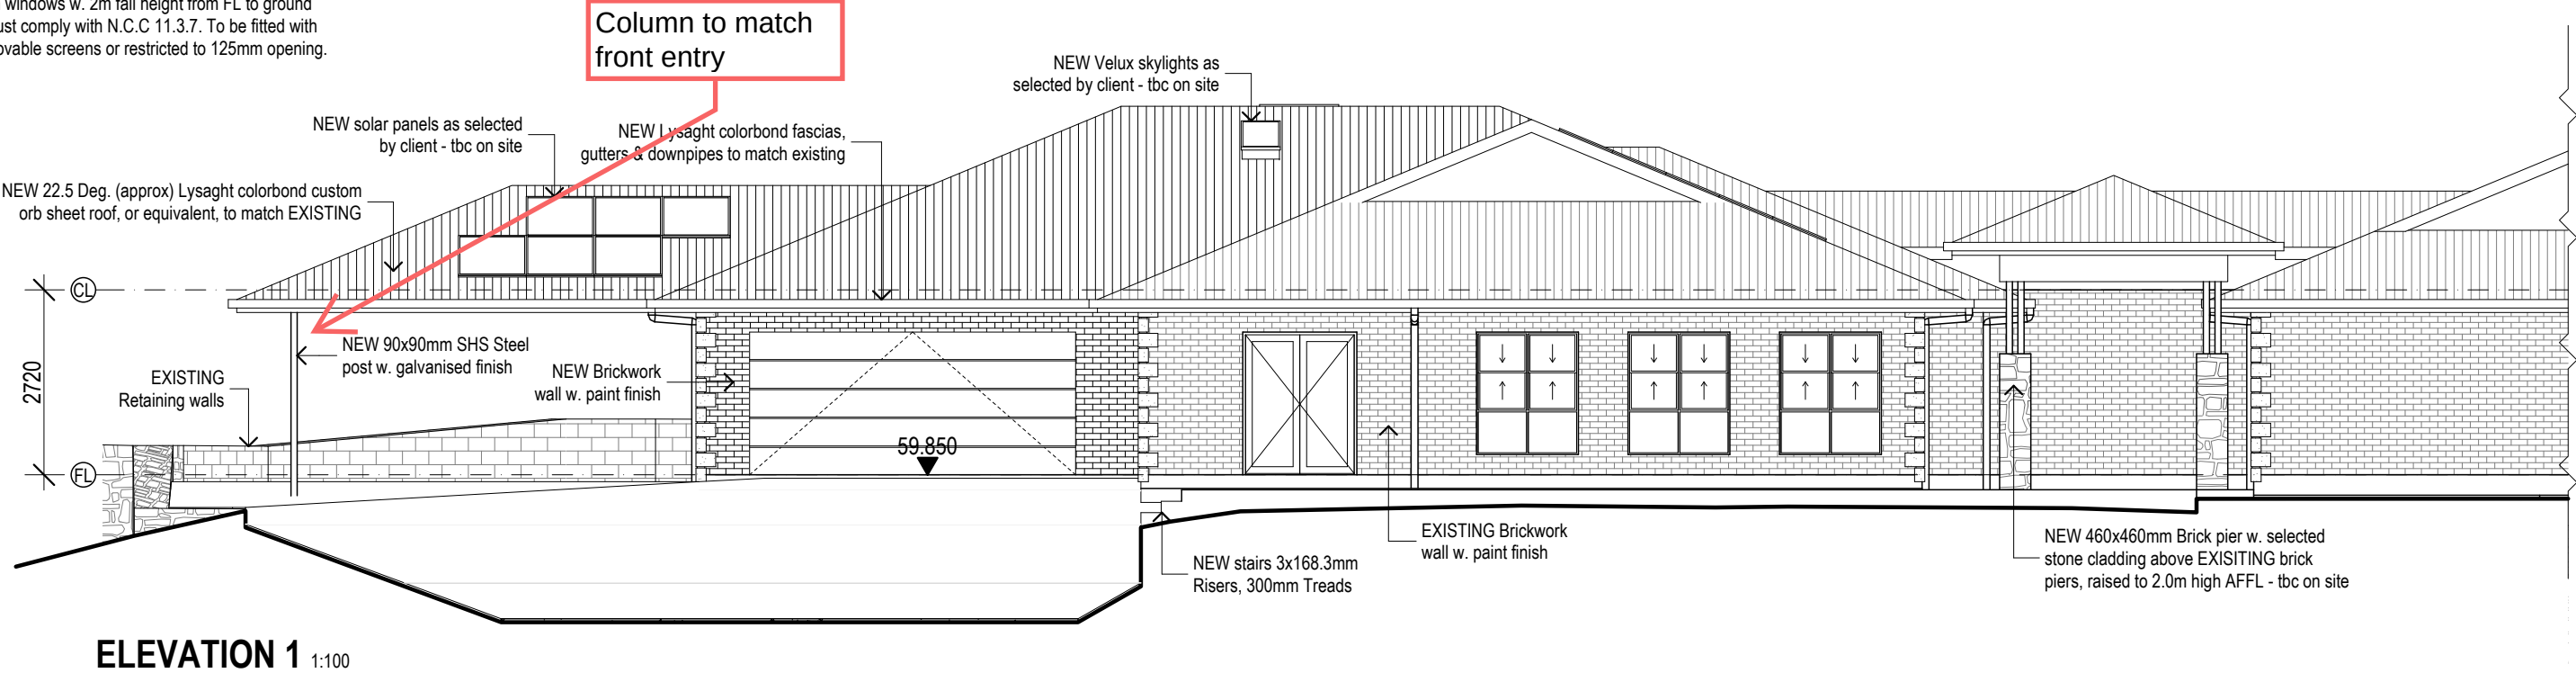

PRELIMINARY PLANS ONLY NOT FOR CONSTRUCTION

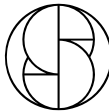

**Stuart
Osman**

P 07 55 203 022
E design@stuartosman.com.au
Studio 2/71 Township Dr,
West Burleigh, QLD 4219
PO BOX 2845
Burleigh Heads DC QLD 4220

BD Building Design
Queensland

**MASTER
BUILDERS
QUEENSLAND**

bdaa
BUILDING DESIGNERS
ASSOCIATION OF AUSTRALIA

ABN 73 097 995 616
QBCC License No: 1129687

PROPOSED RENOVATION

BUILDER: SEEKA
CONSTRUCTIONS
CLIENT: SEEKA
CONSTRUCTIONS
PROJECT: LOT 90 No. 356
RUFFLES RD
WILLOWVALE

DESIGN: CUSTOM
DATE: A01/05/2026
SCALES: 1:100 @ A3
AMENDMENTS:
B250526, C020726,
DRAWN BY: EP/RS SHEET NUMBER: 17 of 24
CHECKED BY: SO JOB NUMBER: 10588

© Copyright reserved in part or whole.
THIS DESIGN IS THE EXCLUSIVE PROPERTY
OF STUART OSMAN
N.B ALL WRITTEN DIMENSIONS TAKE
PRECEDENCE OVER SCALED SIZES
Contractor to verify dimensions. Notify
designers of discrepancies. Failure to do so
shall void the designers responsibilities.
ALL dimensions to structure only - finishes
excluded. BE WARNED: SUBSTITUTION OF
ANY STRUCTURAL MEMBERS, AND OR ANY
VARIATION TO ANY PART OF THE DESIGN
WILL VOID ANY RESPONSIBILITIES OF
STUART OSMAN FOR THE STRUCTURAL
INTEGRITY AND PERFORMANCE OF THE
BUILDING.

PROPOSED RENOVATION

BUILDER: SEEKA CONSTRUCTIONS

CLIENT: SEEKA CONSTRUCTIONS

PROJECT: LOT 90 No. 356
RUFFLES RD
WILLOWVALE

DRAWN BY: EP/RS

CHECKED BY: SO

DESIGN: CUSTOM

DATE: A01/05/2026

SCALES: 1:100 @ A3


AMENDMENTS:
B250526, C020726,

SHEET NUMBER: 18 of 24


JOB NUMBER: **10588**

© Copyright reserved in part or whole.
THIS DESIGN IS THE EXCLUSIVE PROPERTY
OF STUART OSMAN
N.B ALL WRITTEN DIMENSIONS TAKE
PRECEDENCE OVER SCALED SIZES
Contractor to verify dimensions. Notify
designers of discrepancies. Failure to do so
shall void the designers responsibilities.
ALL dimensions to structure only - finishes
excluded. BE WARNED: SUBSTITUTION OF
ANY STRUCTURAL MEMBERS, AND OR ANY
VARIATION TO ANY PART OF THE DESIGN
WILL VOID ANY RESPONSIBILITIES OF STUART
OSMAN FOR THE STRUCTURAL INTEGRITY
AND PERFORMANCE OF THE BUILDING.


NOTES:
*All dimensions to structure only - finishes excluded.
*ALL external & internal doors & windows to be
measured onsite & confirmed by builder.
*Sarking to external walls.
*Insulation Req. as per Energy Efficiency Report.
*Hot water system shall be heat pump, solar, or gas.
*Water supply outlets to have WELs rating.
*ALL handrails to be 1000mm above finished floor level.
*Bedroom windows w. 2m fall height from FL to ground
below must comply with N.C.C 11.3.7. To be fitted with
non-removable screens or restricted to 125mm opening.

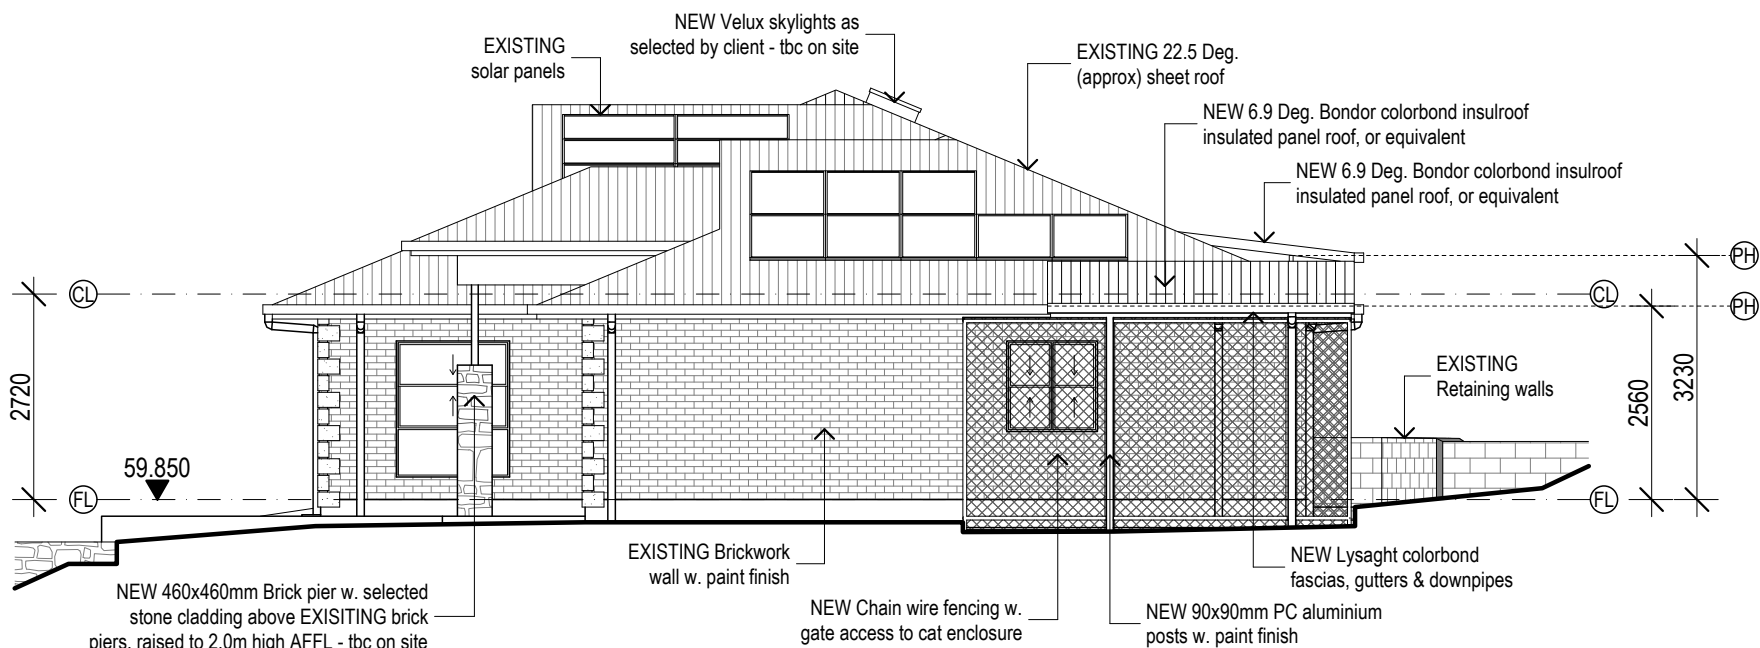


ELEVATION 2 1:100

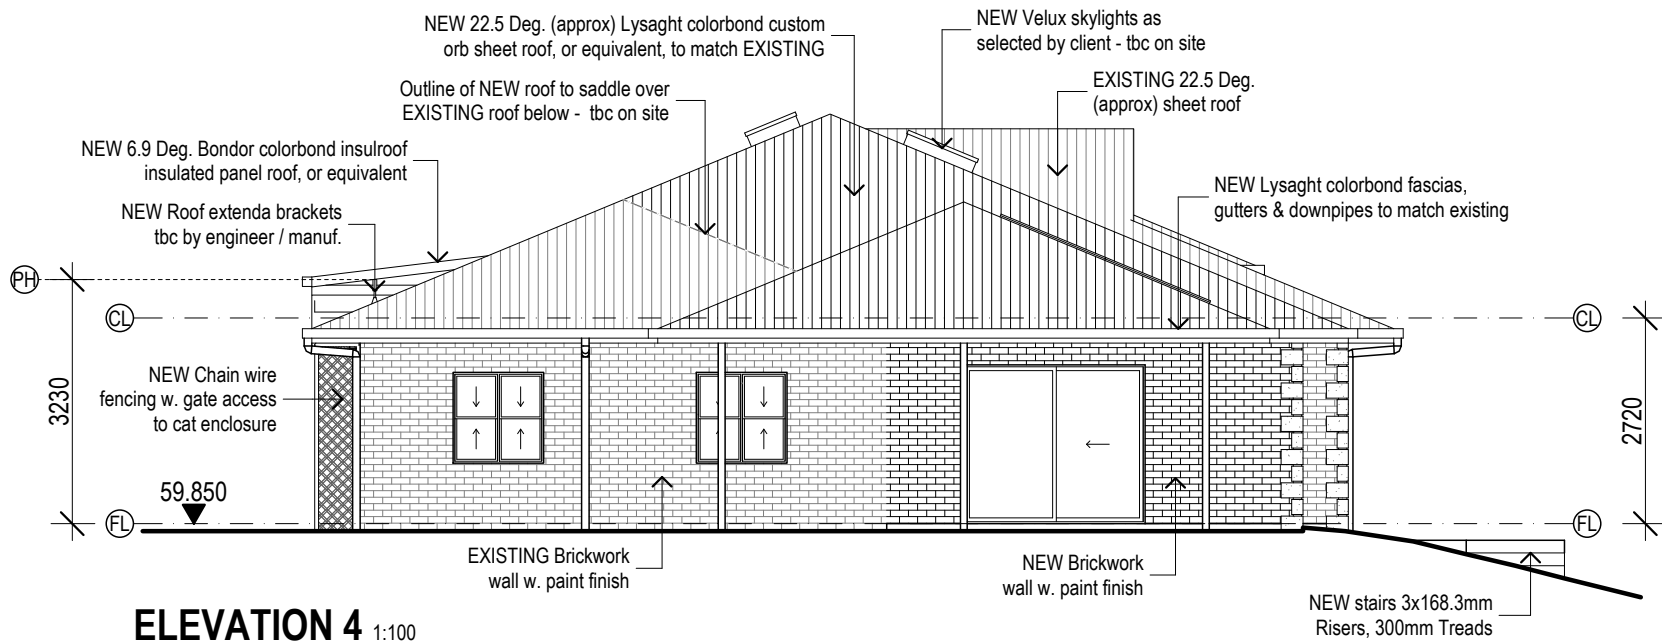


ELEVATION 4 1:100

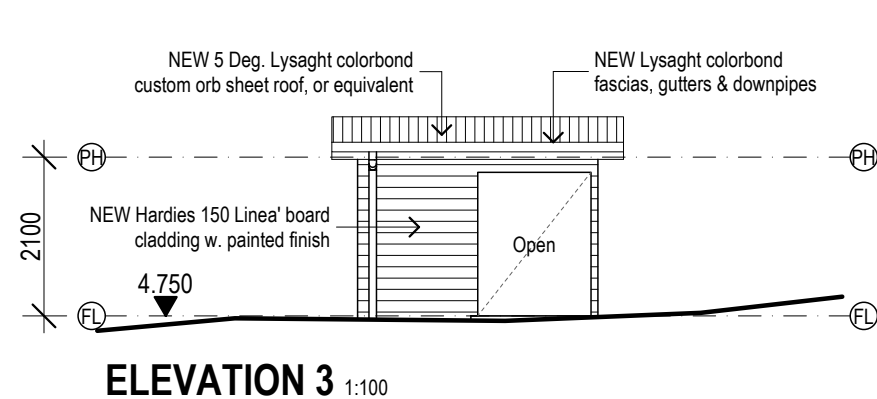


ELEVATION 3 1:100

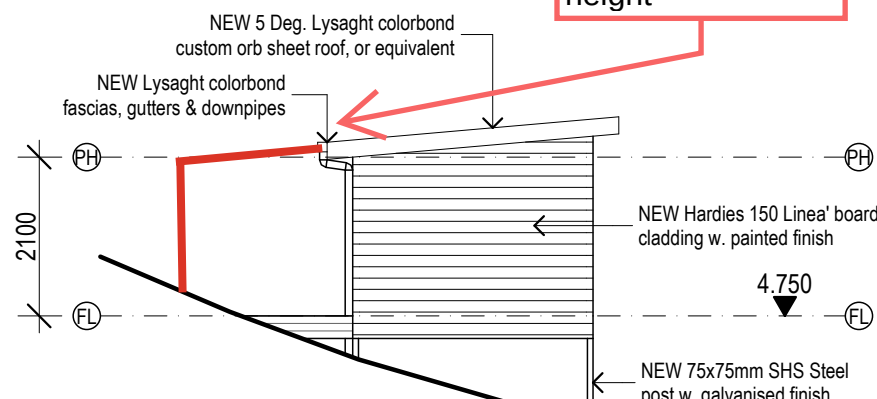

ELEVATION 4 1:100

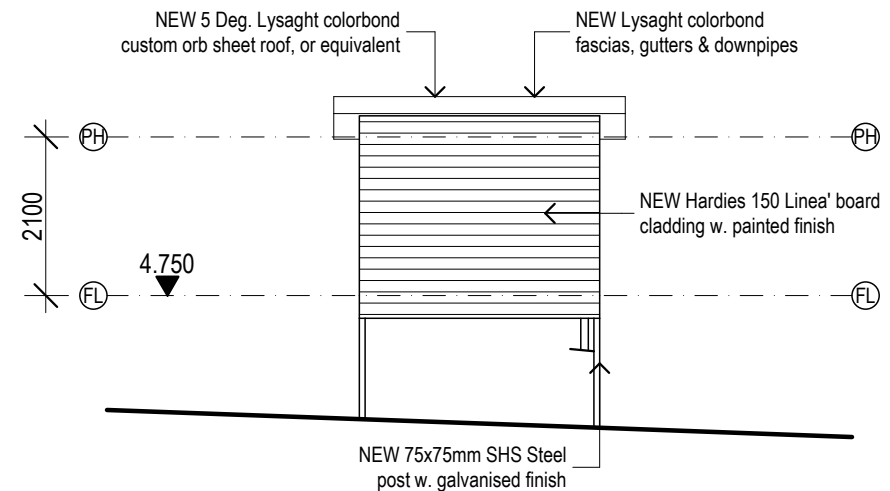

ELEVATION 1 1:100

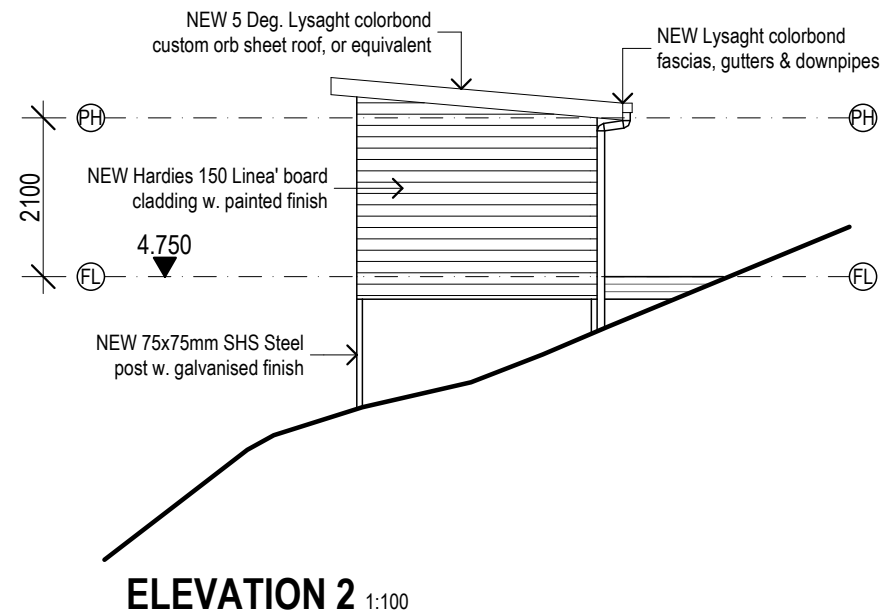


ELEVATION 2 1:100


Veranda Roof -
Min. 2.1 head
height

PRELIMINARY PLANS ONLY NOT FOR CONSTRUCTION

- NOTES:
- *All dimensions to structure only - finishes excluded.
 - *ALL external & internal doors & windows to be measured onsite & confirmed by builder.
 - *Sarking to external walls.
 - *Insulation Req. as per Energy Efficiency Report.
 - *Hot water system shall be heat pump, solar, or gas.
 - *Water supply outlets to have WELs rating.
 - *ALL handrails to be 1000mm above finished floor level.
 - *Bedroom windows w. 2m fall height from FL to ground below must comply with N.C.C 11.3.7. To be fitted with non-removable screens or restricted to 125mm opening.

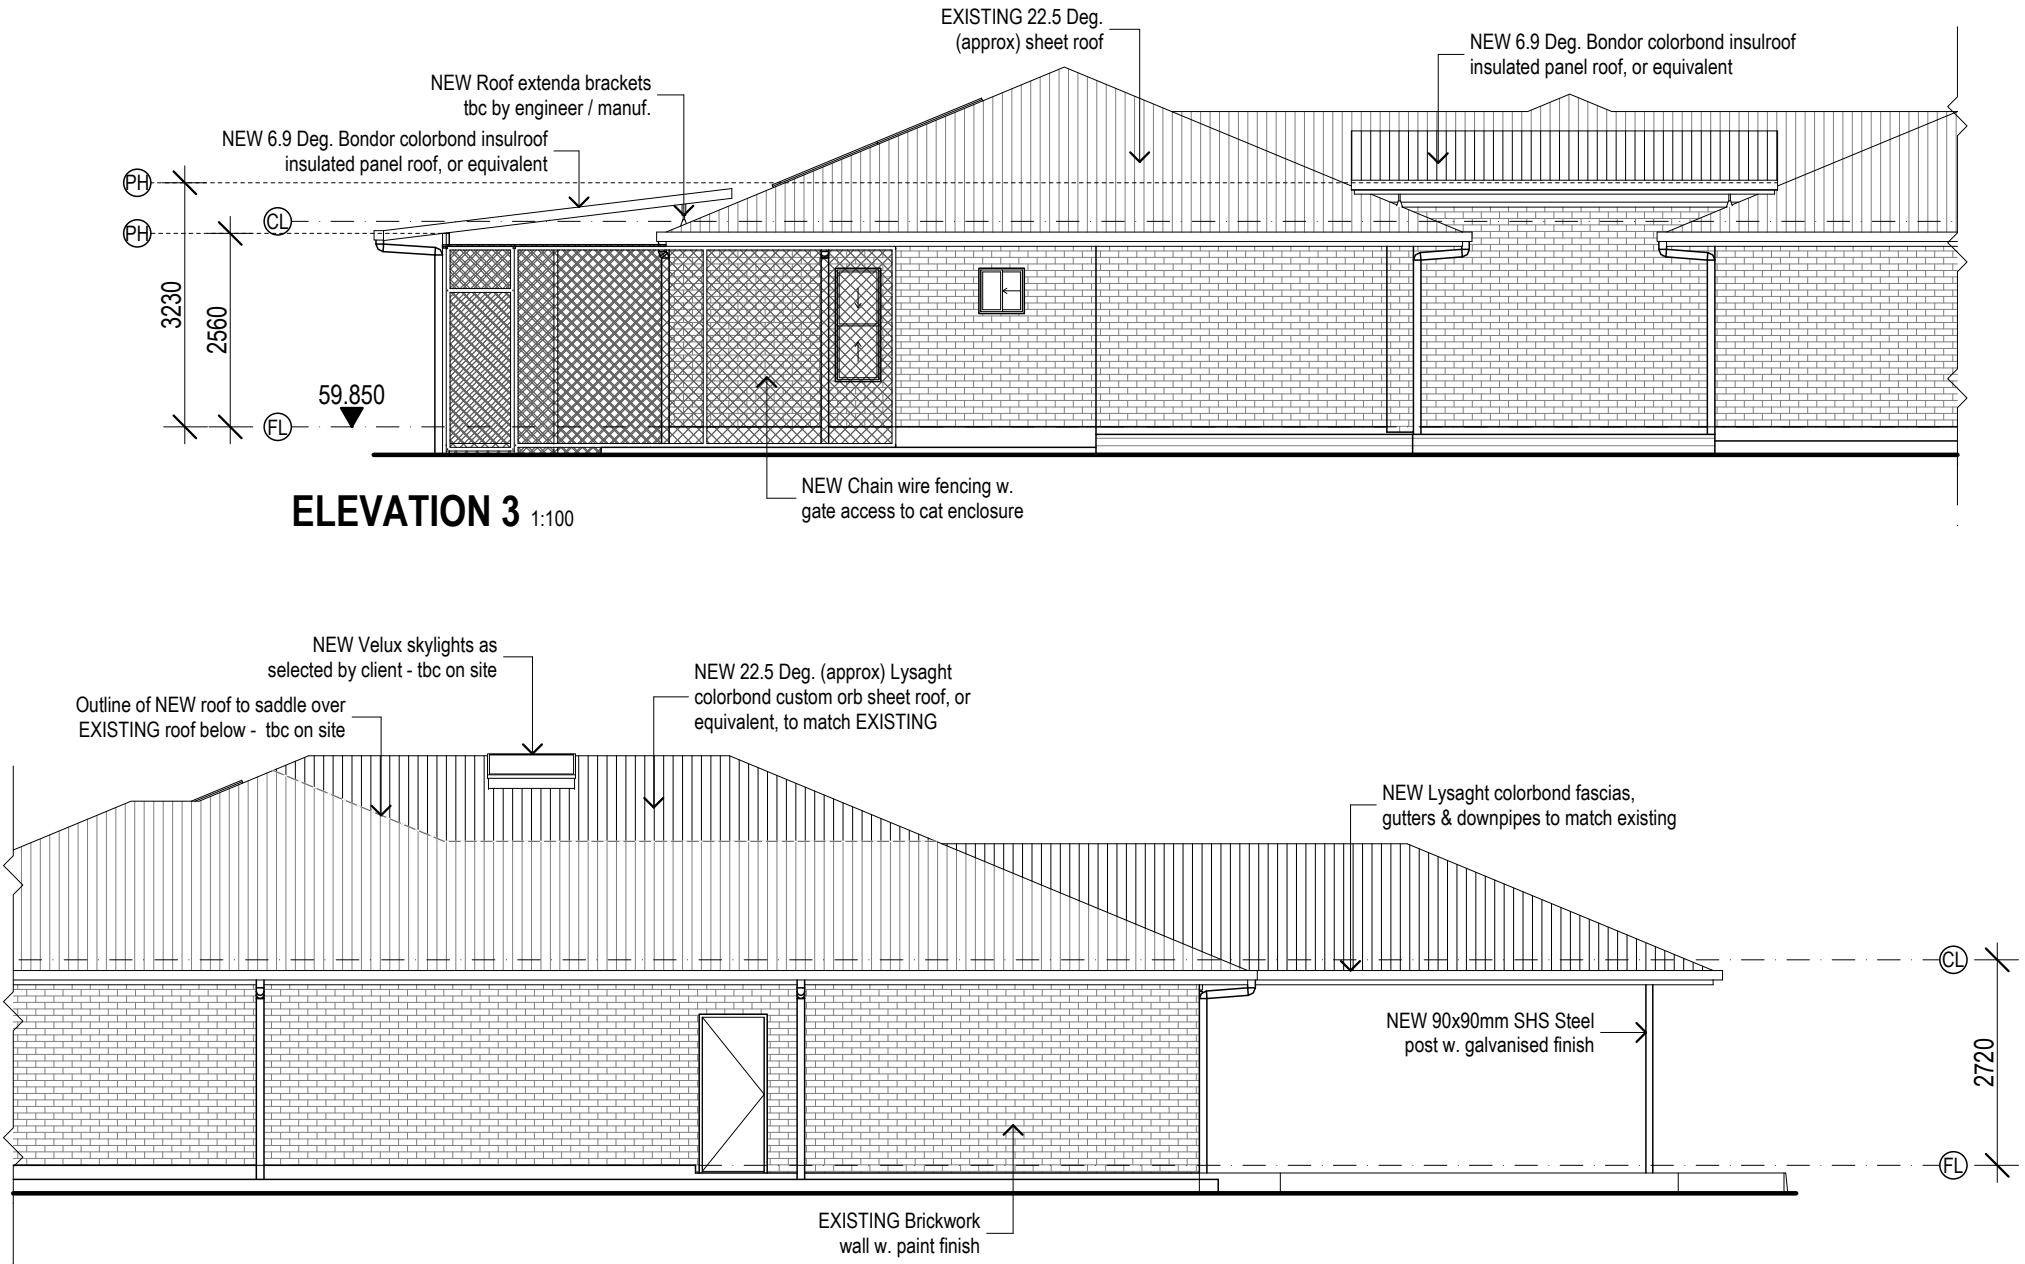

PRELIMINARY PLANS ONLY NOT FOR CONSTRUCTION

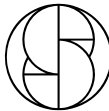

**Stuart
Osman**

P 07 55 203 022
E design@stuartosman.com.au
Studio 2/71 Township Dr,
West Burleigh, QLD 4219
PO BOX 2845
Burleigh Heads DC QLD 4220

BD Building Design
Queensland

**MASTER
BUILDERS
QUEENSLAND**

bda
ASSOCIATION OF AUSTRALIA


ABN 73 097 995 616
QBCC License No: 1129687

PROPOSED RENOVATION

BUILDER: SEEKA
CONSTRUCTIONS
CLIENT: SEEKA
CONSTRUCTIONS
PROJECT: LOT 90 No. 356
RUFFLES RD
WILLOWVALE

DESIGN: CUSTOM
DATE: A01/05/2026
SCALES: 1:100 @ A3
AMENDMENTS:
B250526, C020726,
DRAWN BY: EP/RS SHEET NUMBER: 19 of 24
CHECKED BY: SO JOB NUMBER: **10588**

© Copyright reserved in part or whole.
THIS DESIGN IS THE EXCLUSIVE PROPERTY
OF STUART OSMAN
N.B ALL WRITTEN DIMENSIONS TAKE
PRECEDENCE OVER SCALED SIZES
Contractor to verify dimensions. Notify
designers of discrepancies. Failure to do so
shall void the designers responsibilities.
ALL dimensions to structure only - finishes
excluded. BE WARNED: SUBSTITUTION OF
ANY STRUCTURAL MEMBERS, AND OR ANY
VARIATION TO ANY PART OF THE DESIGN
WILL VOID ANY RESPONSIBILITIES OF
STUART OSMAN FOR THE STRUCTURAL
INTEGRITY AND PERFORMANCE OF THE
BUILDING.

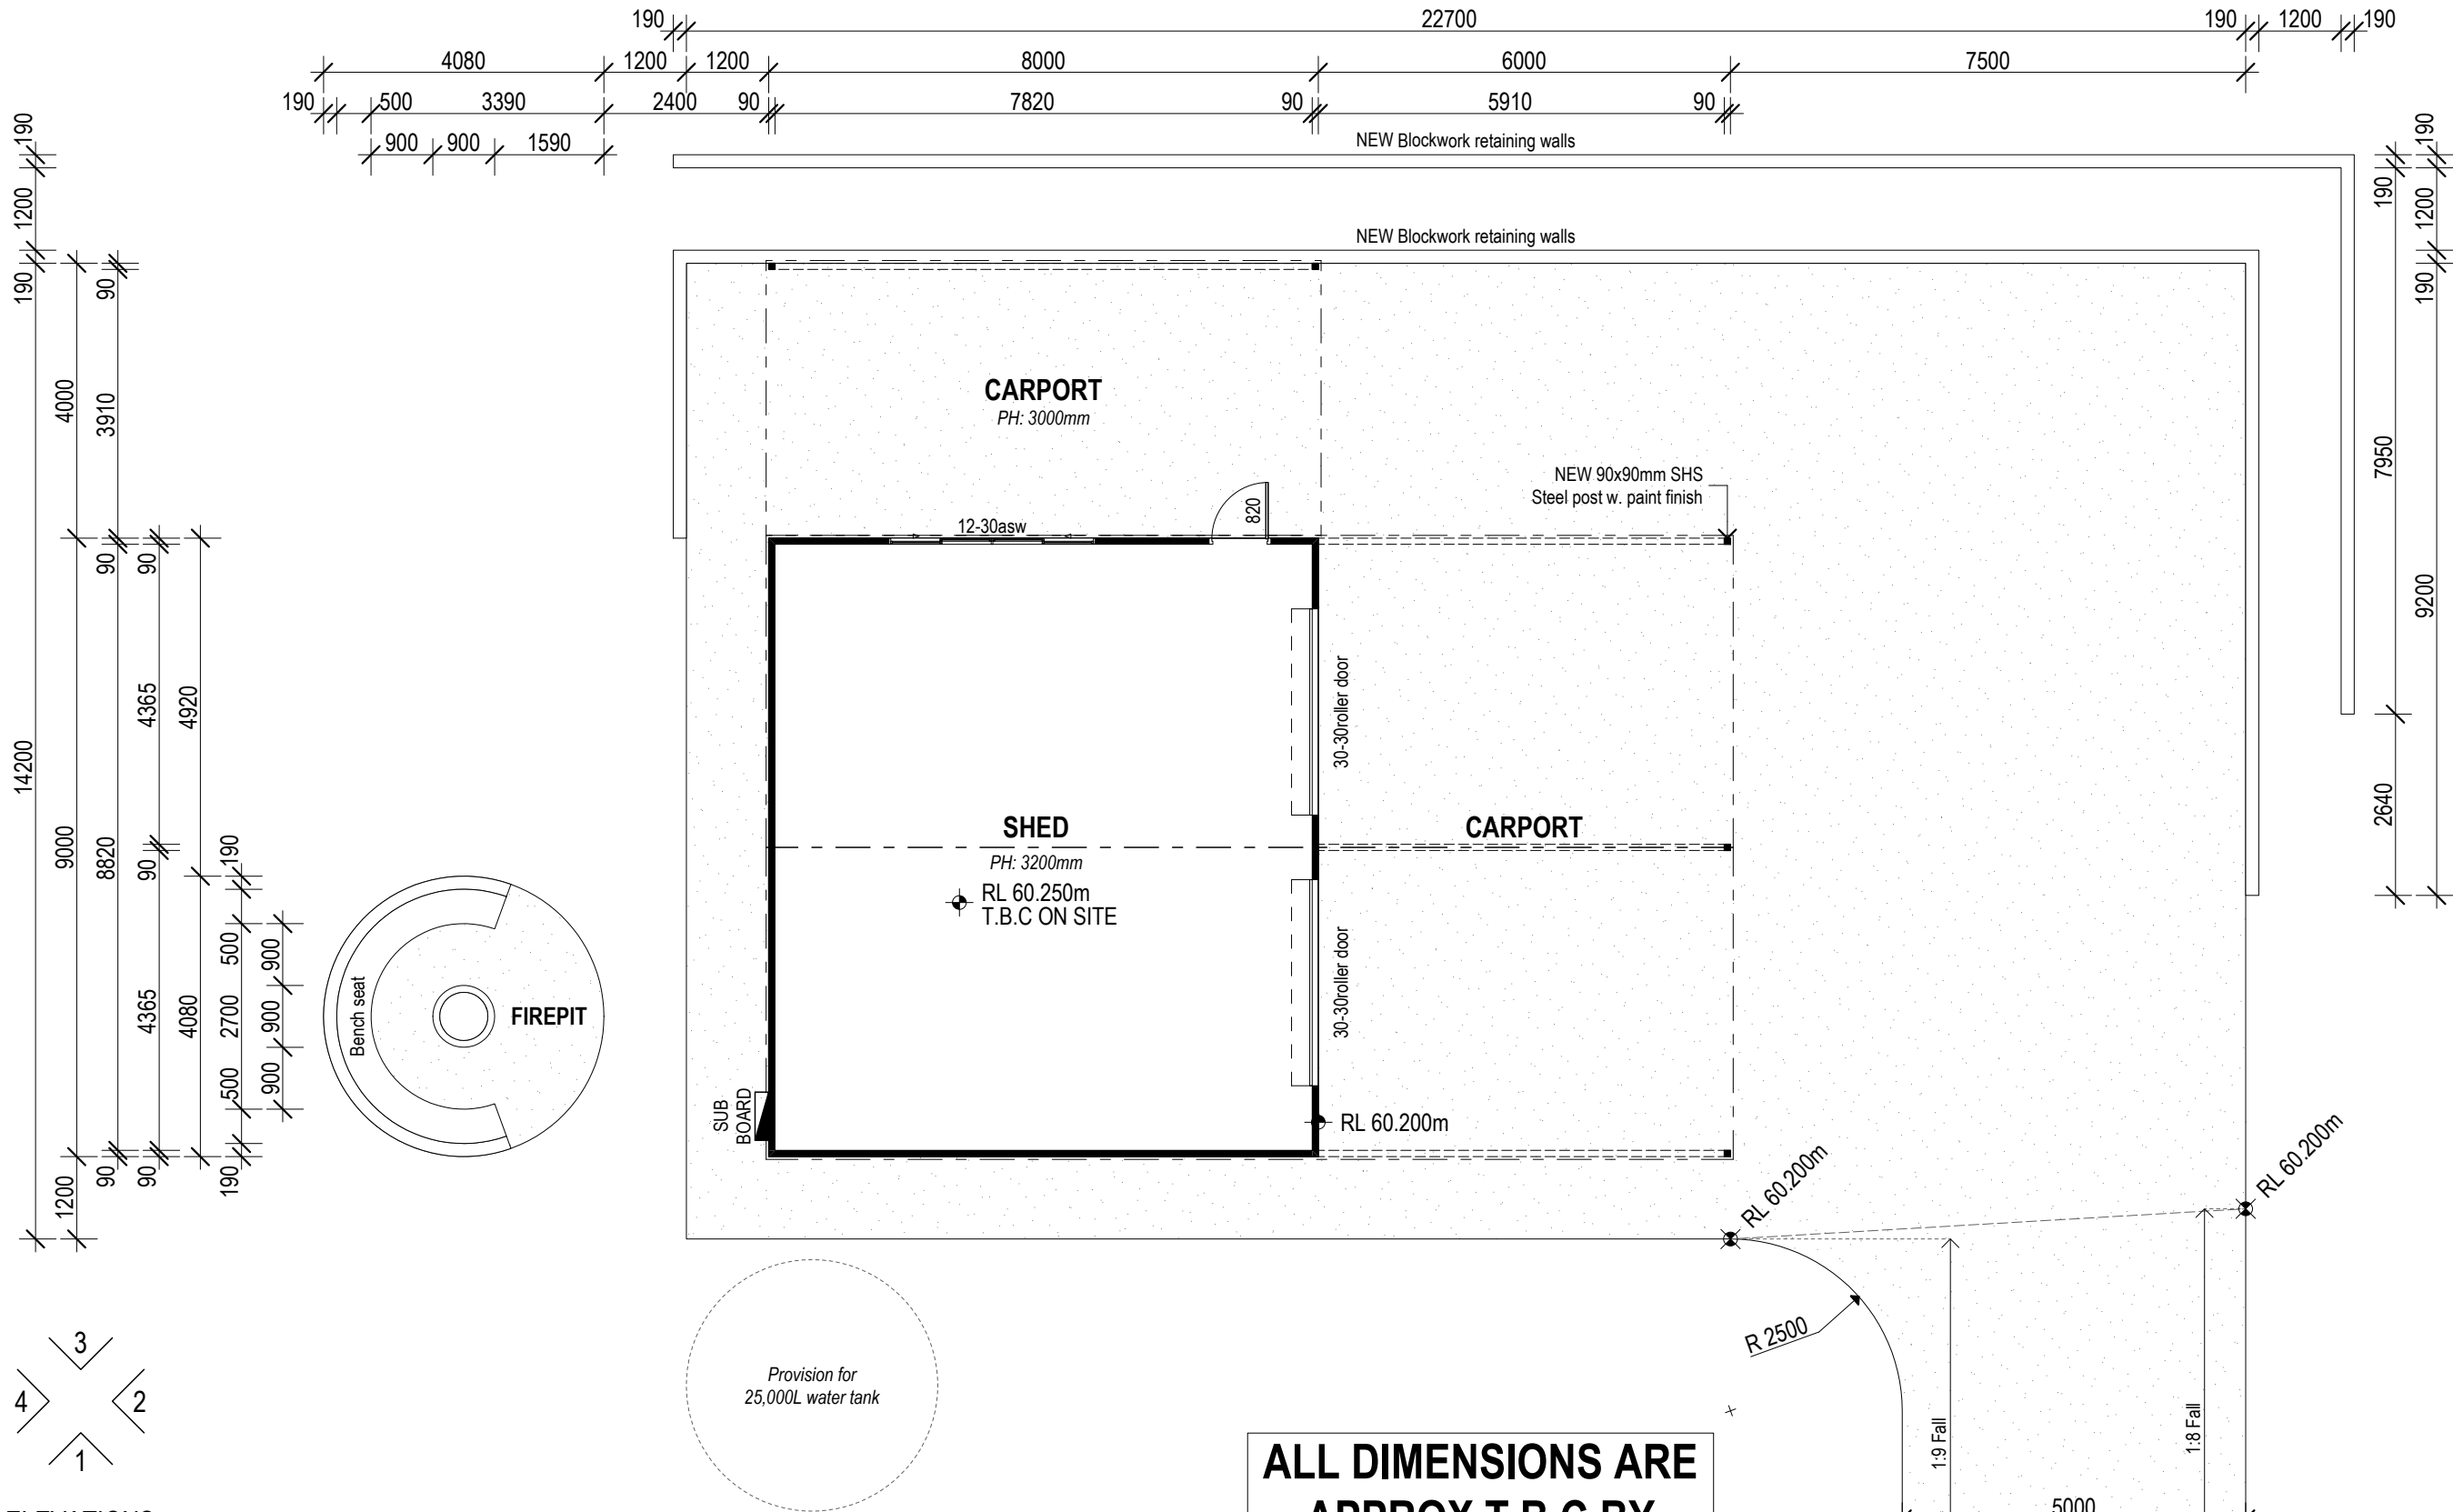

ELEVATIONS

NOTES:

- *All dimensions to structure only - finishes excluded.
- *Lift off hinges to WC door, as per N.C.C 10.4.2.
- *Provide GPO & cold water provisions to DW space.
- *ALL external & internal doors & windows to be measured onsite & confirmed by builder.
- *Sarking to external walls.
- *Insulation Req. as per Energy Efficiency Report.
- *Mechanically vent rooms without natural ventilation.
- *Maximum water supply pressure not to exceed 500kpa at any outlet.
- *ALL shower roses to be AAA rated.
- *Hot water system shall be heat pump, solar, or gas.
- *Water supply outlets to have WELs rating.
- *Toilet cisterns to have dual flush. 6/3 Litre.
- *ALL handrails to be 1000mm above finished floor level.
- *Bedroom windows w. 2m fall height from FL to ground below must comply with N.C.C 11.3.7. To be fitted with non-removable screens or restricted to 125mm opening.
- *If more than one smoke alarm is required they must be interconnected as per N.C.C 9.5.1, & comply with AS 3786.


PROPOSED SHED FLOOR PLAN

SCALE 1:100

PROPOSED FLOOR AREAS

	Area (m2)
GROUND FLOOR LIVING	287.97
GARAGE	41.69
CARPORT	39.00
PORCH	11.42
PATIO	32.10
CAT ENCLOSURE	17.22
GOAT SHACK	10.11
SHED / CARPORTS	158.00
TOTAL	597.51 m ²

ALL DIMENSIONS ARE
APPROX T.B.C BY
BUILDER ONSITE

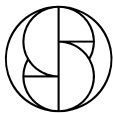

Stuart
Osman

P 07 55 203 022
E design@stuartosman.com.au
Studio 2/71 Township Dr,
West Burleigh, QLD 4219
PO BOX 2845
Burleigh Heads DC QLD 4220

BD Building Design
Queensland

MASTER
BUILDERS
QUEENSLAND

bdqa
BUILDING DESIGNERS
ASSOCIATION OF AUSTRALIA

ABN 73 097 995 616
QBCC License No: 1129687

PROPOSED RENOVATION


BUILDER:	SEEKA CONSTRUCTIONS	DESIGN:	CUSTOM
CLIENT:	SEEKA CONSTRUCTIONS	DATE:	A01/05/2026
PROJECT:	LOT 90 No. 356 RUFFLES RD WILLOWVALE	SCALES:	1:100 @ A3
DRAWN BY:	EP/RS	AMENDMENTS:	B250526, C020726,
CHECKED BY:	SO	SHEET NUMBER:	20 of 24
		JOB NUMBER:	10588

© Copyright reserved in part or whole.
THIS DESIGN IS THE EXCLUSIVE PROPERTY
OF STUART OSMAN
N.B ALL WRITTEN DIMENSIONS TAKE
PRECEDENCE OVER SCALED SIZES
Contractor to verify dimensions. Notify
designers of discrepancies. Failure to do so
shall void the designers responsibilities.
ALL dimensions to structure only - finishes
excluded. BE WARNED: SUBSTITUTION OF
ANY STRUCTURAL MEMBERS, AND OR ANY
VARIATION TO ANY PART OF THE DESIGN
WILL VOID ANY RESPONSIBILITIES OF
STUART OSMAN FOR THE STRUCTURAL
INTEGRITY AND PERFORMANCE OF THE
BUILDING.


PRELIMINARY PLANS ONLY NOT FOR CONSTRUCTION

PRELIMINARY PLANS ONLY NOT FOR CONSTRUCTION


NOTES:
*All dimensions to structure only - finishes excluded.
*ALL external & internal doors & windows to be measured onsite & confirmed by builder.
*Sarking to external walls.
*Insulation Req. as per Energy Efficiency Report.
*Hot water system shall be heat pump, solar, or gas.
*Water supply outlets to have WELs rating.
*ALL handrails to be 1000mm above finished floor level.
*Bedroom windows w. 2m fall height from FL to ground below must comply with N.C.C 11.3.7. To be fitted with non-removable screens or restricted to 125mm opening.

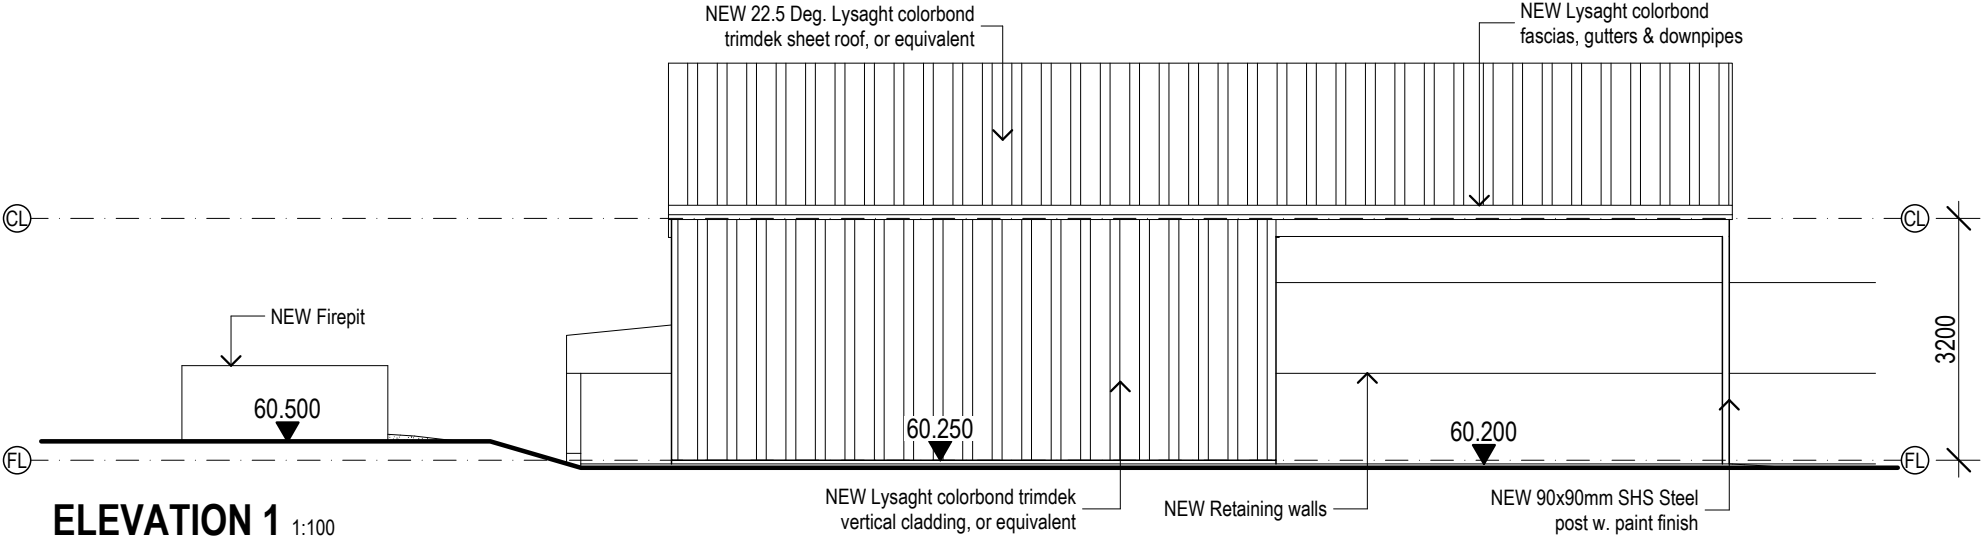


ELEVATION 1 1:100

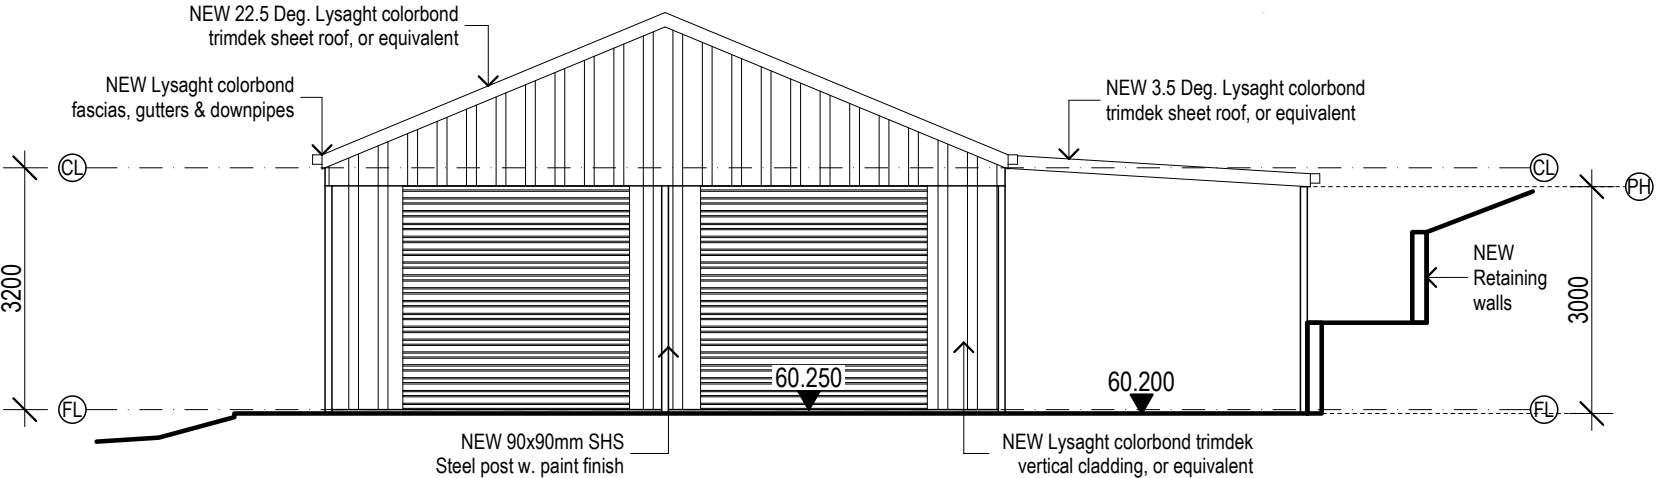

ELEVATION 2 1:100

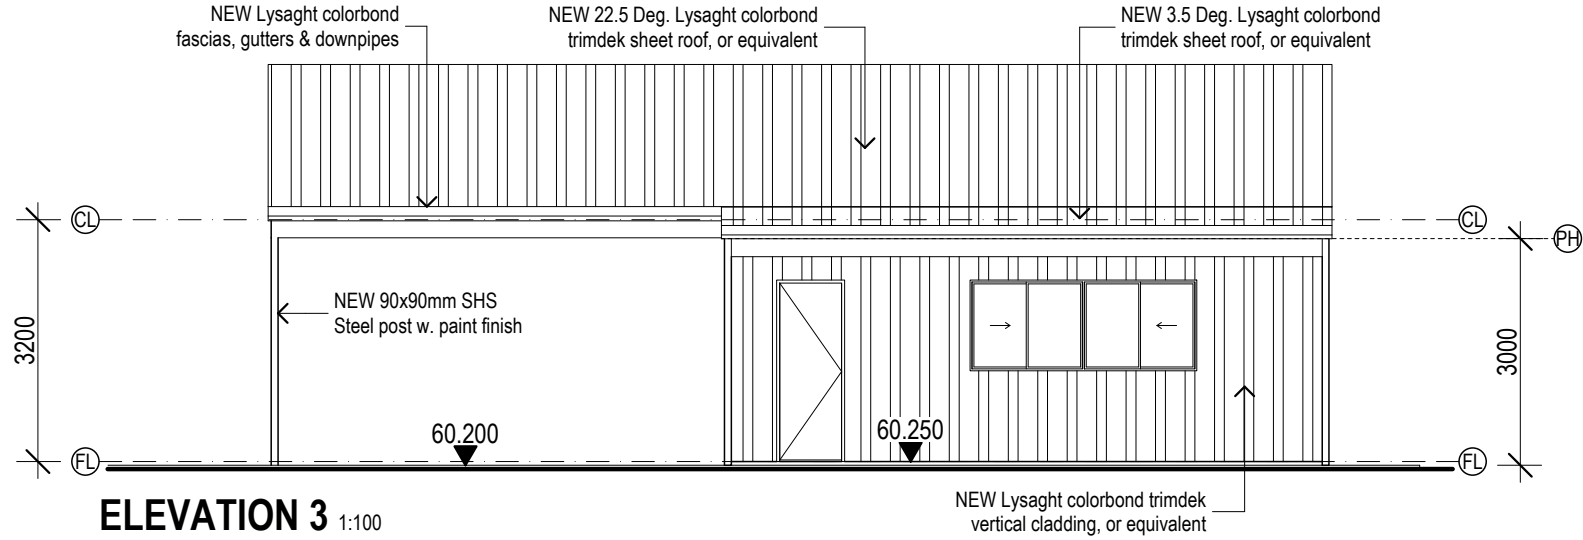

ELEVATION 3 1:100

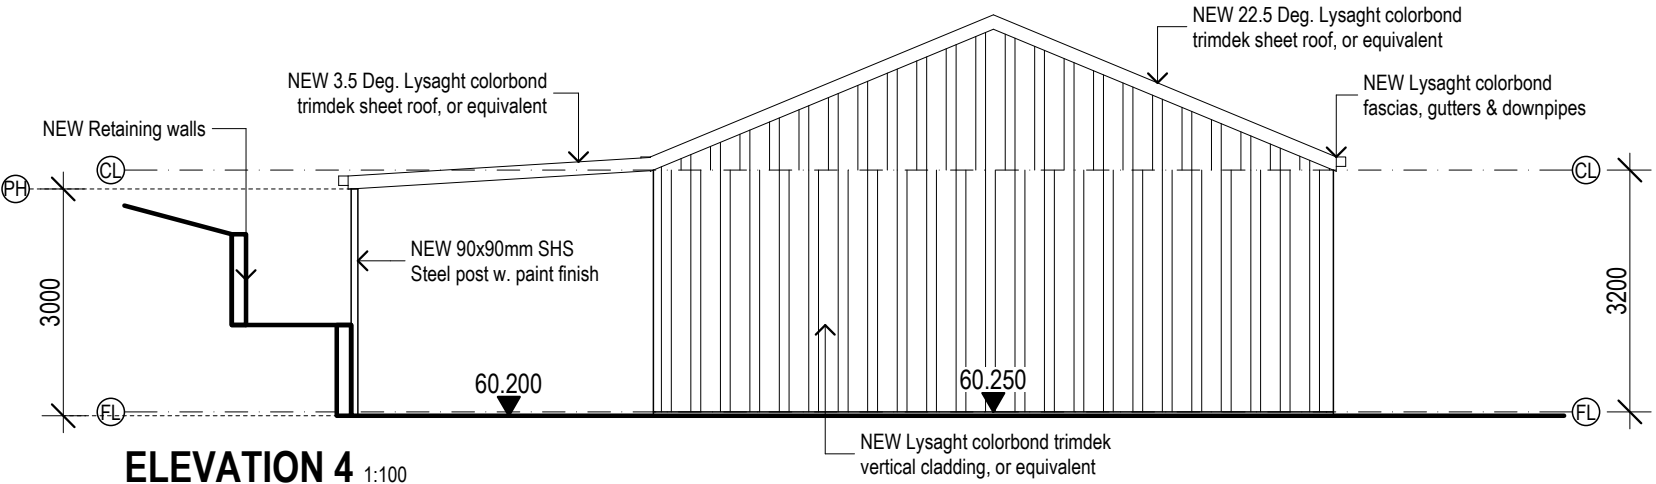

ELEVATION 4 1:100



P 07 55 203 022
E design@stuartosman.com.au

Studio 2/71 Township Dr,
West Burleigh, QLD 4219

PO BOX 2845
Burleigh Heads DC QLD 4220

ABN 73 097 995 616
QBCC License No: 1129687



PROPOSED RENOVATION

BUILDER:SEEKA CONSTRUCTIONS

CLIENT: SEEKA CONSTRUCTIONS

PROJECT: LOT 90 No. 356
RUFFLES RD
WILLOWVALE

DRAWN BY: EP/RS

CHECKED BY: SO

DESIGN: CUSTOM

DATE: A01/05/2026

SCALES: 1:100 @ A3

AMENDMENTS:
B250526, C020726,

SHEET NUMBER: 22 of 24

JOB NUMBER: 10588

© Copyright reserved in part or whole.
THIS DESIGN IS THE EXCLUSIVE PROPERTY
OF STUART OSMAN
N.B ALL WRITTEN DIMENSIONS TAKE
PRECEDENCE OVER SCALED SIZES
Contractor to verify dimensions. Notify
designers of discrepancies. Failure to do so
shall void the designers responsibilities.
ALL dimensions to structure only - finishes
excluded. BE WARNED: SUBSTITUTION OF
ANY STRUCTURAL MEMBERS, AND OR ANY
VARIATION TO ANY PART OF THE DESIGN
WILL VOID ANY RESPONSIBILITIES OF STUART
OSMAN FOR THE STRUCTURAL INTEGRITY
AND PERFORMANCE OF THE BUILDING.

PRELIMINARY PLANS ONLY NOT FOR CONSTRUCTION



P 07 55 203 022
E design@stuartosman.com.au

Studio 2/71 Township Dr,
West Burleigh, QLD 4219

PO BOX 2845
Burleigh Heads DC QLD 4220

ABN 73 097 995 616
QBCC License No: 1129687



PROPOSED RENOVATION

BUILDER:SEEKA CONSTRUCTIONS

CLIENT: SEEKA CONSTRUCTIONS

PROJECT: LOT 90 No. 356
RUFFLES RD
WILLOWVALE

DRAWN BY: EP/RS

CHECKED BY: SO

DESIGN: CUSTOM

DATE: A01/05/2026



SCALES: @ A3

AMENDMENTS:
B250526, C020726,

SHEET NUMBER: 23 of 24

JOB NUMBER: **10588**

© Copyright reserved in part or whole.
THIS DESIGN IS THE EXCLUSIVE PROPERTY
OF STUART OSMAN
N.B ALL WRITTEN DIMENSIONS TAKE
PRECEDENCE OVER SCALED SIZES
Contractor to verify dimensions. Notify
designers of discrepancies. Failure to do so
shall void the designers responsibilities.
ALL dimensions to structure only - finishes
excluded. BE WARNED: SUBSTITUTION OF
ANY STRUCTURAL MEMBERS, AND OR ANY
VARIATION TO ANY PART OF THE DESIGN
WILL VOID ANY RESPONSIBILITIES OF STUART
OSMAN FOR THE STRUCTURAL INTEGRITY
AND PERFORMANCE OF THE BUILDING.

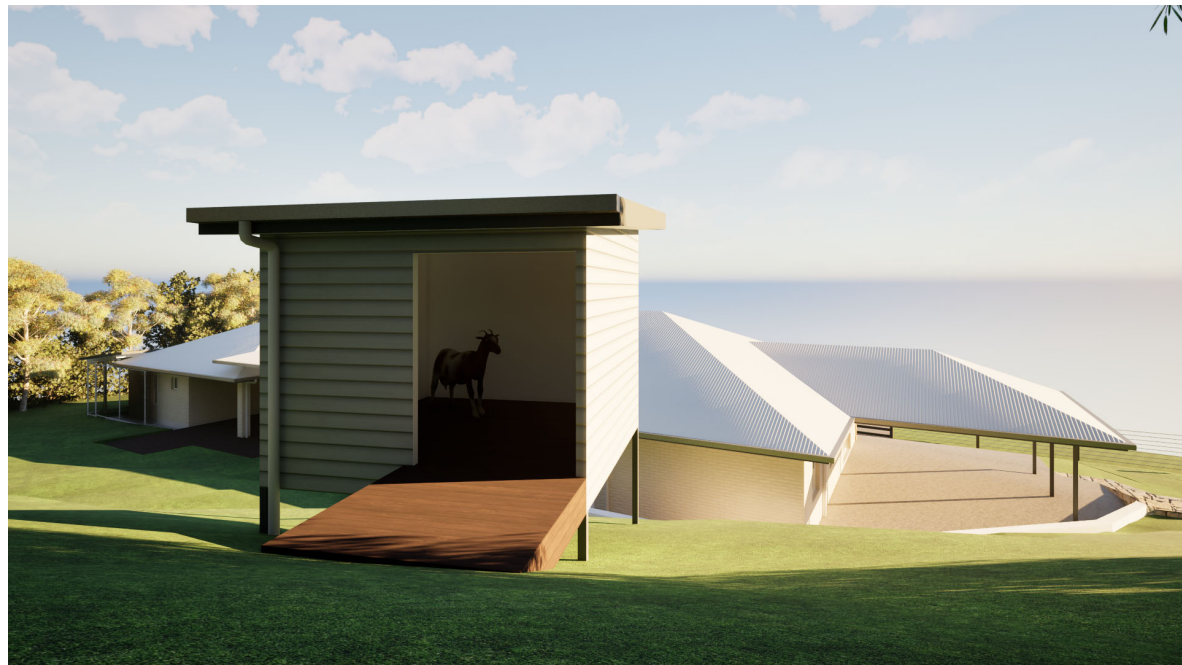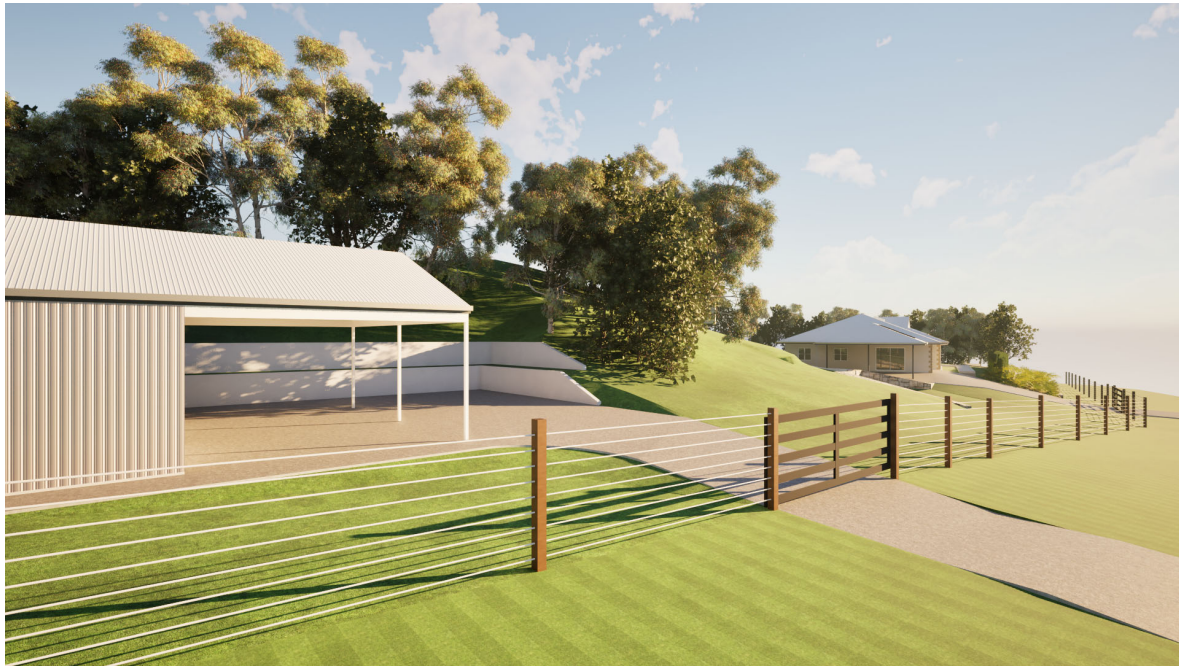

PROPOSED RENOVATION

BUILDER:SEEKA CONSTRUCTIONS

CLIENT: SEEKA CONSTRUCTIONS

PROJECT: LOT 90 No. 356
RUFFLES RD
WILLOWVALE

DRAWN BY: EP/RS

CHECKED BY: SO

DESIGN: CUSTOM

DATE: A01/05/2026

SCALES: @ A3

AMENDMENTS:
B250526, C020726,

SHEET NUMBER: 24 of 24

JOB NUMBER: **10588**

© Copyright reserved in part or whole.
THIS DESIGN IS THE EXCLUSIVE PROPERTY
OF STUART OSMAN
N.B ALL WRITTEN DIMENSIONS TAKE
PRECEDENCE OVER SCALED SIZES
Contractor to verify dimensions. Notify
designers of discrepancies. Failure to do so
shall void the designers responsibilities.
ALL dimensions to structure only - finishes
excluded. BE WARNED: SUBSTITUTION OF
ANY STRUCTURAL MEMBERS, AND OR ANY
VARIATION TO ANY PART OF THE DESIGN
WILL VOID ANY RESPONSIBILITIES OF STUART
OSMAN FOR THE STRUCTURAL INTEGRITY
AND PERFORMANCE OF THE BUILDING.