



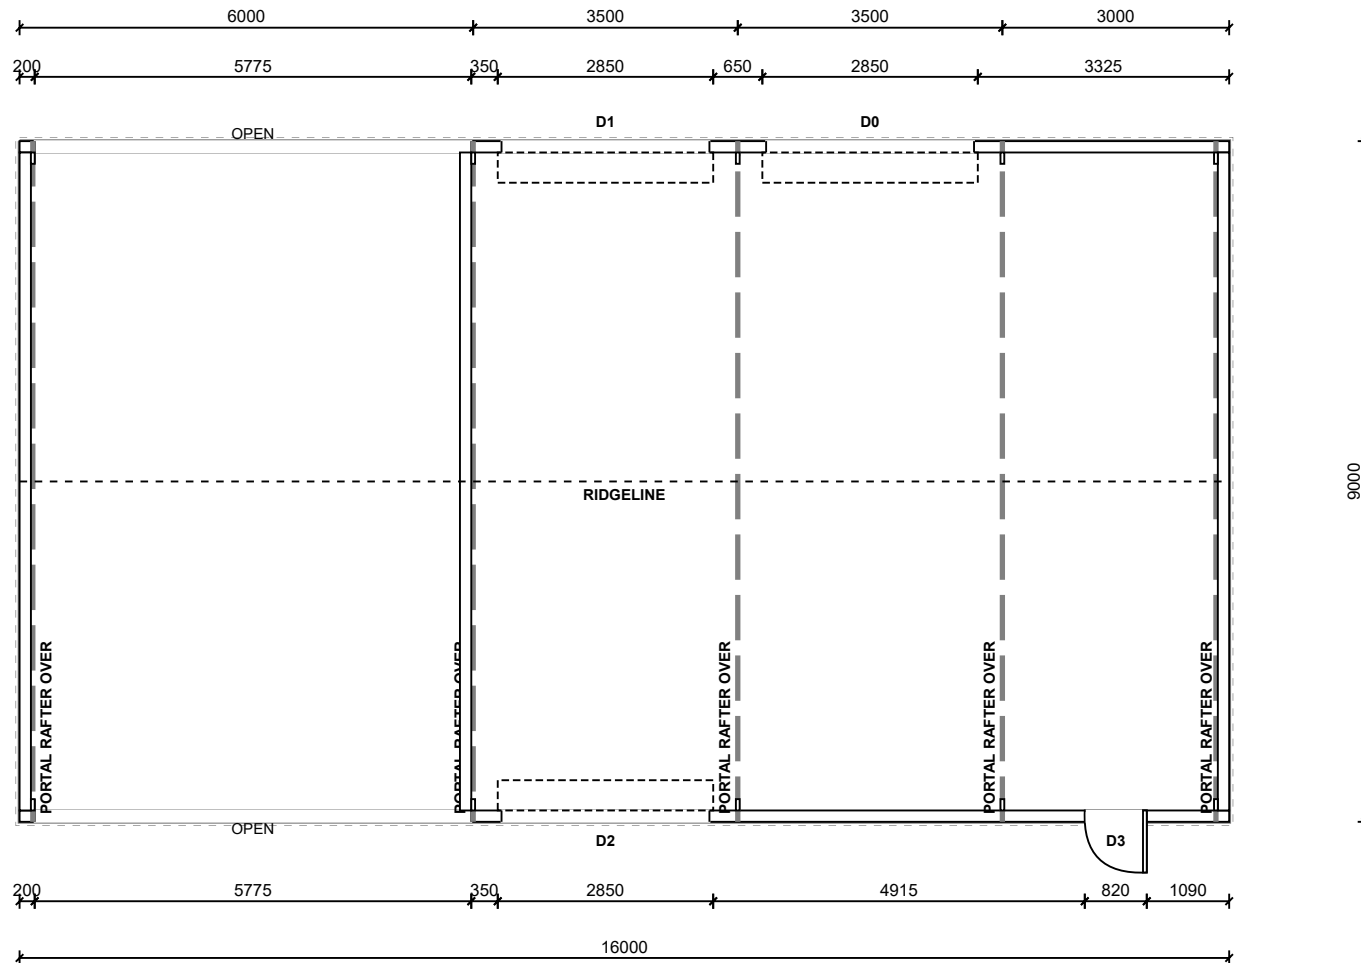

FLOORPLAN
SCALE 1:100

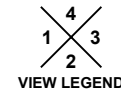

REFER TO CONSTRUCTION DRAWING FOR SLAB/FOOTING LAYOUT

OPENING SCHEDULE				
MARK	TYPE	HEIGHT	WIDTH	DESCRIPTION
D0-1	ROLLER DOOR	3400	2850	COLORBOND® STRAMIT RAD B - ROLLER DOOR
D2	ROLLER DOOR	3000	2850	COLORBOND® STRAMIT RAD A - ROLLER DOOR
D3	PA DOOR	2040	820	COLORBOND® PERSONAL ACCESS DOOR

North VIC Sheds
69 Victoria Street
Kerang, 3579
P: 03 5452 2255
F:



client
Craig Jane Manners

project
Proposed Garage: Sturdy
5 Forest Street
Barham, VIC, 2732

Drawing Name
Floor Plan

Project Number
NVSK - 10784C - 2

Drawn
1:100

Date
07/11/2025


Sheet
16Lx9Wx4.2H|10°|4bays

Rev.


Copyright © 2019 by A-Line Building Systems Pty Ltd.
The concepts and information contained in this document are the intellectual property of A-Line Building Systems Pty Ltd. Use or copying of the document in whole or in part without written permission of A-Line Building Systems Pty Ltd constitutes an infringement of copyright

All Dimensions In Millimetres U.N.O.

Sheet Size
A4

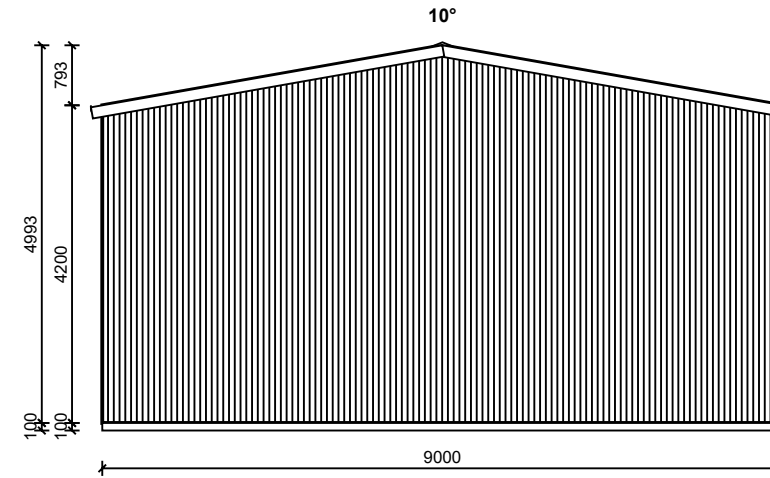

1. FRONT ELEVATION
SCALE 1:100

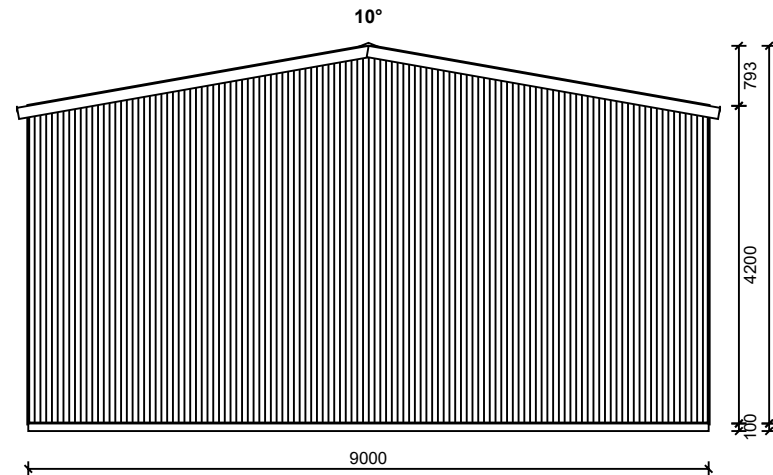


3. REAR ELEVATION
SCALE 1:100


REFER TO CONSTRUCTION DRAWING FOR SLAB/FOOTING LAYOUT

OPENING SCHEDULE				
MARK	TYPE	HEIGHT	WIDTH	DESCRIPTION
D0-1	ROLLER DOOR	3400	2850	COLORBOND® STRAMIT RAD B - ROLLER DOOR
D2	ROLLER DOOR	3000	2850	COLORBOND® STRAMIT RAD A - ROLLER DOOR
D3	PA DOOR	2040	820	COLORBOND® PERSONAL ACCESS DOOR

North VIC Sheds 69 Victoria Street Kerang, 3579 P: 03 5452 2255 F:		 		client Craig Jane Manners project Proposed Garage: Sturdy 5 Forest Street Barham, VIC, 2732	
Drawing Name End Elevation		Project Number NVSK - 10784C - 2		Drawing Number _____	
Drawn _____		Date 07/11/2025		Rev. _____	
Copyright © 2019 by A-Line Building Systems Pty Ltd. The concepts and information contained in this document are the intellectual property of A-Line Building Systems Pty Ltd. Use or copying of the document in whole or in part without written permission of A-Line Building Systems Pty Ltd constitutes an infringement of copyright				All Dimensions In Millimetres U.N.O. Scale: 1:100	
				Sheet Size A4	

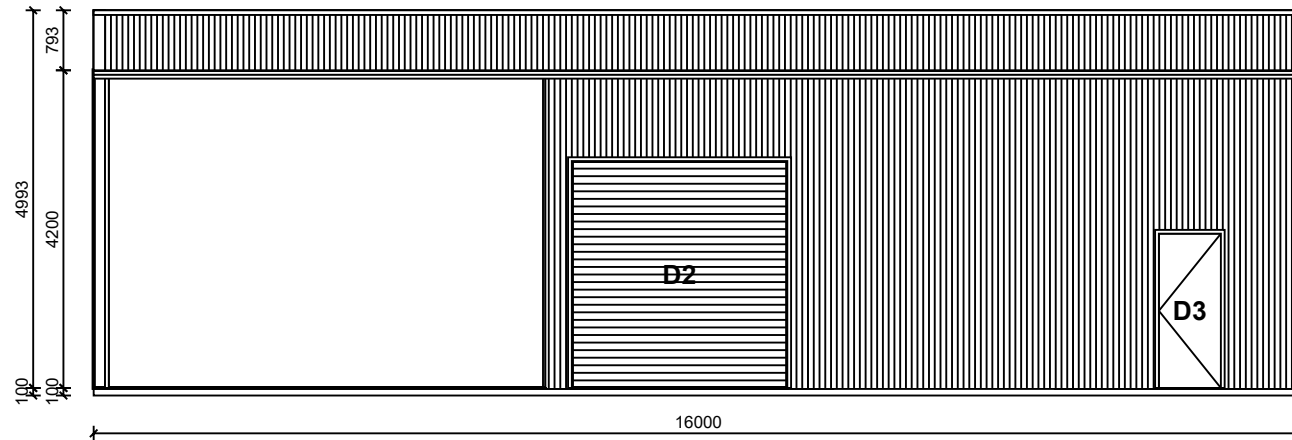

2. RIGHT ELEVATION
SCALE 1:100

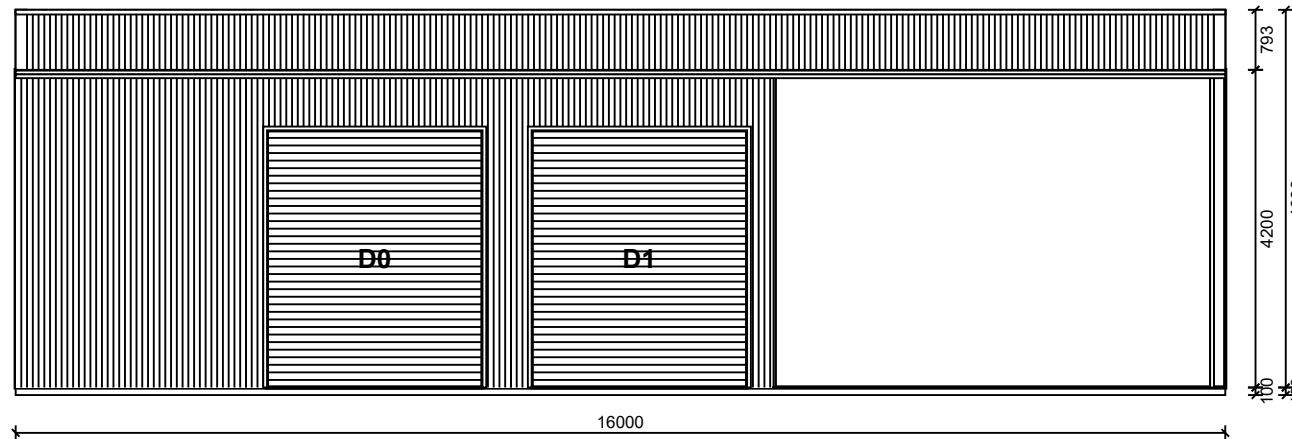


4. LEFT ELEVATION
SCALE 1:100

REFER TO CONSTRUCTION DRAWING FOR SLAB/FOOTING LAYOUT

OPENING SCHEDULE				
MARK	TYPE	HEIGHT	WIDTH	DESCRIPTION
D0-1	ROLLER DOOR	3400	2850	COLORBOND® STRAMIT RAD B - ROLLER DOOR
D2	ROLLER DOOR	3000	2850	COLORBOND® STRAMIT RAD A - ROLLER DOOR
D3	PA DOOR	2040	820	COLORBOND® PERSONAL ACCESS DOOR

North VIC Sheds 69 Victoria Street Kerang, 3579 P: 03 5452 2255 F:		 		client Craig Jane Manners project Proposed Garage: Sturdy 5 Forest Street Barham, VIC, 2732	
Drawing Name: Side Elevation		Project Number: NVSK - 10784C - 2		Drawing Number:	
Drawn:		Date: 07/11/2025		Rev:	
Copyright © 2019 by A-Line Building Systems Pty Ltd. The concepts and information contained in this document are the intellectual property of A-Line Building Systems Pty Ltd. Use or copying of the document in whole or in part without written permission of A-Line Building Systems Pty Ltd constitutes an infringement of copyright		All Dimensions in Millimetres U.N.O.		Sheet Size A4	
Scale: 1:100		Sheet: 16Lx9Wx4.2H 10° 4bays			

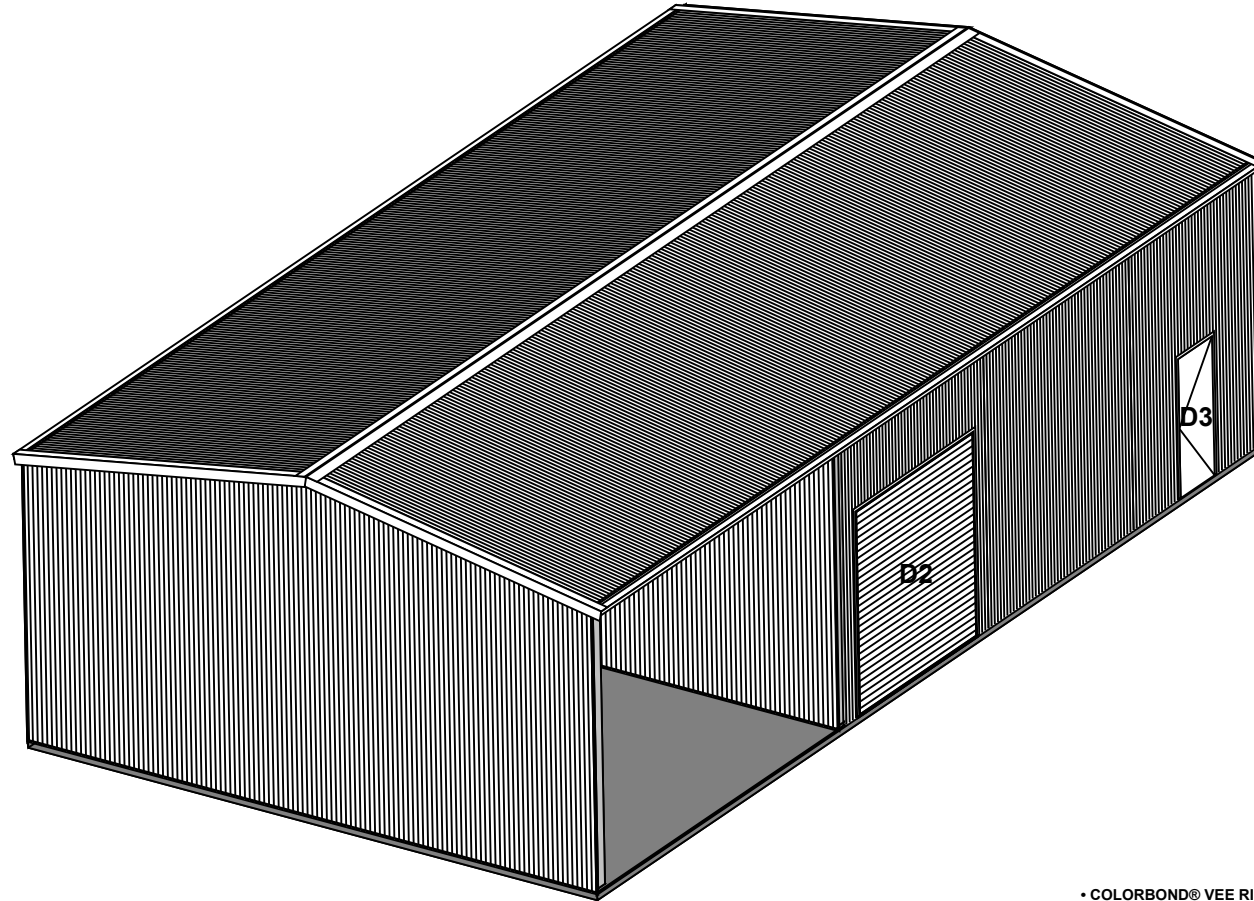

FRONT RIGHT ELEVATION
SCALE 1:100

- COLORBOND® VEE RIDGE CAPPING
- COLORBOND® 0.47 TCT CORRUGATED ROOF CLADDING
- COLORBOND® GARAGE BARGE FLASHING
- COLORBOND® QUAD 115 EAVE GUTTER
- WHITE UPVC 90D DOWNPIPE
- COLORBOND® 0.47 TCT CORRUGATED WALL CLADDING
- COLORBOND® CORNER FLASHING

OPENING SCHEDULE				
MARK	TYPE	HEIGHT	WIDTH	DESCRIPTION
D0-1	ROLLER DOOR	3400	2850	COLORBOND® STRAMIT RAD B - ROLLER DOOR
D2	ROLLER DOOR	3000	2850	COLORBOND® STRAMIT RAD A - ROLLER DOOR
D3	PA DOOR	2040	820	COLORBOND® PERSONAL ACCESS DOOR

North VIC Sheds


69 Victoria Street
Kerang, 3579
P: 03 5452 2255
F:



Copyright © 2019 by A-Line Building Systems Pty Ltd.
The concepts and information contained in this document are the intellectual property of A-Line Building Systems Pty Ltd. Use or copying of the document in whole or in part without written permission of A-Line Building Systems Pty Ltd constitutes an infringement of copyright

client Craig Jane Manners		project Proposed Garage: Sturdy 5 Forest Street Barham, VIC, 2732	
Drawing Name: ISO		Rev:	
Drawing Number: NVSK - 10784C - 2		Date: 07/11/2025	
Scale: 1:100		Sheet Size A4	
All Dimensions in Millimetres U.N.O.		Sheet: 16Lx9Wx4.2H 10° 4bays	

REFER TO CONSTRUCTION DRAWING FOR SLAB/FOOTING LAYOUT

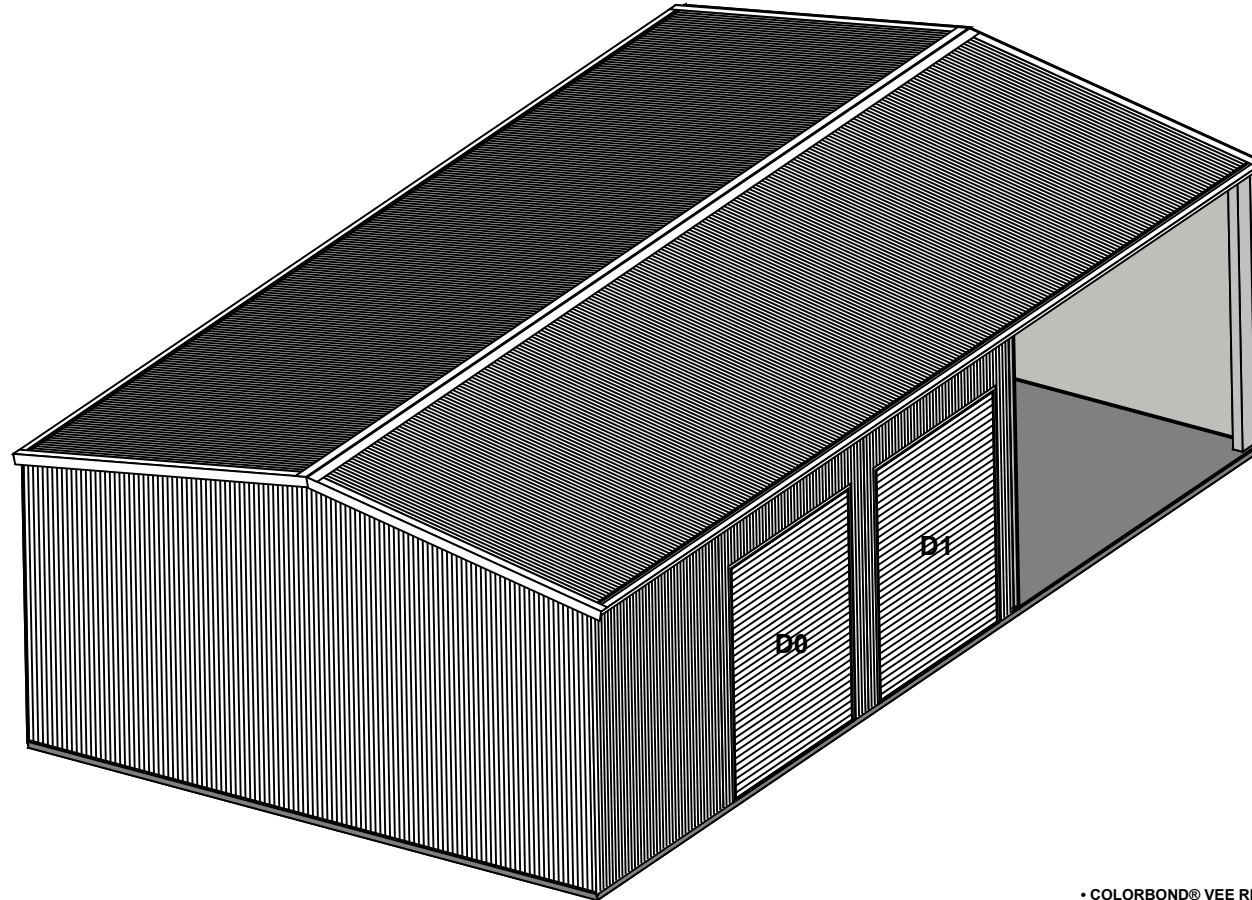

REAR LEFT ELEVATION
SCALE 1:100

- COLORBOND® VEE RIDGE CAPPING
- COLORBOND® 0.47 TCT CORRUGATED ROOF CLADDING
- COLORBOND® GARAGE BARGE FLASHING
- COLORBOND® QUAD 115 EAVE GUTTER
- WHITE UPVC 90D DOWNPIPE
- COLORBOND® 0.47 TCT CORRUGATED WALL CLADDING
- COLORBOND® CORNER FLASHING

REFER TO CONSTRUCTION DRAWING FOR SLAB/FOOTING LAYOUT

OPENING SCHEDULE				
MARK	TYPE	HEIGHT	WIDTH	DESCRIPTION
D0-1	ROLLER DOOR	3400	2850	COLORBOND® STRAMIT RAD B - ROLLER DOOR
D2	ROLLER DOOR	3000	2850	COLORBOND® STRAMIT RAD A - ROLLER DOOR
D3	PA DOOR	2040	820	COLORBOND® PERSONAL ACCESS DOOR

North VIC Sheds

69 Victoria Street
Kerang, 3579
P: 03 5452 2255
F:



Copyright © 2019 by A-Line Building Systems Pty Ltd.
The concepts and information contained in this document are the intellectual property of A-Line Building Systems Pty Ltd. Use or copying of the document in whole or in part without written permission of A-Line Building Systems Pty Ltd constitutes an infringement of copyright

client Craig Jane Manners		project Proposed Garage: Sturdy 5 Forest Street Barham, VIC, 2732	
Drawing Name: Iso			
Project Number: NVSK - 10784C - 2		Drawing Number:	Rev.
Drawn: NVSK	Date: 07/11/2025		
All Dimensions in Millimetres U.N.O.			Sheet Size
Scale: 1:100	Sheet: 16Lx9Wx4.2H 10° 4bays		A4